

Elevator Electrical Attached Document

Drawing No. : GR30023AA. SJ01 (A) –FB (EN)

Version: A Modify: 0

Scope of application:

GRP GRPS GRPN GRB GRBS GRBN

GRO GROS GRON GRF GRFS GRFN



Sicher Elevator Co., LTD

■ Electric Principle Diagram

GR30023AA–YL01–FB (EN)

■ Prefabricated Cable Diagram

GR31423AA–DL01. EN (A)

■ Commissioning instruction

Design: Xinfengluo 07/10/2021

Check: JianxueShen 07/10/2021

Approve: XiaoyingRu 07/10/2021

Electric Principle Diagram

Control system: RH6000

Drawing No. : GR30023AA-YL01-FB (EN)

Version: A

Scope of application: GRPS\GROS\GRBS
GRPN\GRON\GRBN
GRF\GRFS\GRFN

Design: XinfengLuo 25/09/2021

Check: JianxueShen 25/09/2021

Standardize: GuopingZhou 25/09/2021

Approve: XiaoyingRu 25/09/2021

Sicher Elevator CO., LTD

1

2

3

4

D

C

B

A

Catalog

Page	Content	Remarks	Page	Content	Remarks
1	Drawing catalog		14	Car top control board circuit	
2	Drawing description & changed Record		15	Main operation box control circuit	
3	Components code list		16	Auxiliary operation box control circuit	
3A	Components code list				
4	Main circuit(Geared)		17	Disabled operation box control circuit	When no auxiliary operation box, it need to connect to CN8.
4A	Main circuit(Gearless)	The control relay completes the star sealing function			
4B	Main circuit(Gearless)	The star sealing contactor completes the star sealing function	17A	Disabled operation box control circuit	When has auxiliary operation box, the buttons are connected in parallel.
5	Control power supply circuit				
6	Safety door lock circuit	Single door	18	Landing communication	
6A	Safety door lock circuit	Double door	19	Combined landing call box control circuit	
7	Brake circuit/Emergency brake release device circuit				
8	PC input circuit	Single door	20	Parallel circuit(CAN2)	
8A	PC input circuit	Double door	20A	Parallel circuit(232-485)	
9	PC output circuit(Gearless)	Single door	21	Group control circuit	
9A	PC output circuit(Gearless)	Double door	22	Door machine control circuit	NSFC01-01, AAD03010, NOMJ-01
9B	PC output circuit(Gearless)	Single door	22A	Door machine control circuit	NSFC01-02
9C	PC output circuit(Gearless)	Double door	22B	Door machine control circuit	ACVF003C
9D	PC output circuit(Geared)	Single door	22C	Door machine control circuit	RH900
9E	PC output circuit(Geared)	Double door	22D	Door machine control circuit	FERMATOR
10	Inspection circuit / MRL Overspeed governor control circuit	Cartop inspection signal by CANbus	22E	Door machine control circuit	JARLESS-CON
			22F	Door machine control circuit	RH200
			23	Installation and wiring diagram of leveling switches	
11	Lighting circuit		24	Shaft switches installation diagram	
12	Emergency power circuit		25, 25A, 25B, 25C, 25D	UCMP or open the door early diagram	
13	Car communication circuit				

SRH		Sicher Elevator CO., LTD			
GR30023AA-YL01-FB(EN)		Drawing Catalog			
Design	XinfengLuo	Check	JianxueShen	Page	1
Standardize	GuopingZhou	Approve	XiaoyingRu	Date	25/09/2021

1

2

3

4

1

2

3

4

D

C

B

A

Components Code Instruction

No.	Codes	Items	Location	No.	Codes	Items	Location
1	ARD	elevator emergency leveling device	Machine room	31	PTD/1PTD	Door motor inverter	Car top
2	EM	Light lamp of car	Car	32	PCJX	Car top control board	Car top
3	EK	Light lamp of control cabinet	Control cabinet	33	PCQK	Group control board	Control cabinet
4	EA	Light lamp of car top	Car top	34	PCZLZ	Car command board	Main operation box
5	EGS	Wire rope lamp of MRL lift	Shaft	35	PCXSZ	Display board	Main operation box
6	EJ1-EJn	Light lamps of shaft	Shaft	36	PCXSF	Display board	Auxiliary operation box
7	EYJ	Emergency light lamp	Car	37	PCZLF	Car command board	Auxiliary operation box
8	EKM/EGM	Door open button lamp/Door close button lamp	Car	38	PCWH	landing display board	Landing
9	EYGM	Door open holding button lamp	Car	39	PCZLC	Car command board	Disability operation box
10	E1J-E32J	Car command button lamps	Car	40	Q0	Power-on circuit breaker	Control cabinet
11	EBJ	Intercom button of car	Car	41	Q1~2	Circuit breaker	Control cabinet
12	E1S-En-1S	1~n-1 Floor call up lamp	Landing	42	QFW	Overspeed governor reset coil	Shaft
13	E2X-EnX	2~n Floor call down lamp	Landing	43	QDZ	Overspeed governor action coil	Shaft
14	EDS1-EDSn-1	1~n-1 Floor up arrival lamp	Landing	44	RZ2	Over-voltage absorption resistance	Traction machine
15	EDX2-EDXn	2~n Floor down arrival lamp	Landing	45	RZD	Brake resistor	Machine room
16	F1~3	Circuit breaker	Control cabinet	46	STK1-3	Emergency stop switch of pit	Pit
17	FB1~2	Circuit breaker	Control cabinet	47	SPL	Stop switch of MRL	Traction machine
18	FS	Car fan	Car top	48	STJ	Emergency stop switch of control cabinet	Control cabinet
19	KKC	Motor operating control contactor	Control cabinet	49	SMJ	Car door lock	Car top
20	KFX	Star sealing control relay	Control cabinet	50	SMT1-SMTn	Landing door lock	Shaft
21	KB	Brake contactor	Control cabinet	51	SMJH	Car rear door lock	Car top
22	KGDY	Switching supply	Control cabinet	52	SWS/SWX	Up slow-down switch 1 / Down slow-down switch 1	Shaft
23	K12	Plugins for testing(UCMP)	Control cabinet	53	SW2S/SW2X	Up slow-down switch 2 / Down slow-down switch 2	Shaft
24	MCZ	Overload device	Car bottom	54	SZD1~2	Brake limit switch	Traction machine
25	M	Traction machine	Machine room	55	SXD	Mechanical action&reset button of overspeed governor	Control cabinet
26	MD,MD1	Door motor	Car top	56	SEM	Illumination lamp switch of car	Car
27	PT	Drive	Control cabinet	57	SYJ	Emergency rescue monitoring switch of MRL	Control cabinet
28	PG	Encoder	Traction machine	58	SOS	Action on traction Wire holder switch	Machine room
29	PC	Microprocessor based lift control	Control cabinet	59	SGJ	emergency electrical operation switch of machine room	Control cabinet
30	PTC	Motor overheat protection switch	Traction machine	60	SEK	Illumination lamp switch of control cabinet	Control cabinet

D

C

B

A

SRH

Sicher Elevator CO., LTD

GR30023AA-YL01-FB(EN) Components code list					
Design	XinfengLuo	Check	JianxueShen	Page	3
Standardize	GuopingZhou	Approve	XiaoyingRu	Date	25/09/2021

1

2

3

4

1

2

3

4

Components Code Instruction

No.	Codes	Items	Location	No.	Codes	Items	Location
61	SFS	Fan switch of car	Car	91	SXF	Fire switch	Landing
62	SMQS, SMQX	door zone switch	Car top	92	SMTH1-SMTHn	Rear landing door lock	Shaft
63	SEA	Illumination lamp switch of car top	Car top	93	SXF1	Fire linkage control switch	Machine room
64	STD	Emergency stop switch of car top	Car top	94	SXFY	Fireman switch	Operation box
65	SAJ	Safety inspection pin switch	Car top	95	SEGS	Wire rope lighting switch	Control cabinet
66	SGS/SGX	Upwards pushbutton/Downwards pushbutton of machine room	Control cabinet	96	SJZF	Shaft lighting linkage control switch	Control cabinet
67	SJT	Emergency stop switch of car	Car	97	SJZK	Shaft lighting linkage control switch	Pit
68	SAQ	Safety gear switch	Car bottom	98	TC1	Transformer	Control cabinet
69	SXZ1	Overspeed governor switch	Shaft	99	TEL1	Intercom of control cabinet	Machine room
70	SSX, SXX	Up final limit switch/Down final limit switch	Shaft	100	TEL2	Intercom of duty office	Duty office
71	SC1-3	Buffer switch	Pit	101	TEL3/HJ/DZL	Intercom of car top/Alarm bell/Arrival gong	Car top
72	SXS	Overspeed governor rope breaking switch	Pit	102	TEL4	Intercom of car	Car
73	SQRG	Run pushbutton of machine room	Control cabinet	103	TEL5	Intercom of pit	Pit
74	SQRD	Run pushbutton of car top	Car top	104	VZ	Brake unit	Control cabinet
75	SDS/SDX	Upwards pushbutton/Downwards pushbutton of car top	Car top	105	VD	Over-voltage absorption diode	Traction machine
76	SK, 1SK	Open limit switch of front door and rear door	Car top	106	XM XM1	AC220V Power supply socket at machine room	Machine room
77	SG, 1SG	Close limit switch of front door and rear door	Car top	107	XA XA1	AC220V Power supply socket at car top	Car top
78	SAP, 1SAP	Light-beam curtain power switch of front door and rear door	Car top	108	XD XD1	AC220V Power supply socket at pit	Pit
79	SCZ/SMZ	Overload switch / Fullload switch	Car bottom	109	YJDY	Emergency power	Car top
80	SDJ	Inspection switch of car top	Car top	110	YYBZ	Voice announcement	Car top
81	SKM/SGM	Door open button / Door close button	Car	111	YJSZ	Emergency electric brake release device	Control cabinet
82	SYGM	Door open holding button	Car	112	ZCQ	Brake coil	Traction machine
83	SJHX	Direction change switch	Car	113	PL	bypass (PL-J, PL-T, PL-Z)	
84	SDL	Independent running switch	Car	114	PCTQ	UCMP or open the door early	
85	SZS	Direct travel ride button	Car	115	SPS, SPX	Leveling switches	
86	SJS	Attendant switch	Car	116			
87	S1J-SnJ	Car command button of car	Car	117			
88	S1S-Sn-1S	1~n-1 Floor call up button	Landing	118			
89	S2X-SnX	2~n Floor call down button	Landing	119			
90	SDY	Elevator lock switch	Landing	120			

SRH

Sicher Elevator CO., LTD

GR30023AA-YL01-FB(EN)		Components code list			
Design	XinfengLuo	Check	JianxueShen	Page	3A
Standardize	GuopingZhou	Approve	XiaoyingRu	Date	25/09/2021

1

2

3

4

D

C

B


A

D

C

B

A

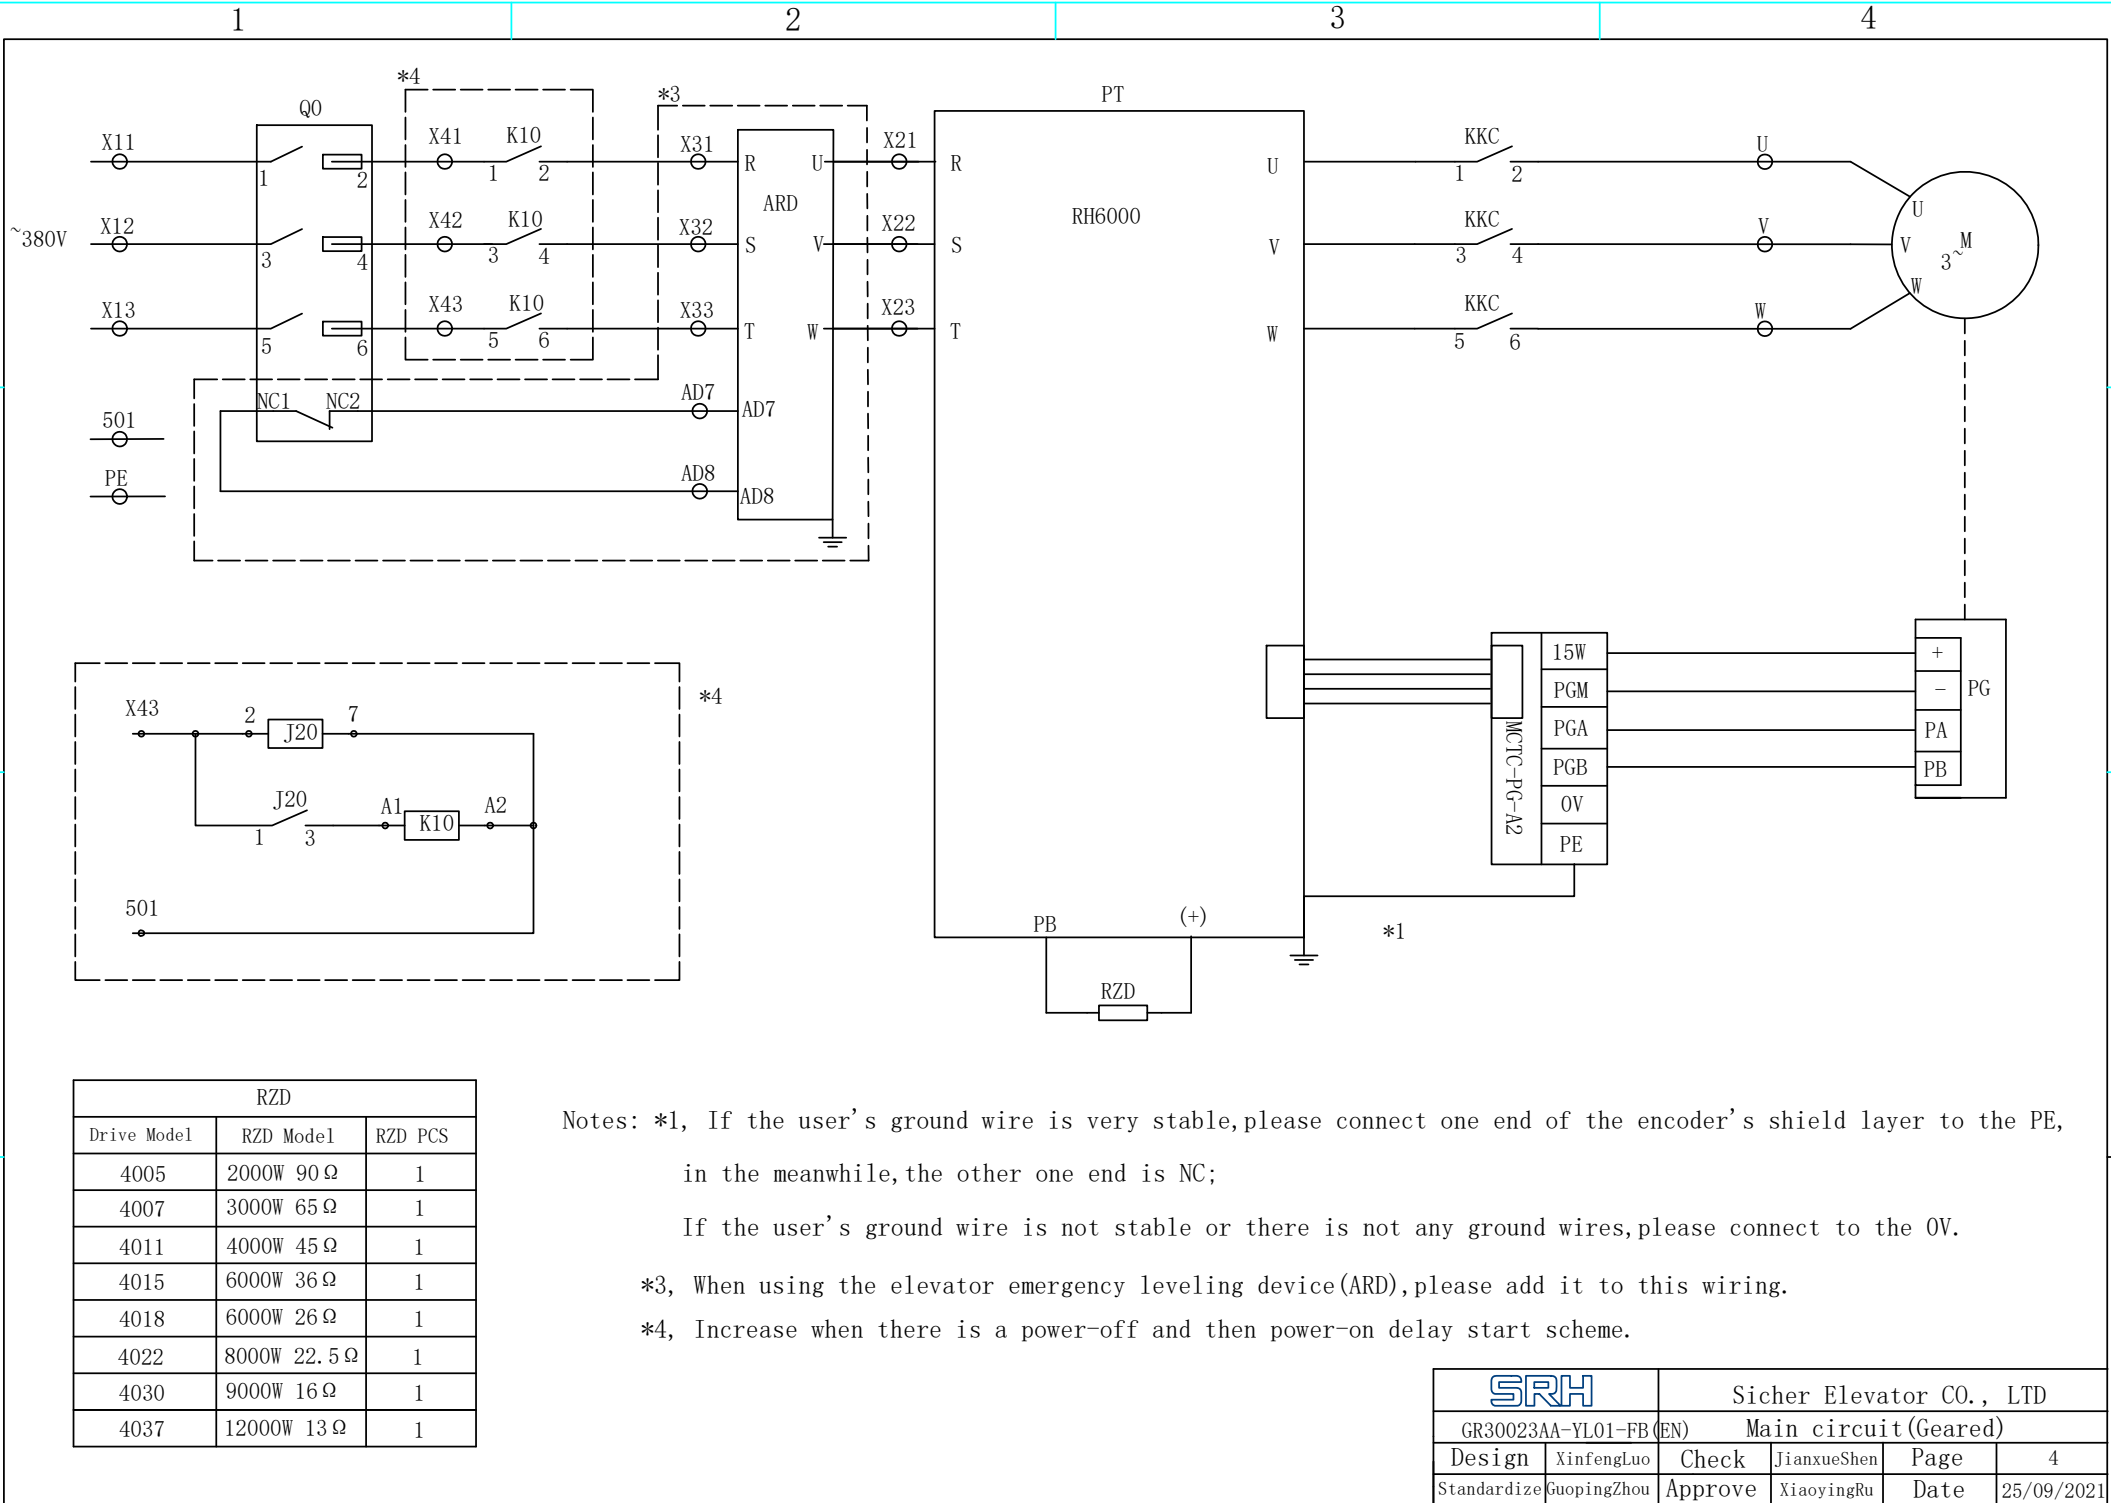

RZD		
Drive Model	RZD Model	RZD PCS
4005	2000W 90 Ω	1
4007	3000W 65 Ω	1
4011	4000W 45 Ω	1
4015	6000W 36 Ω	1
4018	6000W 26 Ω	1
4022	8000W 22.5 Ω	1
4030	9000W 16 Ω	1
4037	12000W 13 Ω	1

SRH		Sicher Elevator CO., LTD			
GR30023AA-YL01-FB (EN)		Main circuit (Geared)			
Design	XinfengLuo	Check	JianxueShen	Page	4
Standardize	GuopingZhou	Approve	XiaoyingRu	Date	25/09/2021

D

C

B


A

D

C

B

A

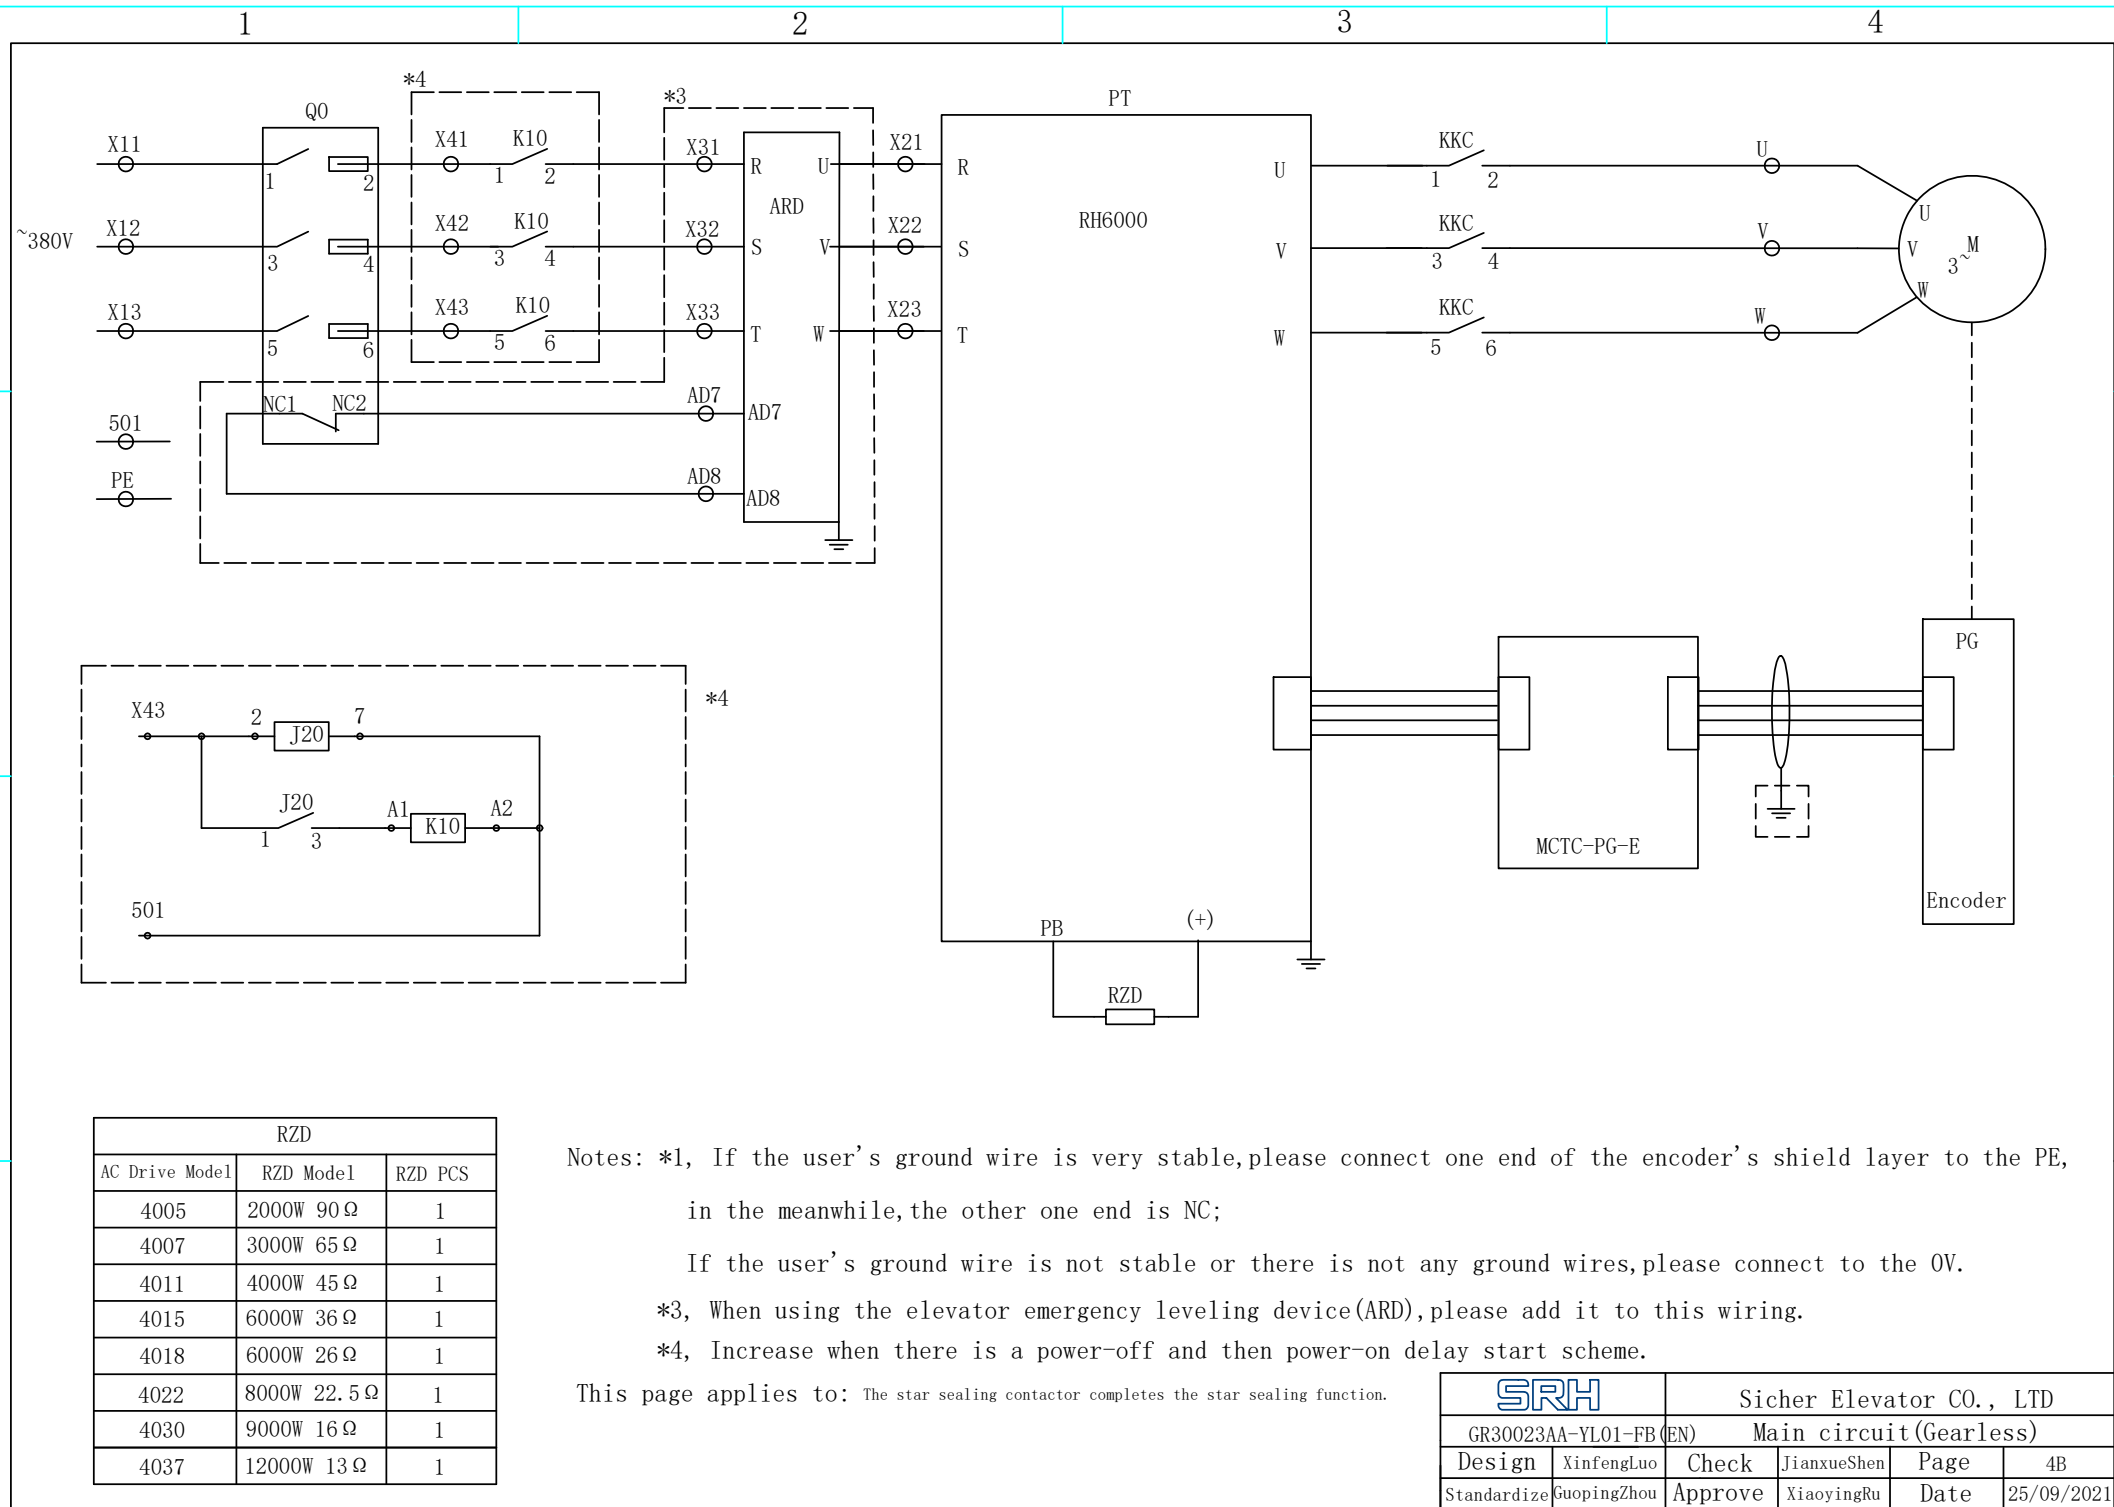

D

C

B


A

D


C

B

A

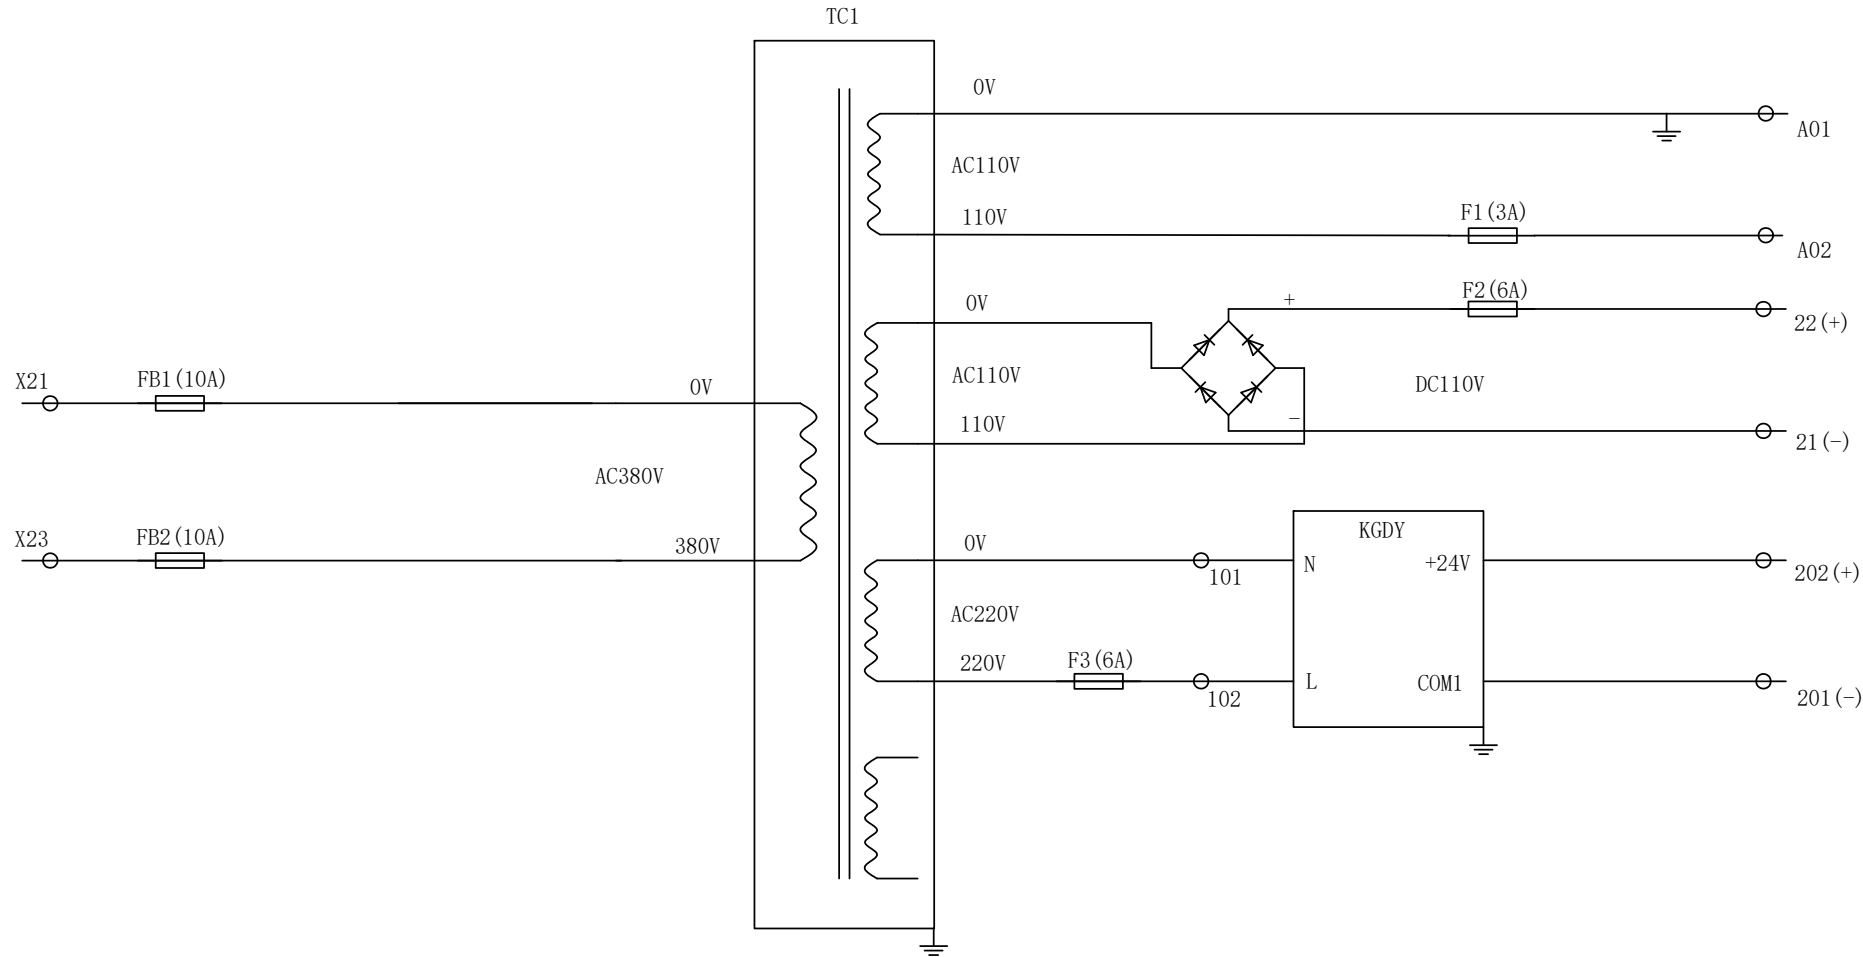

SRH		Sicher Elevator CO., LTD			
GR30023AA-YL01-FB(EN)		Control power supply circuit			
Design	XinfengLuo	Check	JianxueShen	Page	5
Standardize	GuopingZhou	Approve	XiaoyingRu	Date	25/09/2021

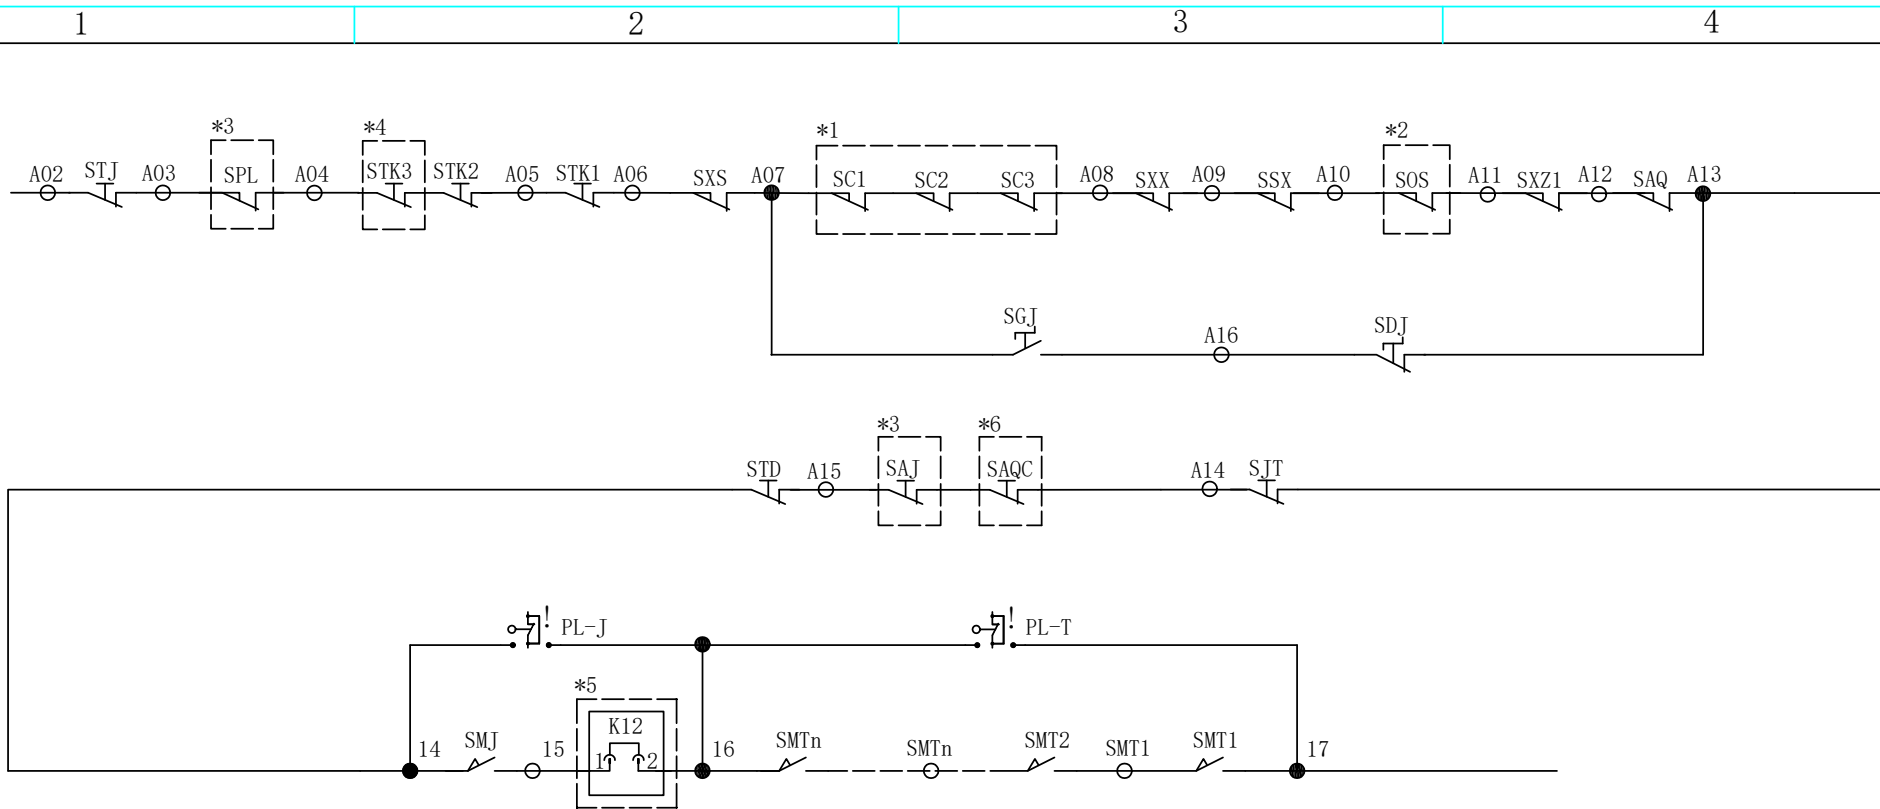

Notes: * 1, Please short A07 to A08 when using non-hydraulic buffer.

* 2, Please short A10 to A11 when using gearless traction machine.

* 3, Please add safety inspection pin switch(SAJ) and MRL stop switch(SPL) when MRL.

Please add hand wheel switch(SPL) when MR.

SPL: It is MRL stop switch when MRL;


It is hand wheel switch when MR.

* 4, Please add pit stop switch(STK3) when the 1st floor is Through door.


* 5, K12 is the UCMP testing plugin.if there is no UCMP function,please short 15 to 16.

This page applies to:Single door.

* 6, Increase when there is a safety window switch.

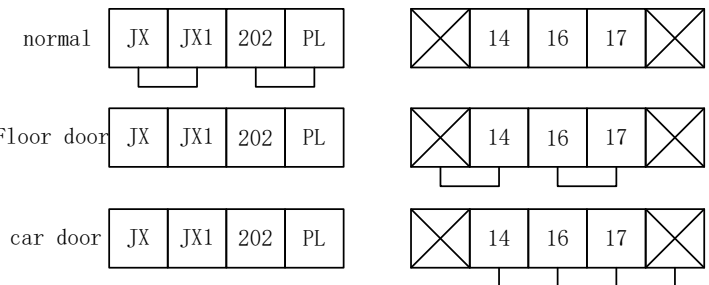

SRH		Sicher Elevator CO., LTD			
GR30023AA-YL01-FB(EN)		Safety door lock circuit			
Design	XinfengLuo	Check	JianxueShen	Page	6
Standardize	GuopingZhou	Approve	XiaoyingRu	Date	25/09/2021

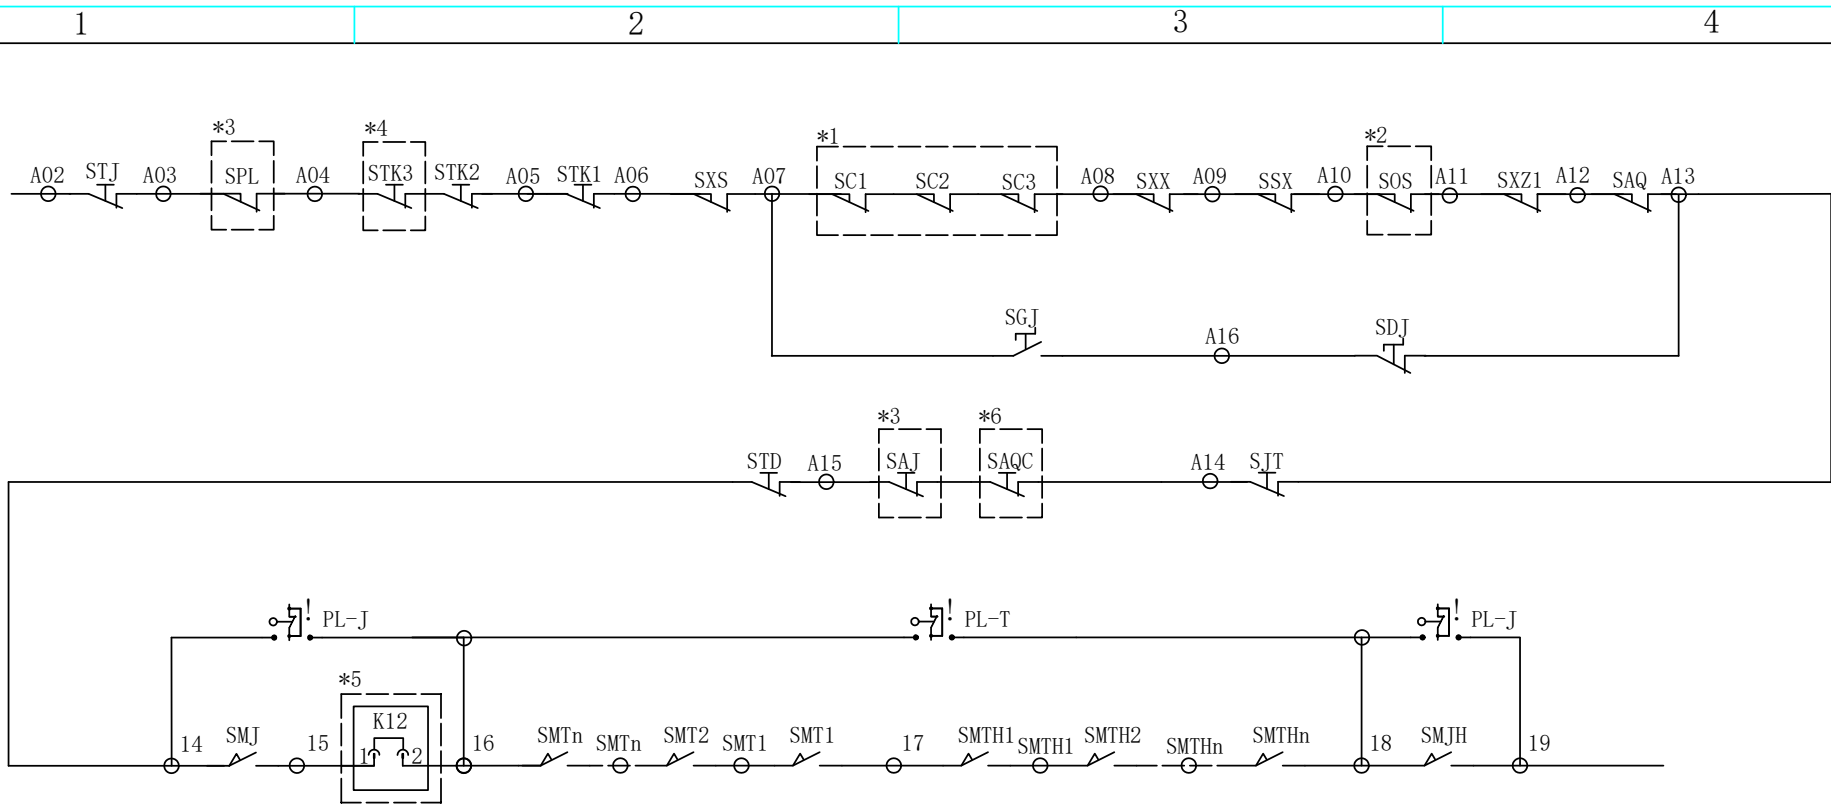

Notes: * 1, Please short A07 to A08 when using non-hydraulic buffer.

* 2, Please short A10 to A11 when using gearless traction machine.

* 3, Please add safety inspection pin switch(SAJ) and MRL stop switch(SPL) when MRL.
Please add hand wheel switch(SPL) when MR.


SPL: It is MRL stop switch when MRL;
It is hand wheel switch when MR.

* 4, Please add pit stop switch(STK3) when the 1st floor is Through door.

* 5, K12 is the UCMF testing plugin.if there is no UCMF function,please short 15 to 16.

This page applies to:Double door.


* 6, Increase when there is a safety window switch.

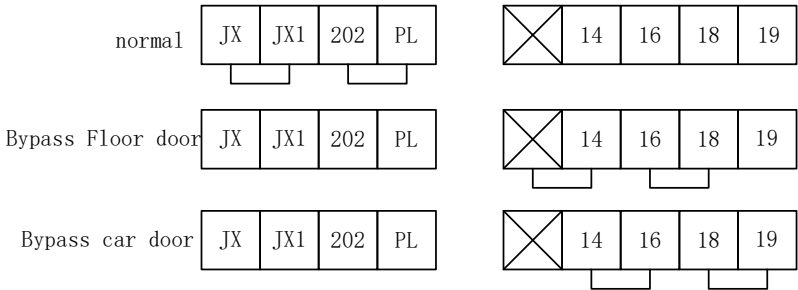

SRH		Sicher Elevator CO., LTD			
GR30023AA-YL01-FB(EN)		Safety door lock circuit			
Design	XinfengLuo	Check	JianxueShen	Page	6A
Standardize	GuopingZhou	Approve	XiaoyingRu	Date	25/09/2021

D

D

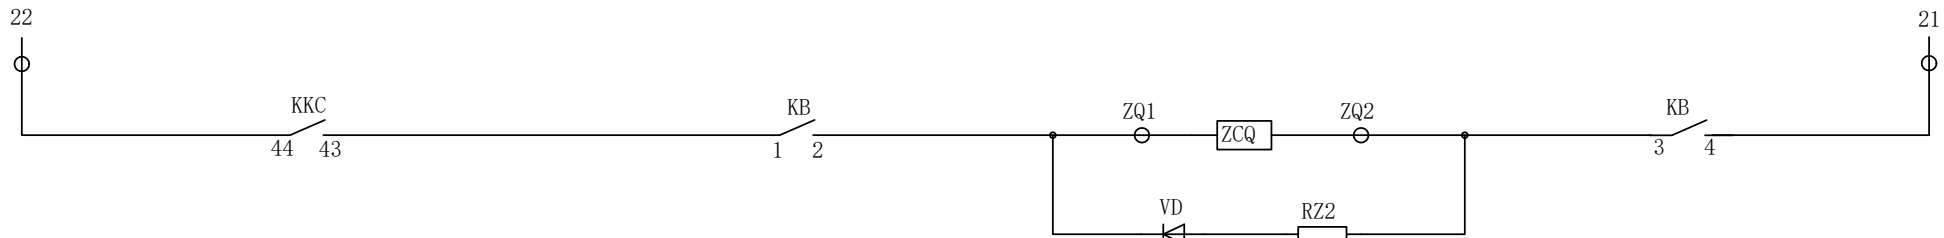


Brake circuit

C


C

B

B

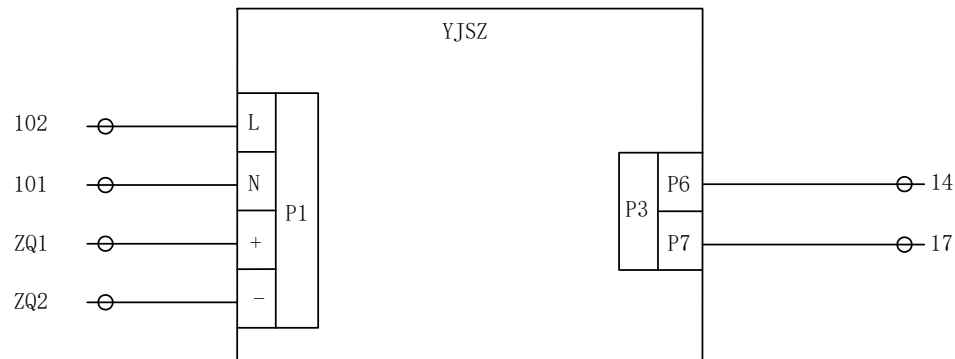

Emergency brake release device circuit(single door)


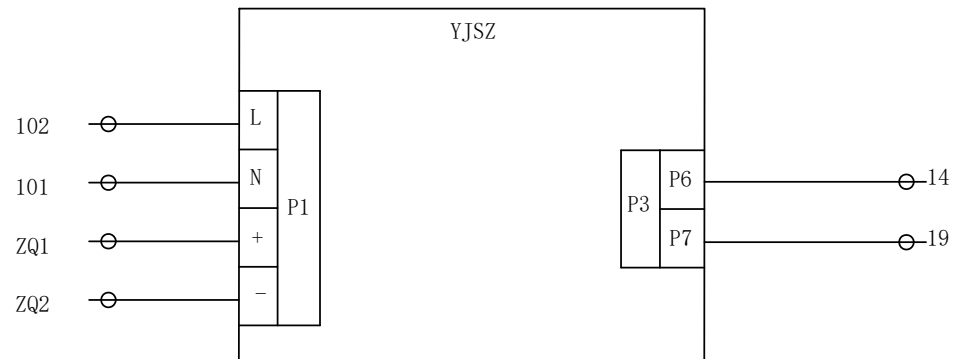


Emergency brake release device circuit(Double door)

A

A

SRH		Sicher Elevator CO., LTD			
GR30023AA-YL01-FB(BN)		Brake Circuit/Emergency brake release device circuit			
Design	XinfengLuo	Check	JianxueShen	Page	7
Standardize	GuopingZhou	Approve	XiaoyingRu	Date	25/09/2021

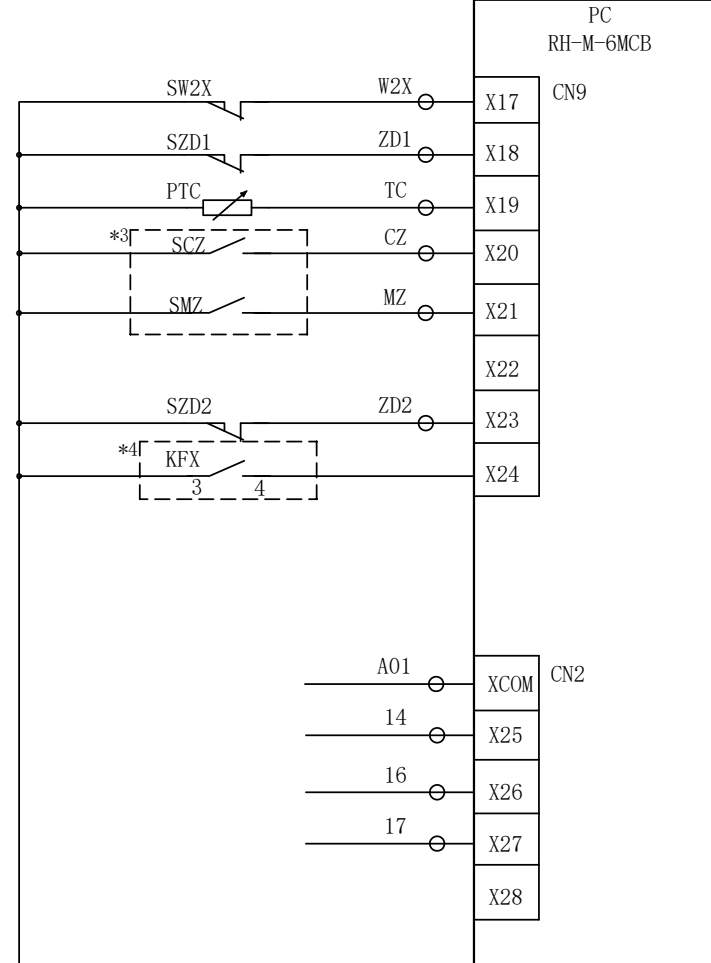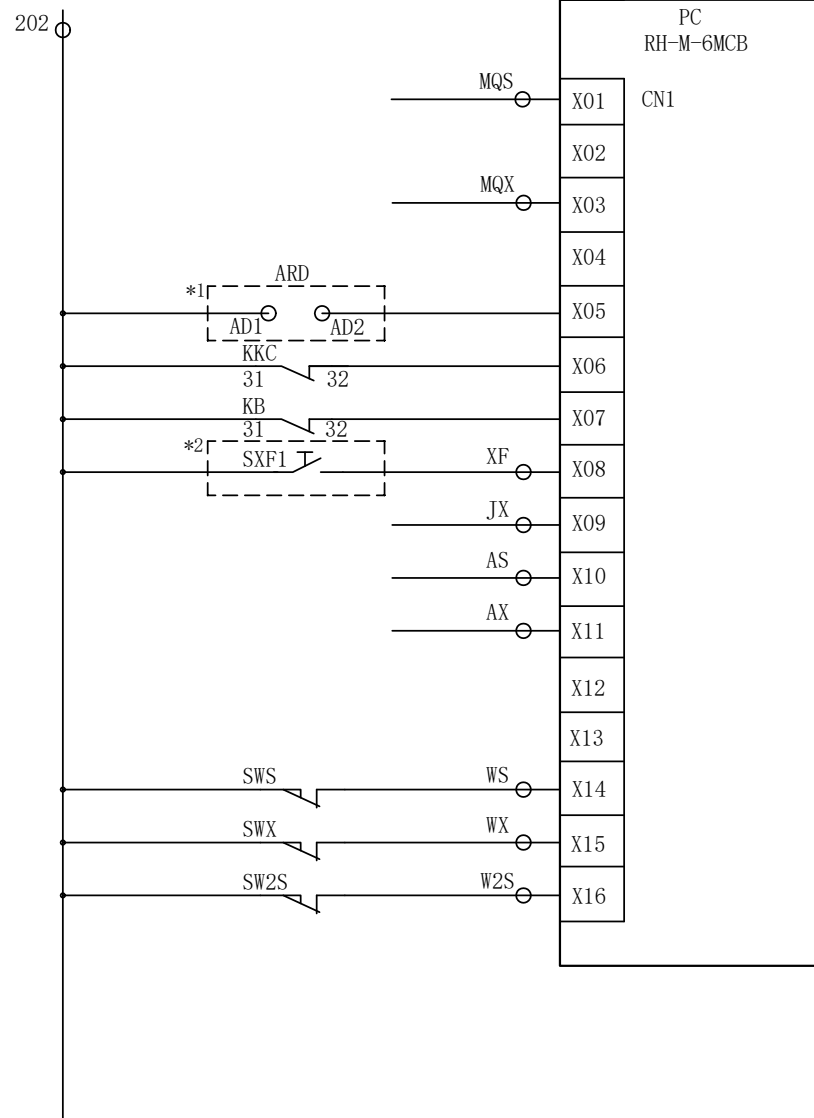

- Notes: *1, When using the elevator emergency leveling device(ARD),please add it to this wiring.
- *2, When using the fire linkage control,please add it to this writing.
- *3, When the weigh device on the rope head plate,please add it to this writing.
- *4, When the control relay completes the star sealing function,please add it to this writing.

SRH		Sicher Elevator CO., LTD			
GR30023AA-YL01-FB(EN)PC input circuit(Single door)					
Design	XinfengLuo	Check	JianxueShen	Page	8
Standardize	GuopingZhou	Approve	XiaoyingRu	Date	25/09/2021

D

C

B



A

D

C

B

A

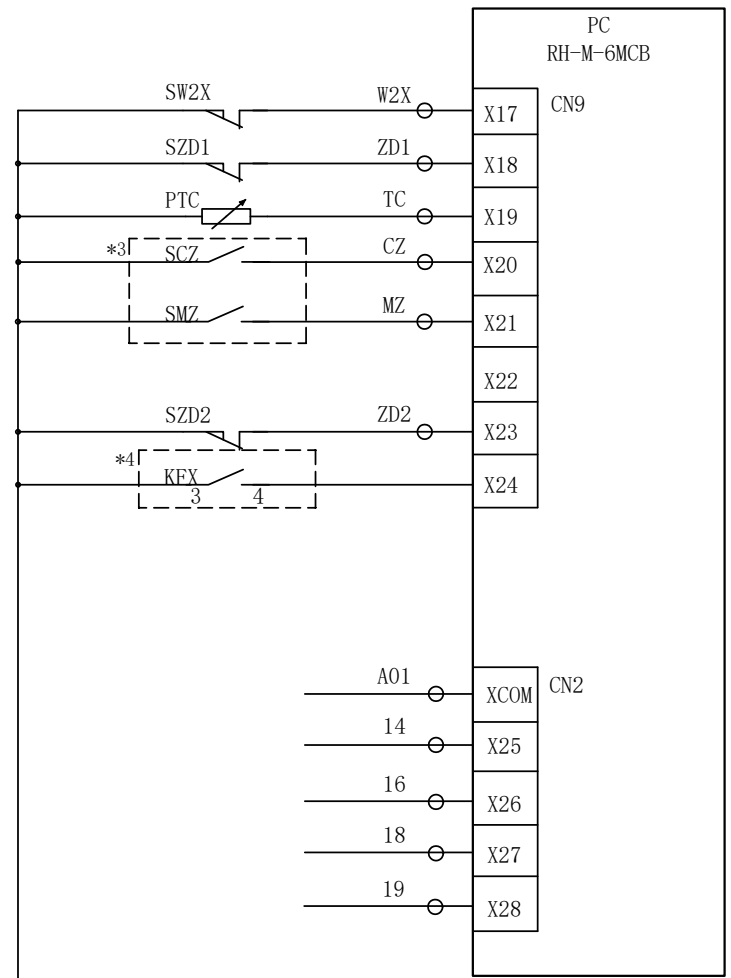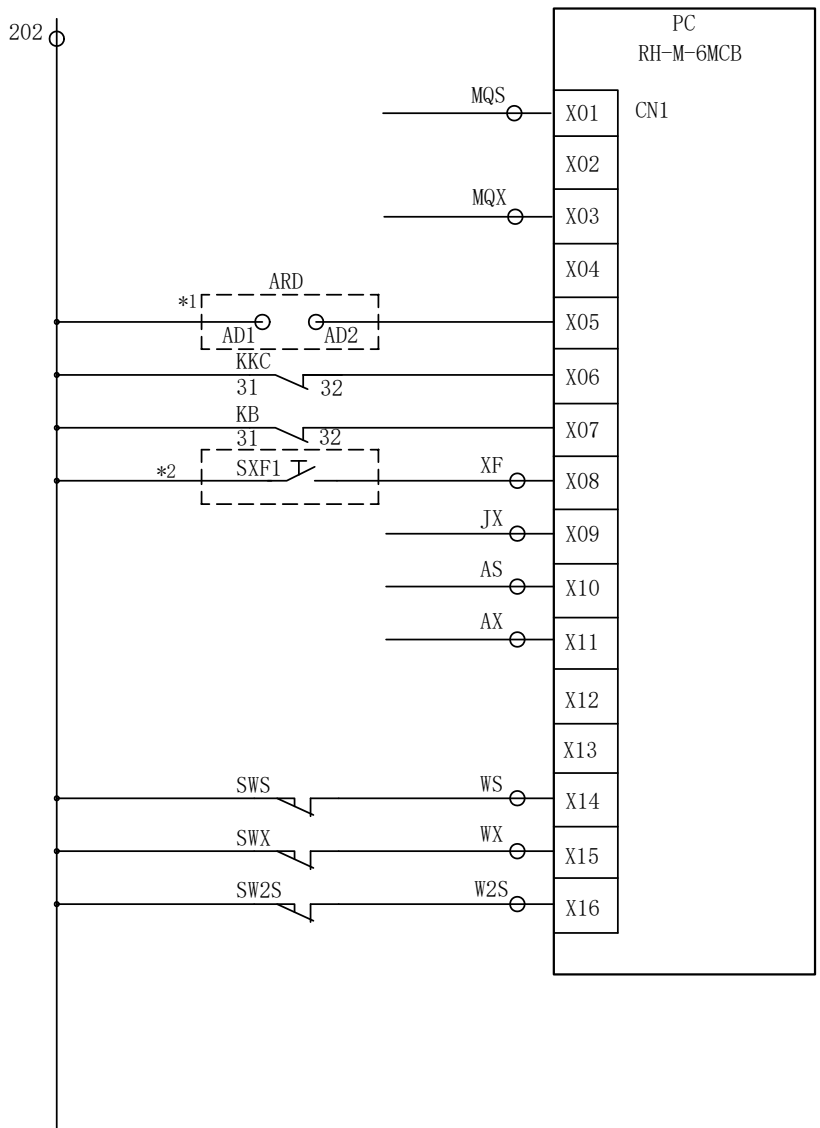

Notes: *1, When using the elevator emergency leveling device(ARD),please add it to this wiring.
*2, When using the fire linkage control,please add it to this writing.
*3, When the weigh device on the rope head plate,please add it to this writing.
*4, When the control relay completes the star sealing function,please add it to this writing.

SRH		Sicher Elevator CO., LTD			
GR30023AA-YL01-FB(EN)		PC input circuit(Double door)			
Design	XinfengLuo	Check	JianxueShen	Page	8A
Standardize	GuopingZhou	Approve	XiaoyingRu	Date	25/09/2021

D

C

B



A

D

C

B

A

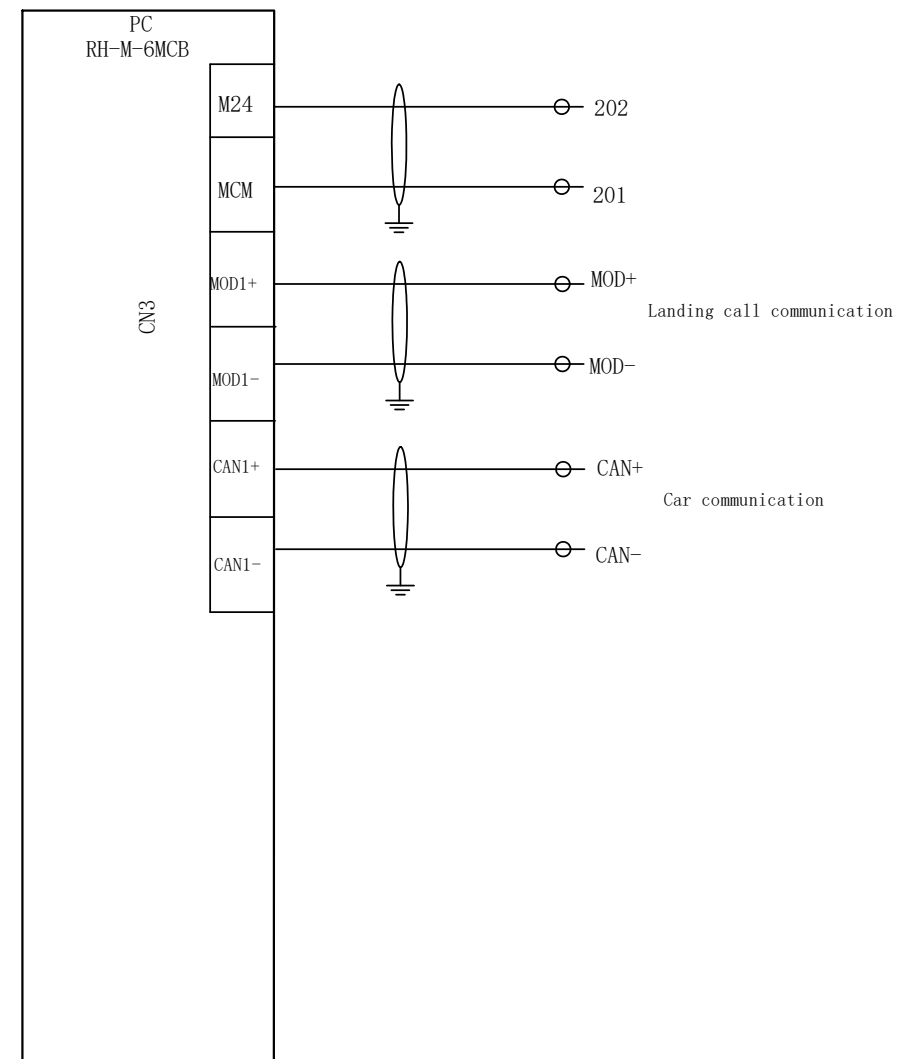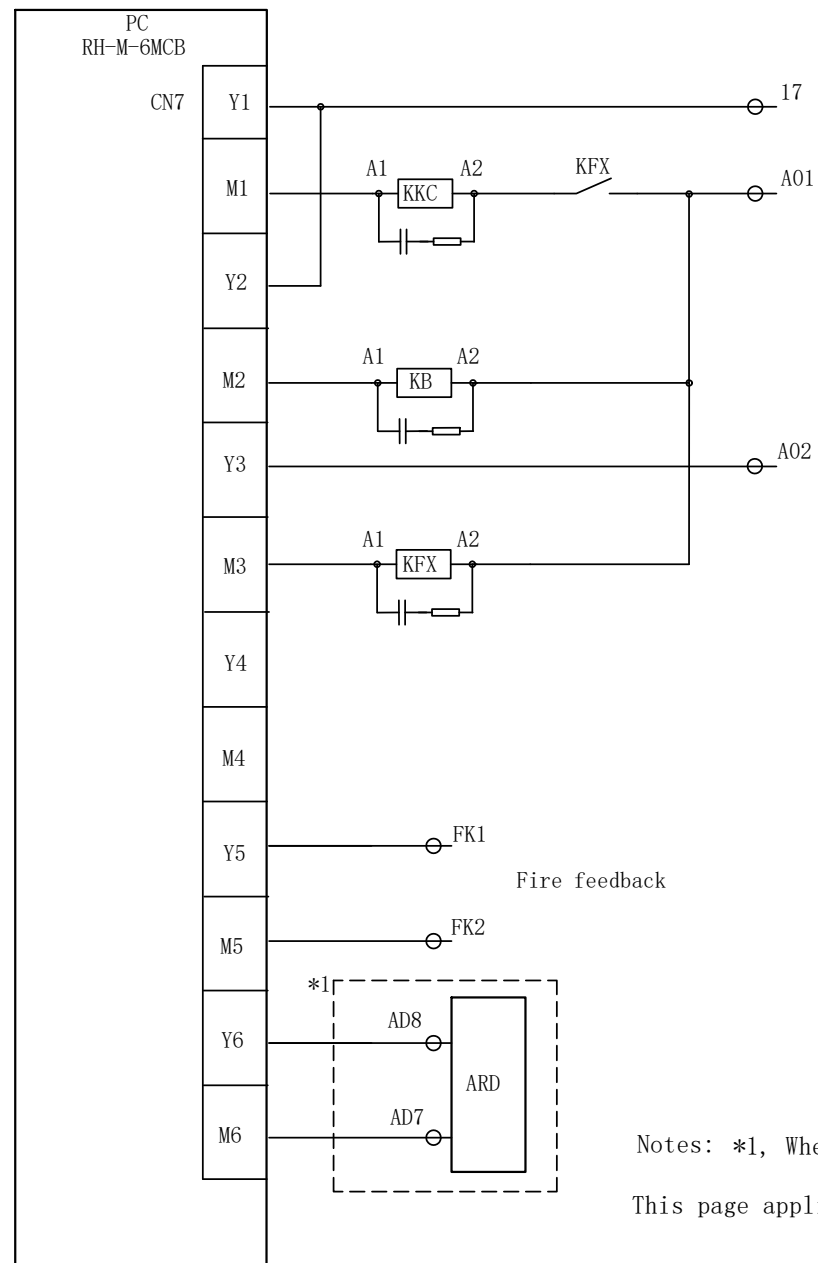

Notes: *1, When using the elevator emergency leveling device (ARD), please add it to this wiring.

This page applies to: The control relay completes the star sealing function.

SRH		Sicher Elevator CO., LTD			
GR30023AA-YL01-FB(EN) PC output circuit(Gearless,Single door)					
Design	XinfengLuo	Check	JianxueShen	Page	9
Standardize	GuopingZhou	Approve	XiaoyingRu	Date	25/09/2021

D

C

B



A

D

C

B



A

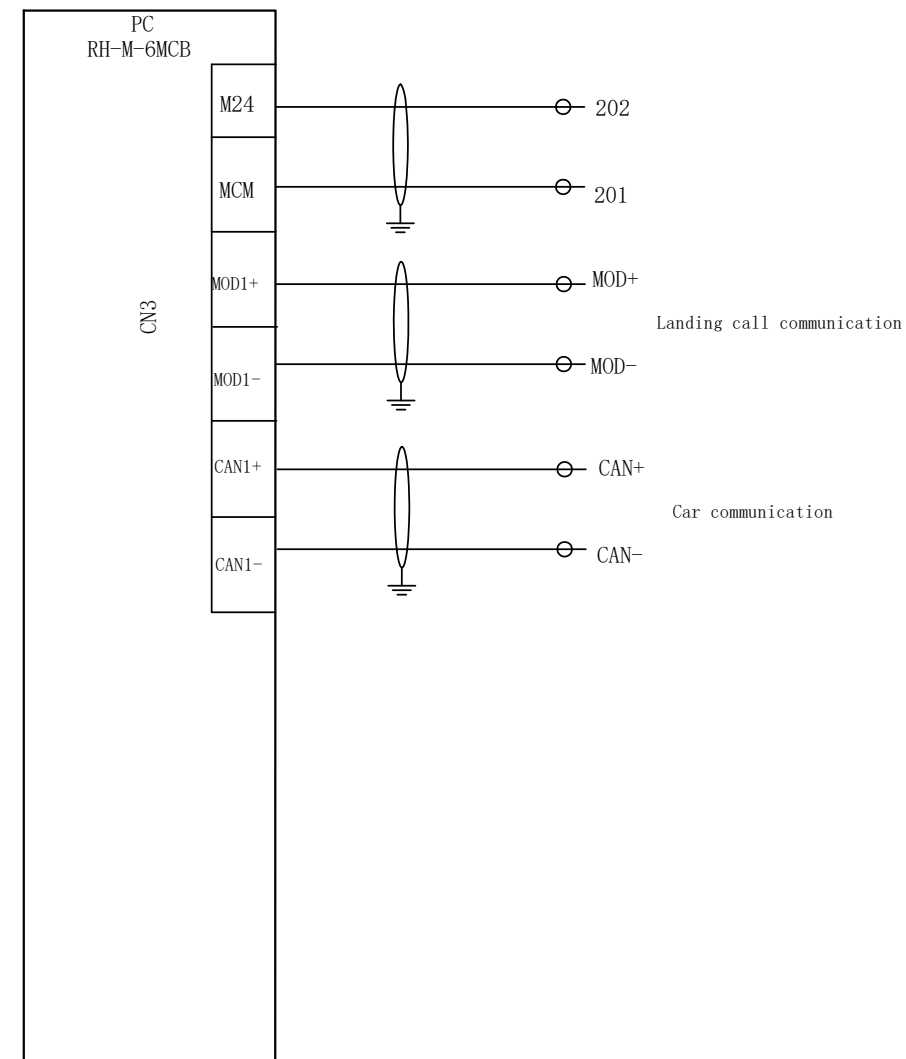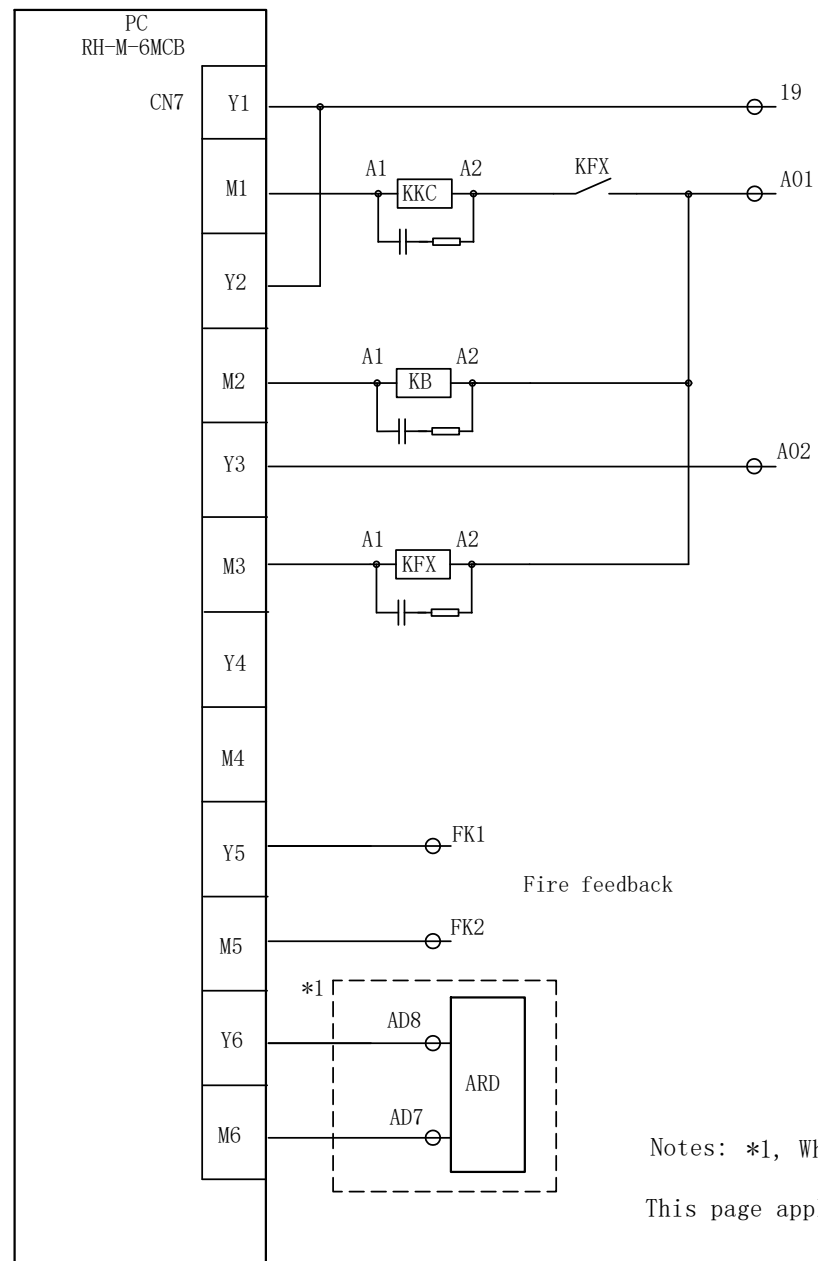

Notes: *1, When using the elevator emergency leveling device(ARD),please add it to this wiring.

This page applies to: The control relay completes the star sealing function.

		Sicher Elevator CO., LTD			
GR30023AA-YL01-FB(EN) PC output circuit(Gearless,Double door)					
Design	XinfengLuo	Check	JianxueShen	Page	9A
Standardize	GuopingZhou	Approve	XiaoyingRu	Date	25/09/2021

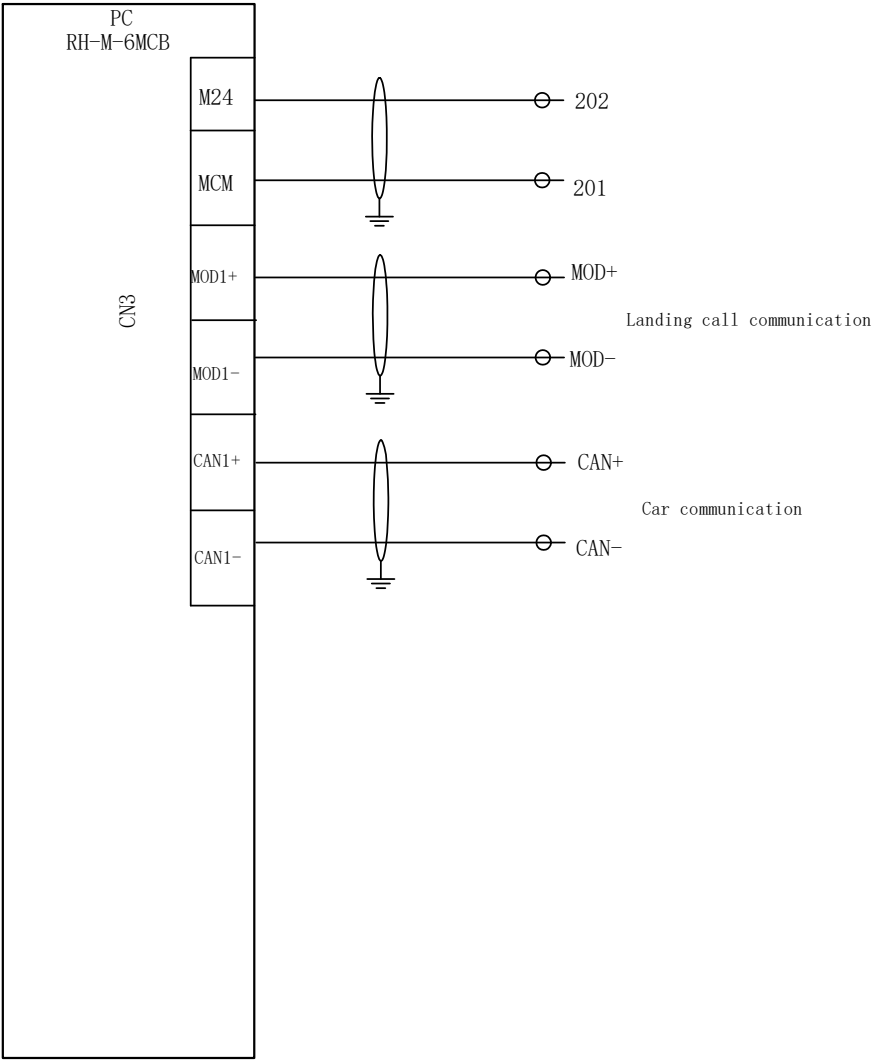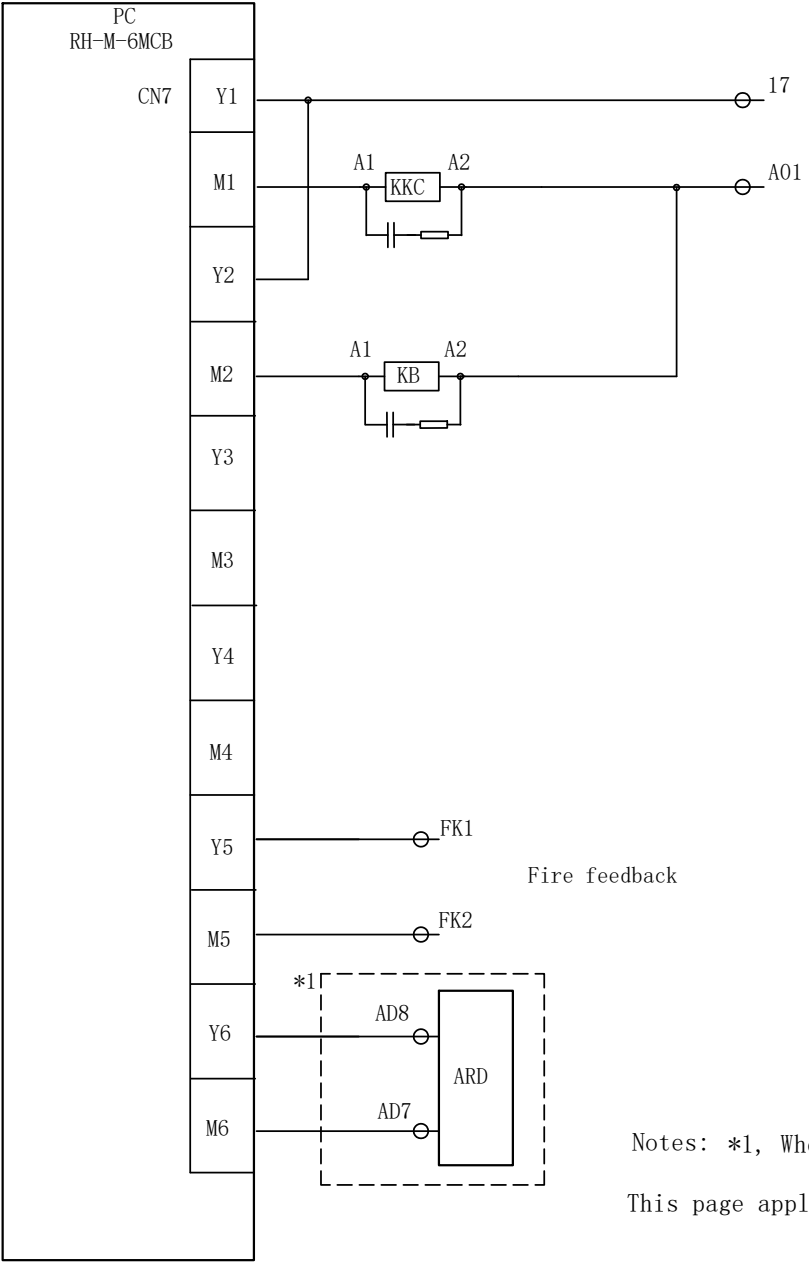

Notes: *1, When using the elevator emergency leveling device(ARD),please add it to this wiring.
This page applies to: The star sealing contactor completes the star sealing function.

D

C

B



A

D

C

B

A

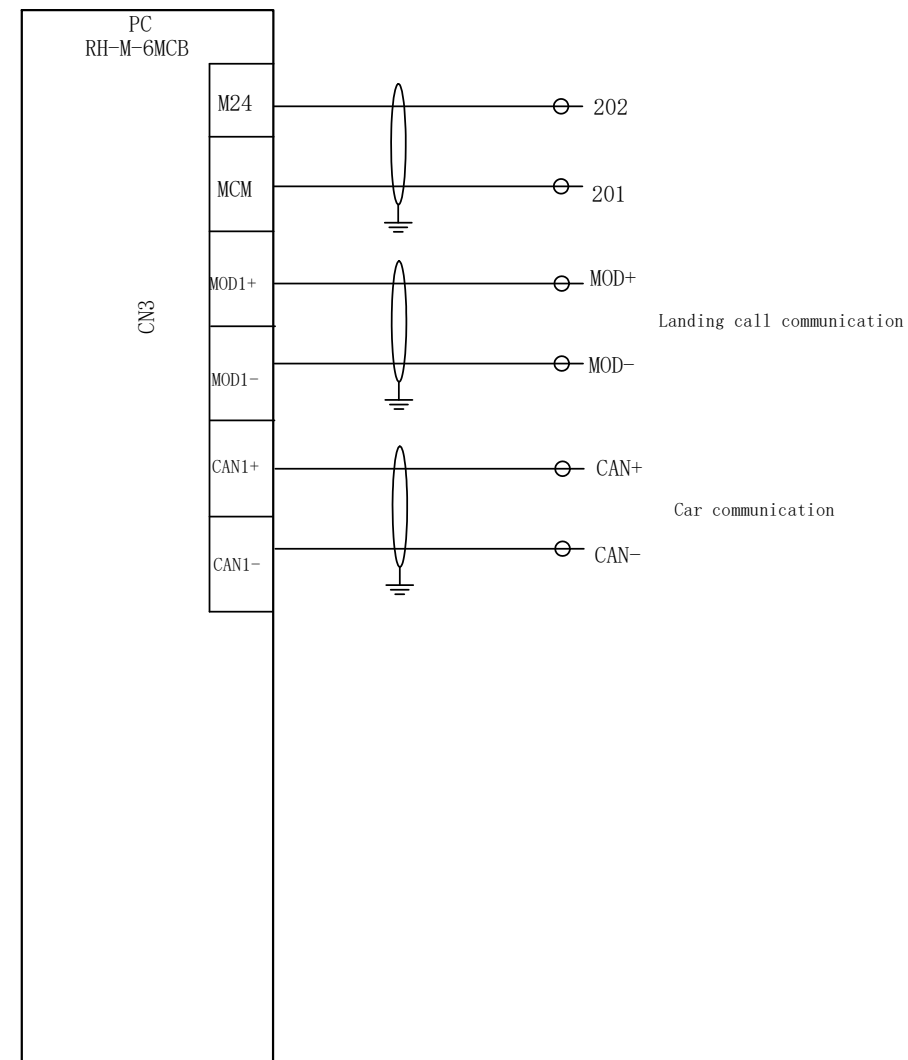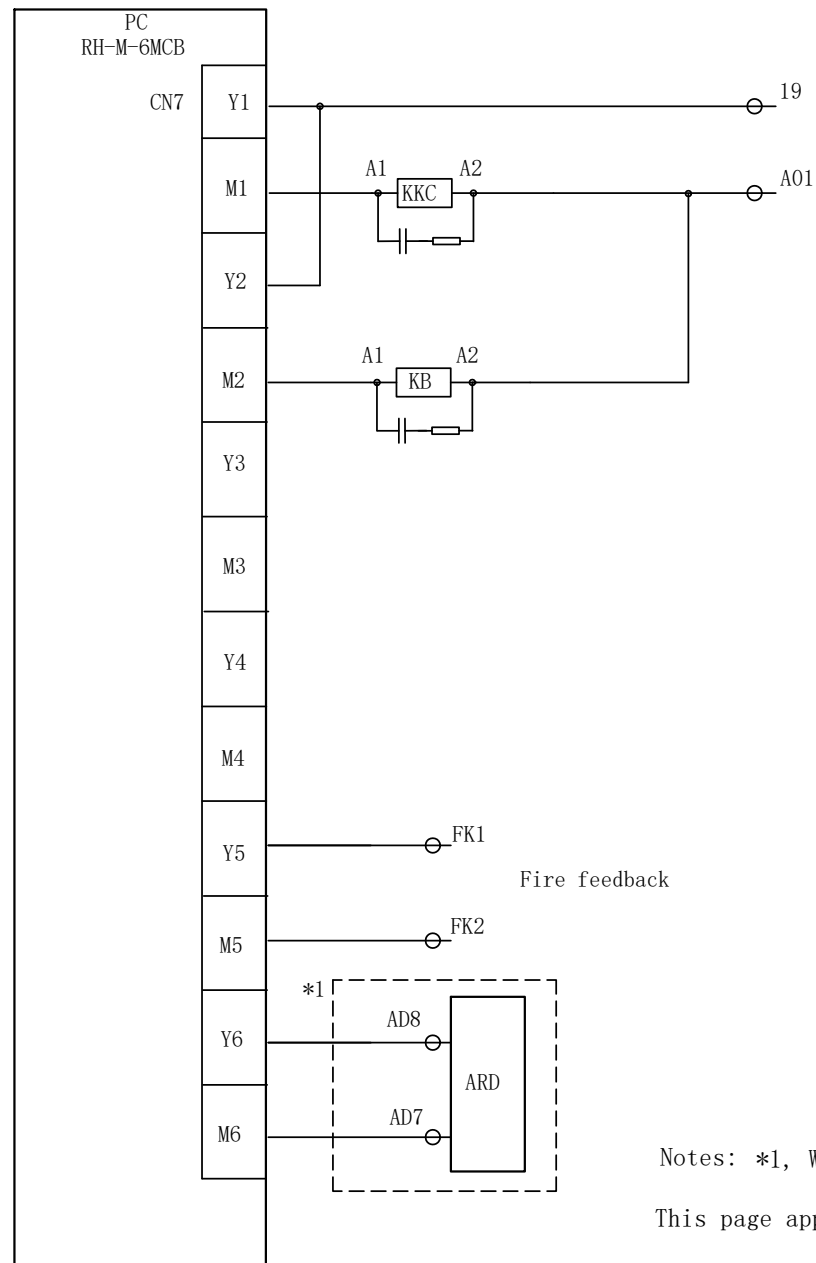

Notes: *1, When using the elevator emergency leveling device(ARD),please add it to this wiring.

This page applies to: The star sealing contactor completes the star sealing function.

SRH		Sicher Elevator CO., LTD			
GR30023AA-YL01-FB(EN)		PC output circuit(Gearless,Double door)			
Design	XinfengLuo	Check	JianxueShen	Page	9C
Standardize	GuopingZhou	Approve	XiaoyingRu	Date	25/09/2021

D

C

B



A

D

C


B

A

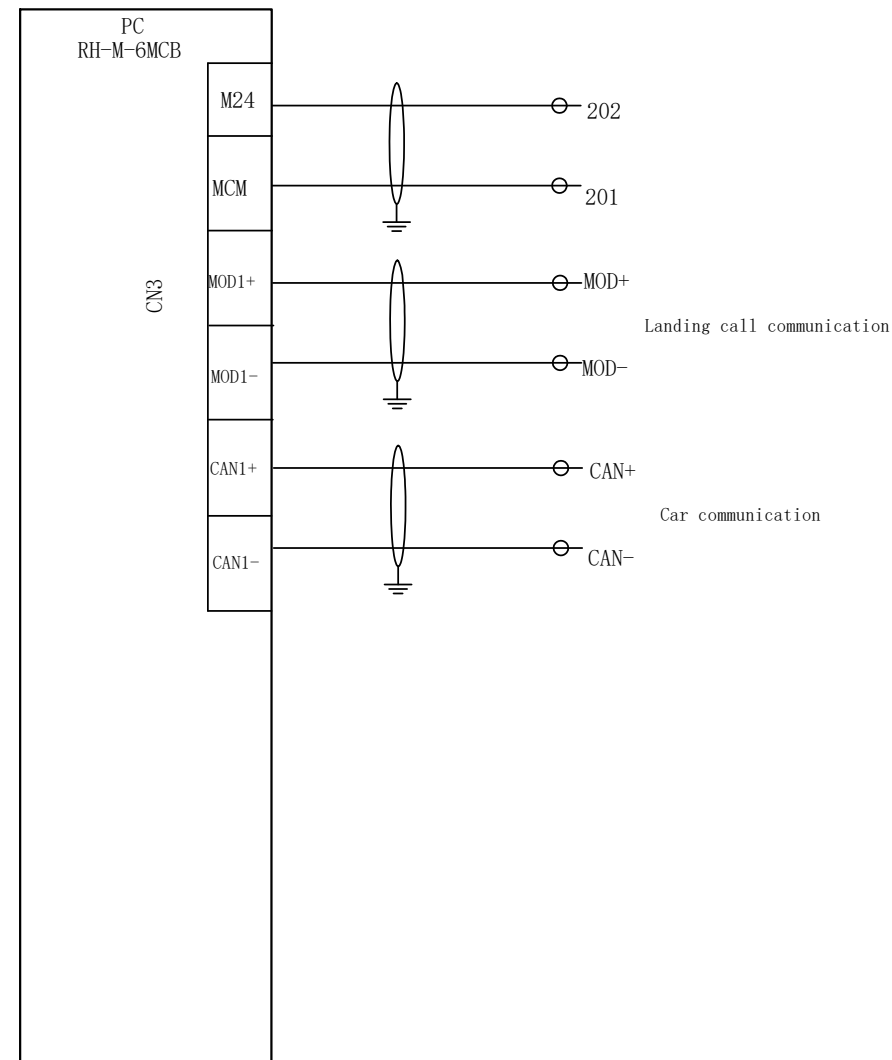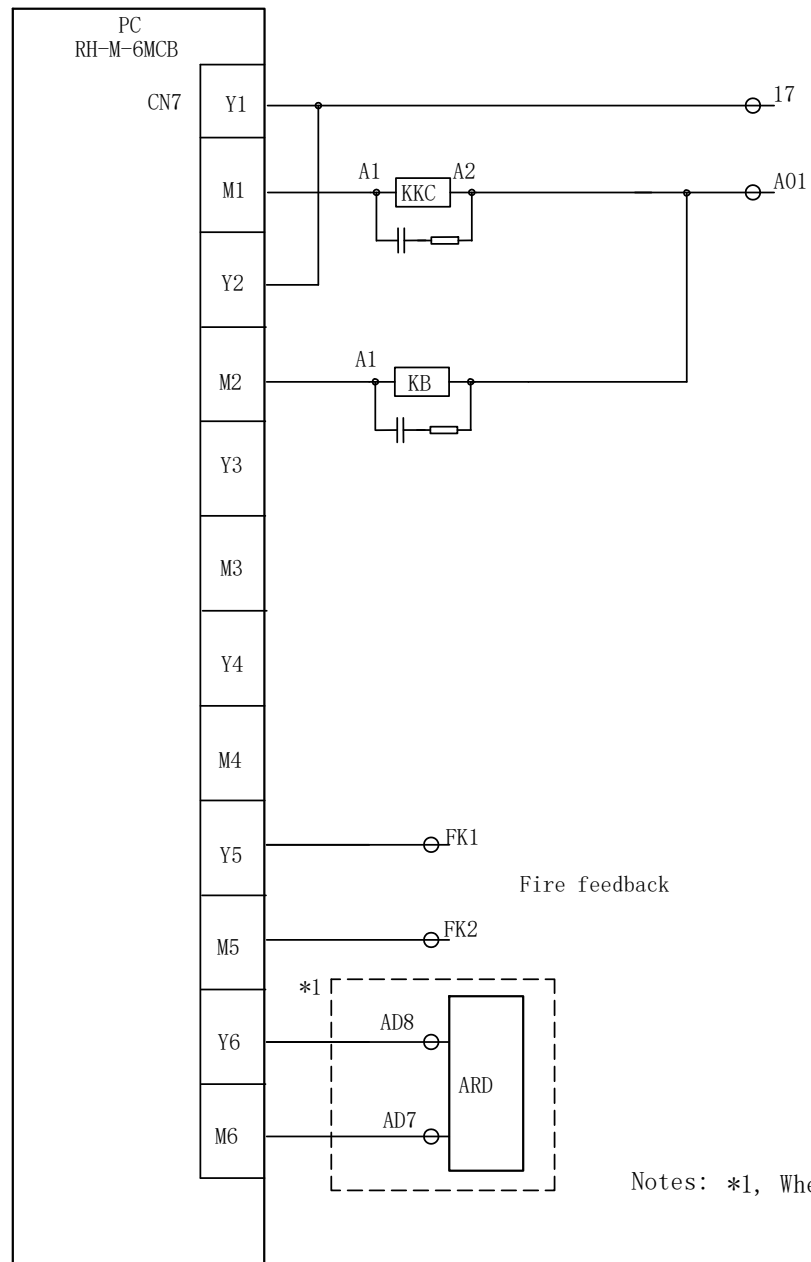

Notes: *1, When using the elevator emergency leveling device(ARD),please add it to this wiring.

SRH		Sicher Elevator CO., LTD			
GR30023AA-YL01-FB(EN)		PC output circuit(Geared,Single door)			
Design	XinfengLuo	Check	JianxueShen	Page	9D
Standardize	GuopingZhou	Approve	XiaoyingRu	Date	25/09/2021

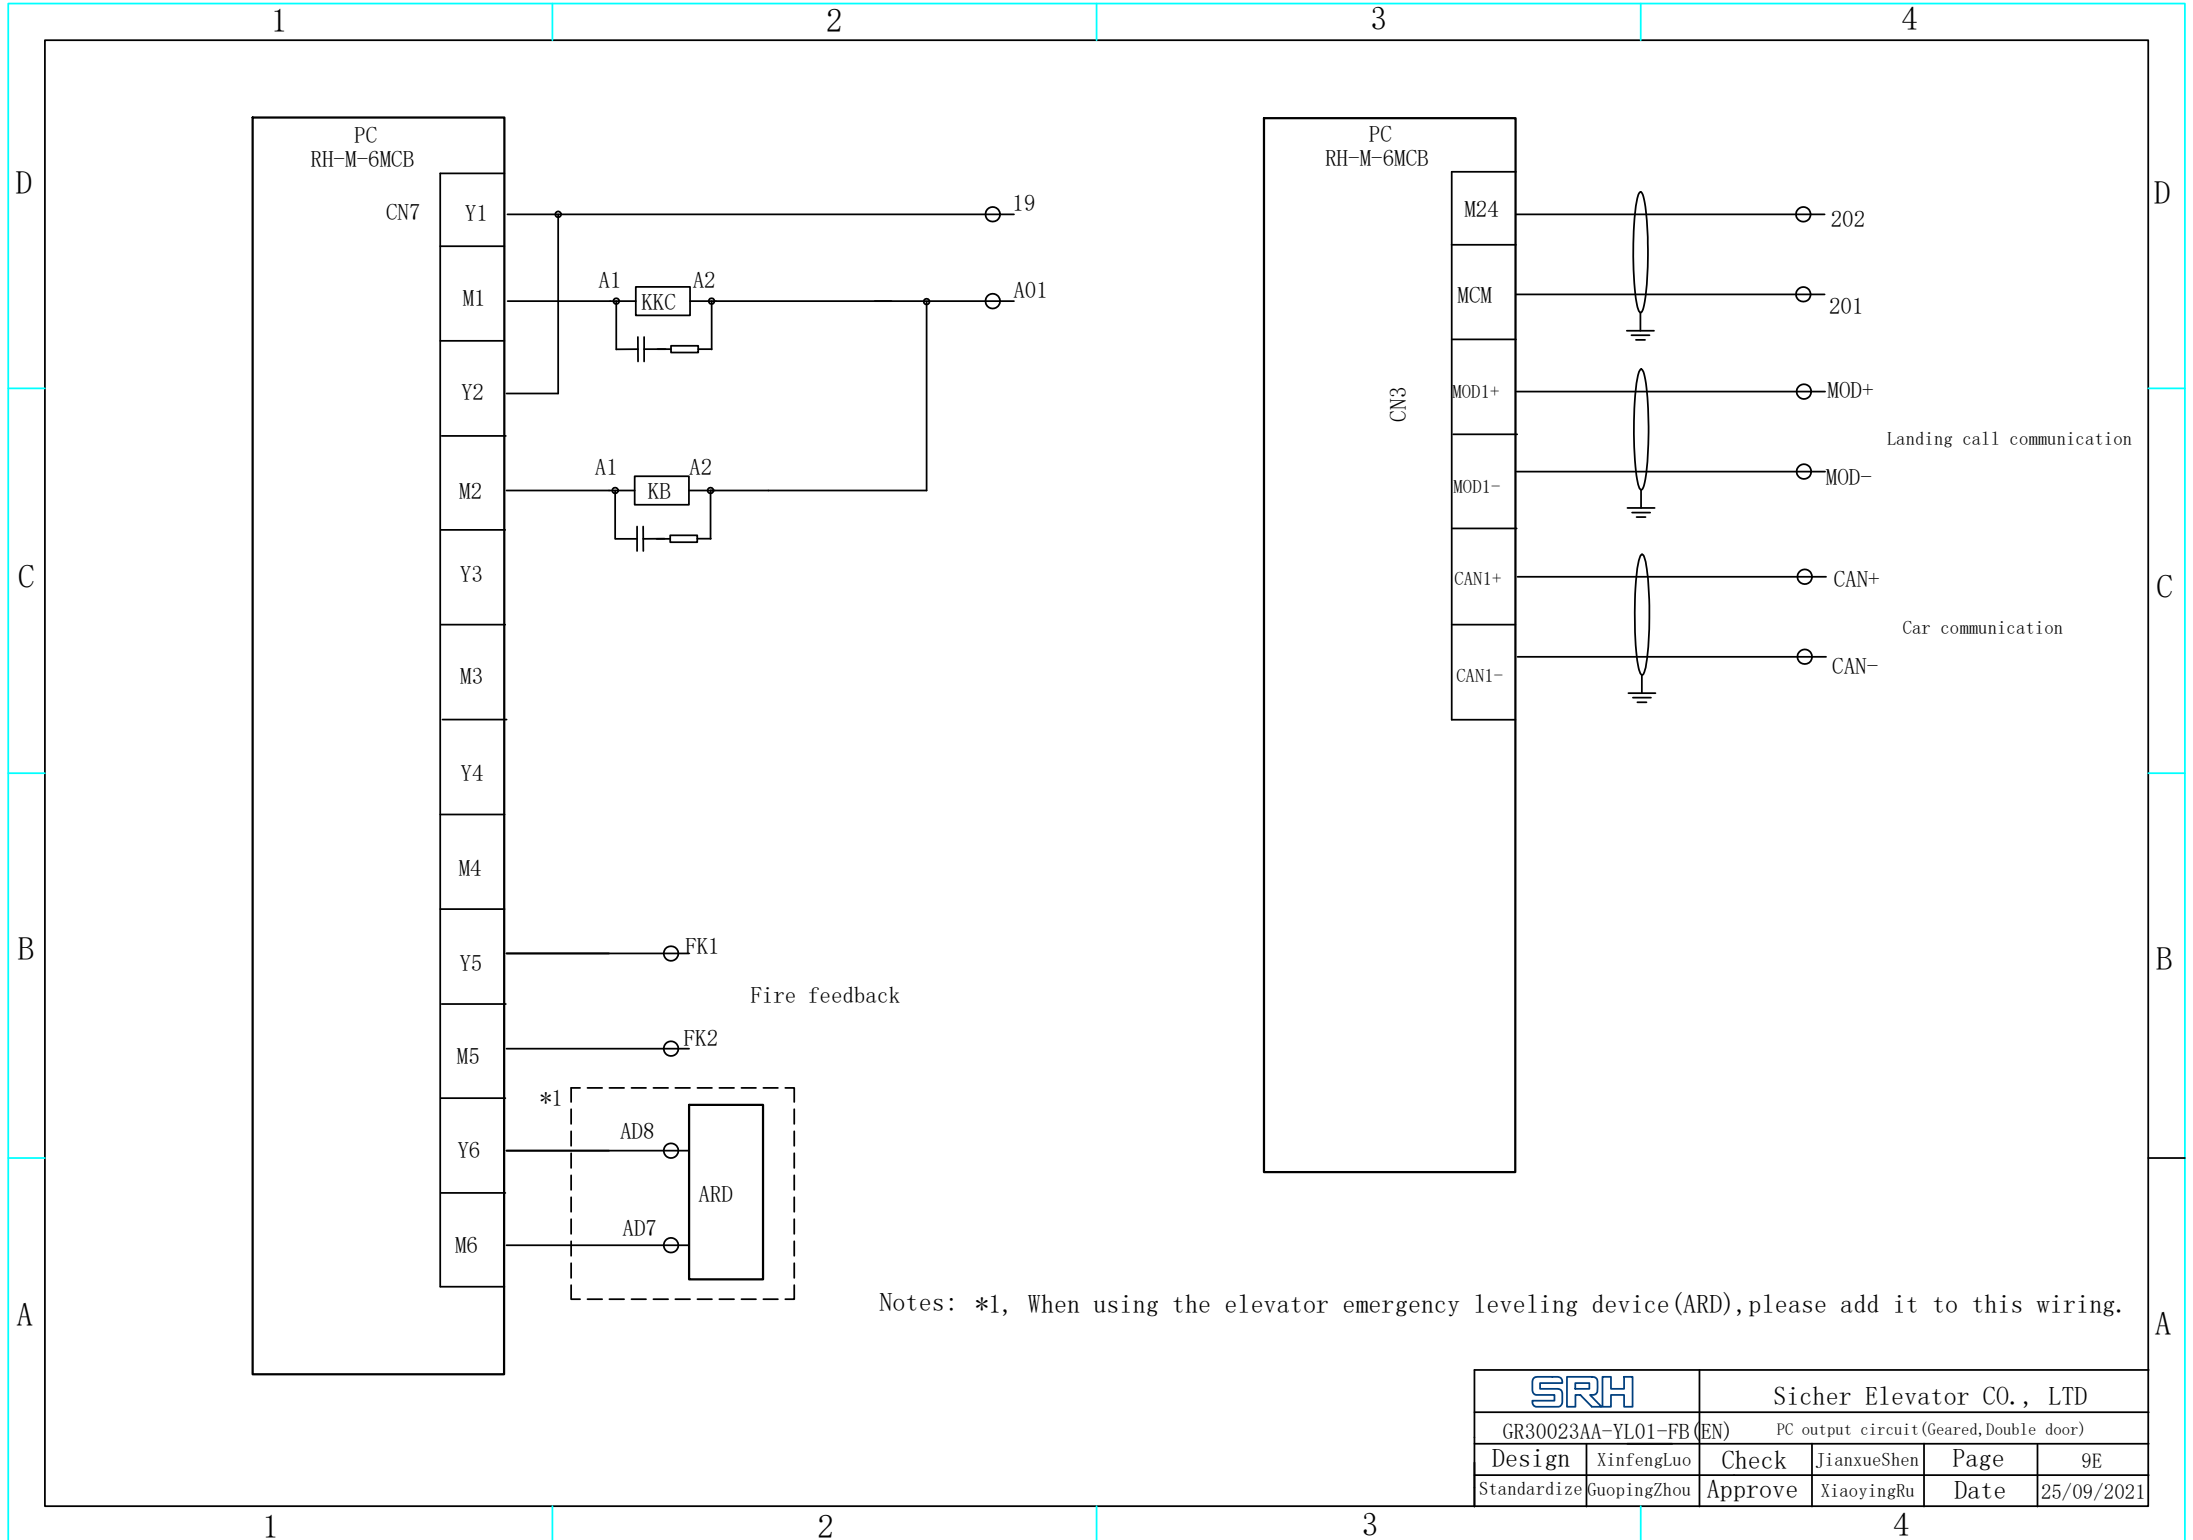

D

C

B



A

D



C

B

A

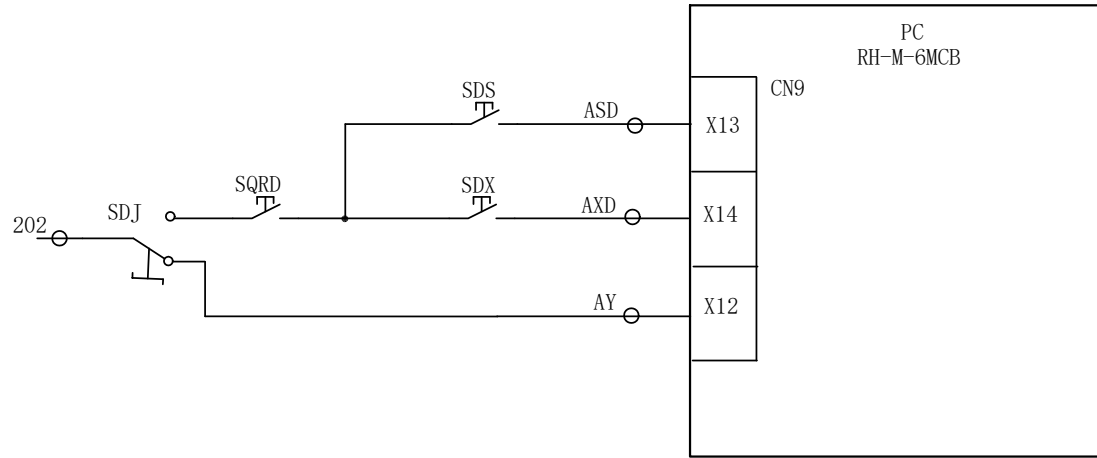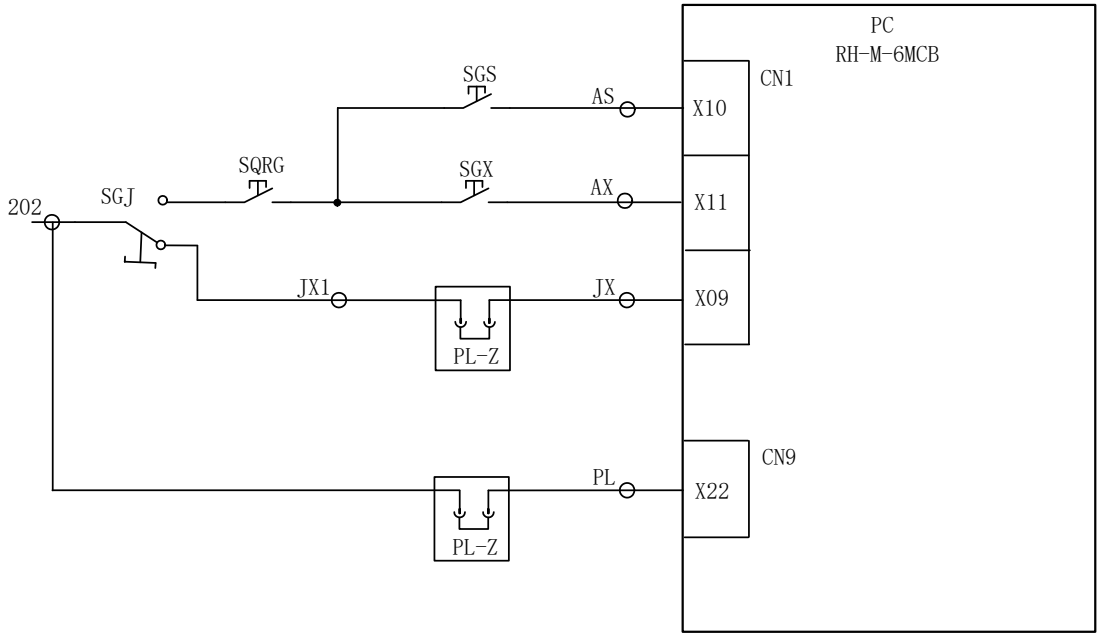


MRL Overspeed governor mechanical action and reset circuit

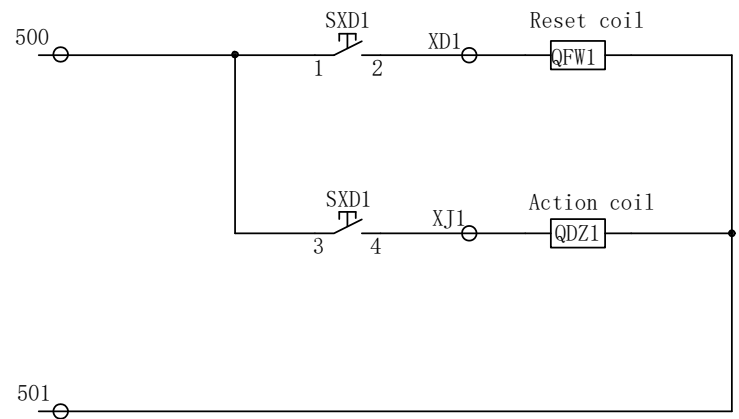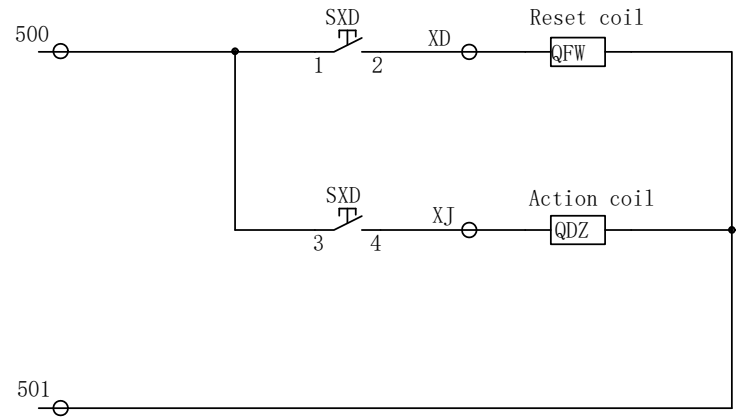

Configure when needed

SRH		Sicher Elevator CO., LTD			
GR30023AA-YL01-FB(EM)		Inspection circuit / MRL Overspeed governor control circuit			
Design	XinfengLuo	Check	JianxueShen	Page	10
Standardize	GuopingZhou	Approve	XiaoyingRu	Date	25/09/2021

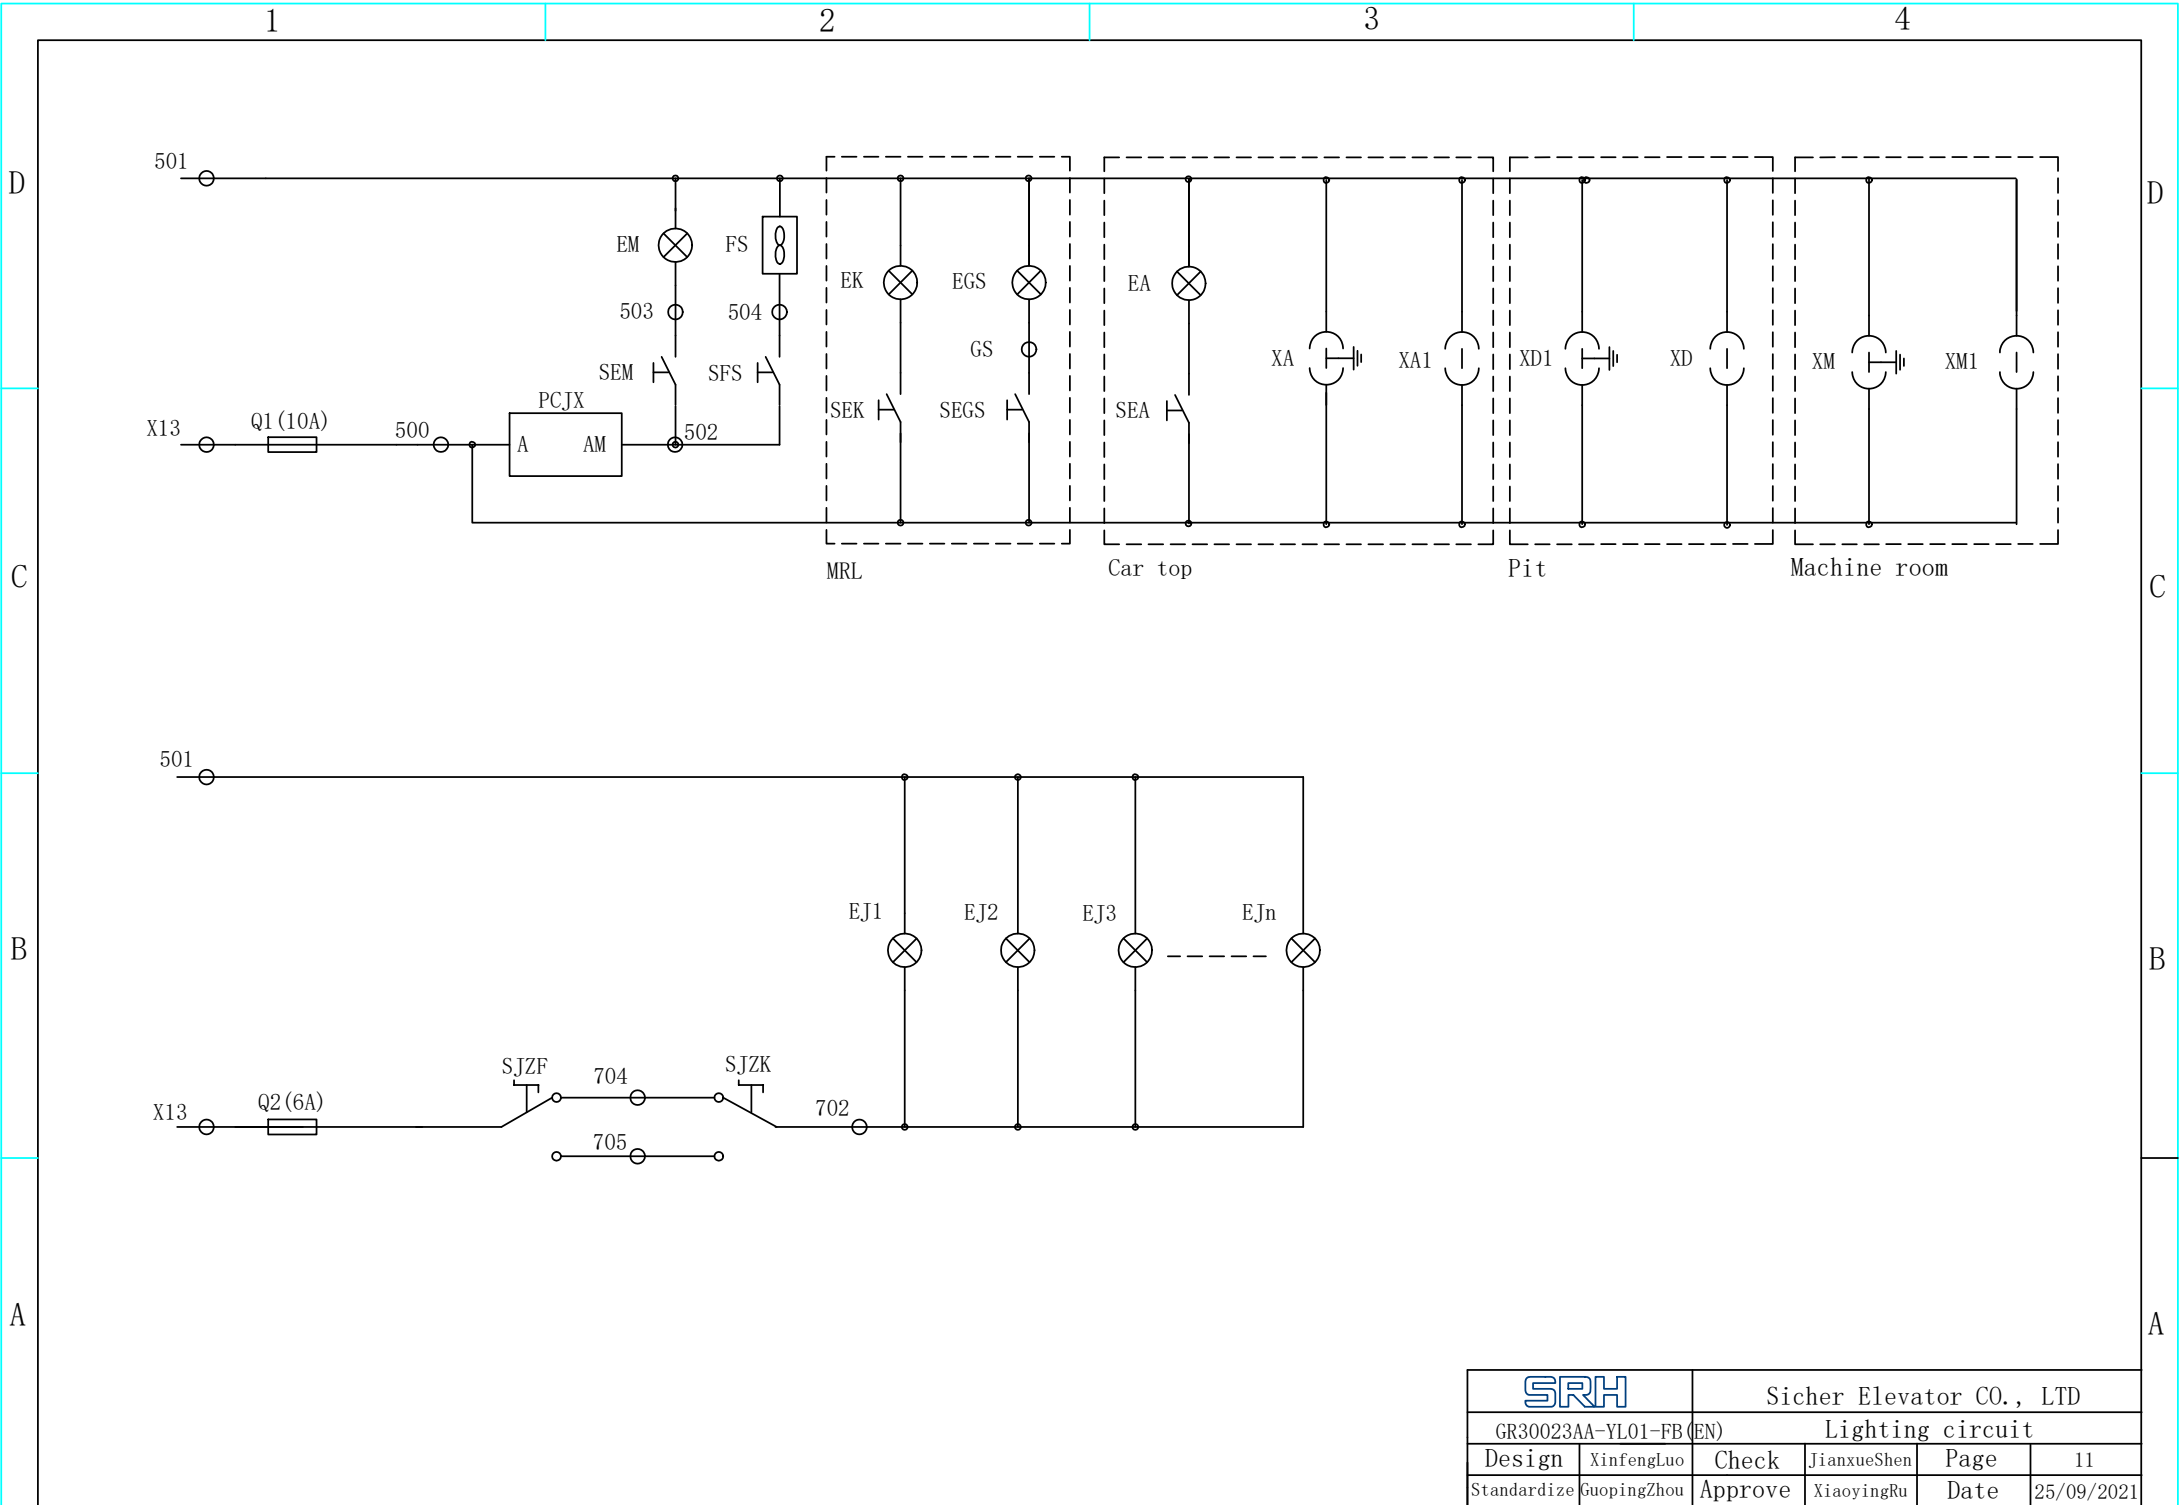

SRH		Sicher Elevator CO., LTD			
GR30023AA-YL01-FB (EN)		Lighting circuit			
Design	XinfengLuo	Check	JianxueShen	Page	11
Standardize	GuopingZhou	Approve	XiaoyingRu	Date	25/09/2021

D

D

C


C

B

B

A

A

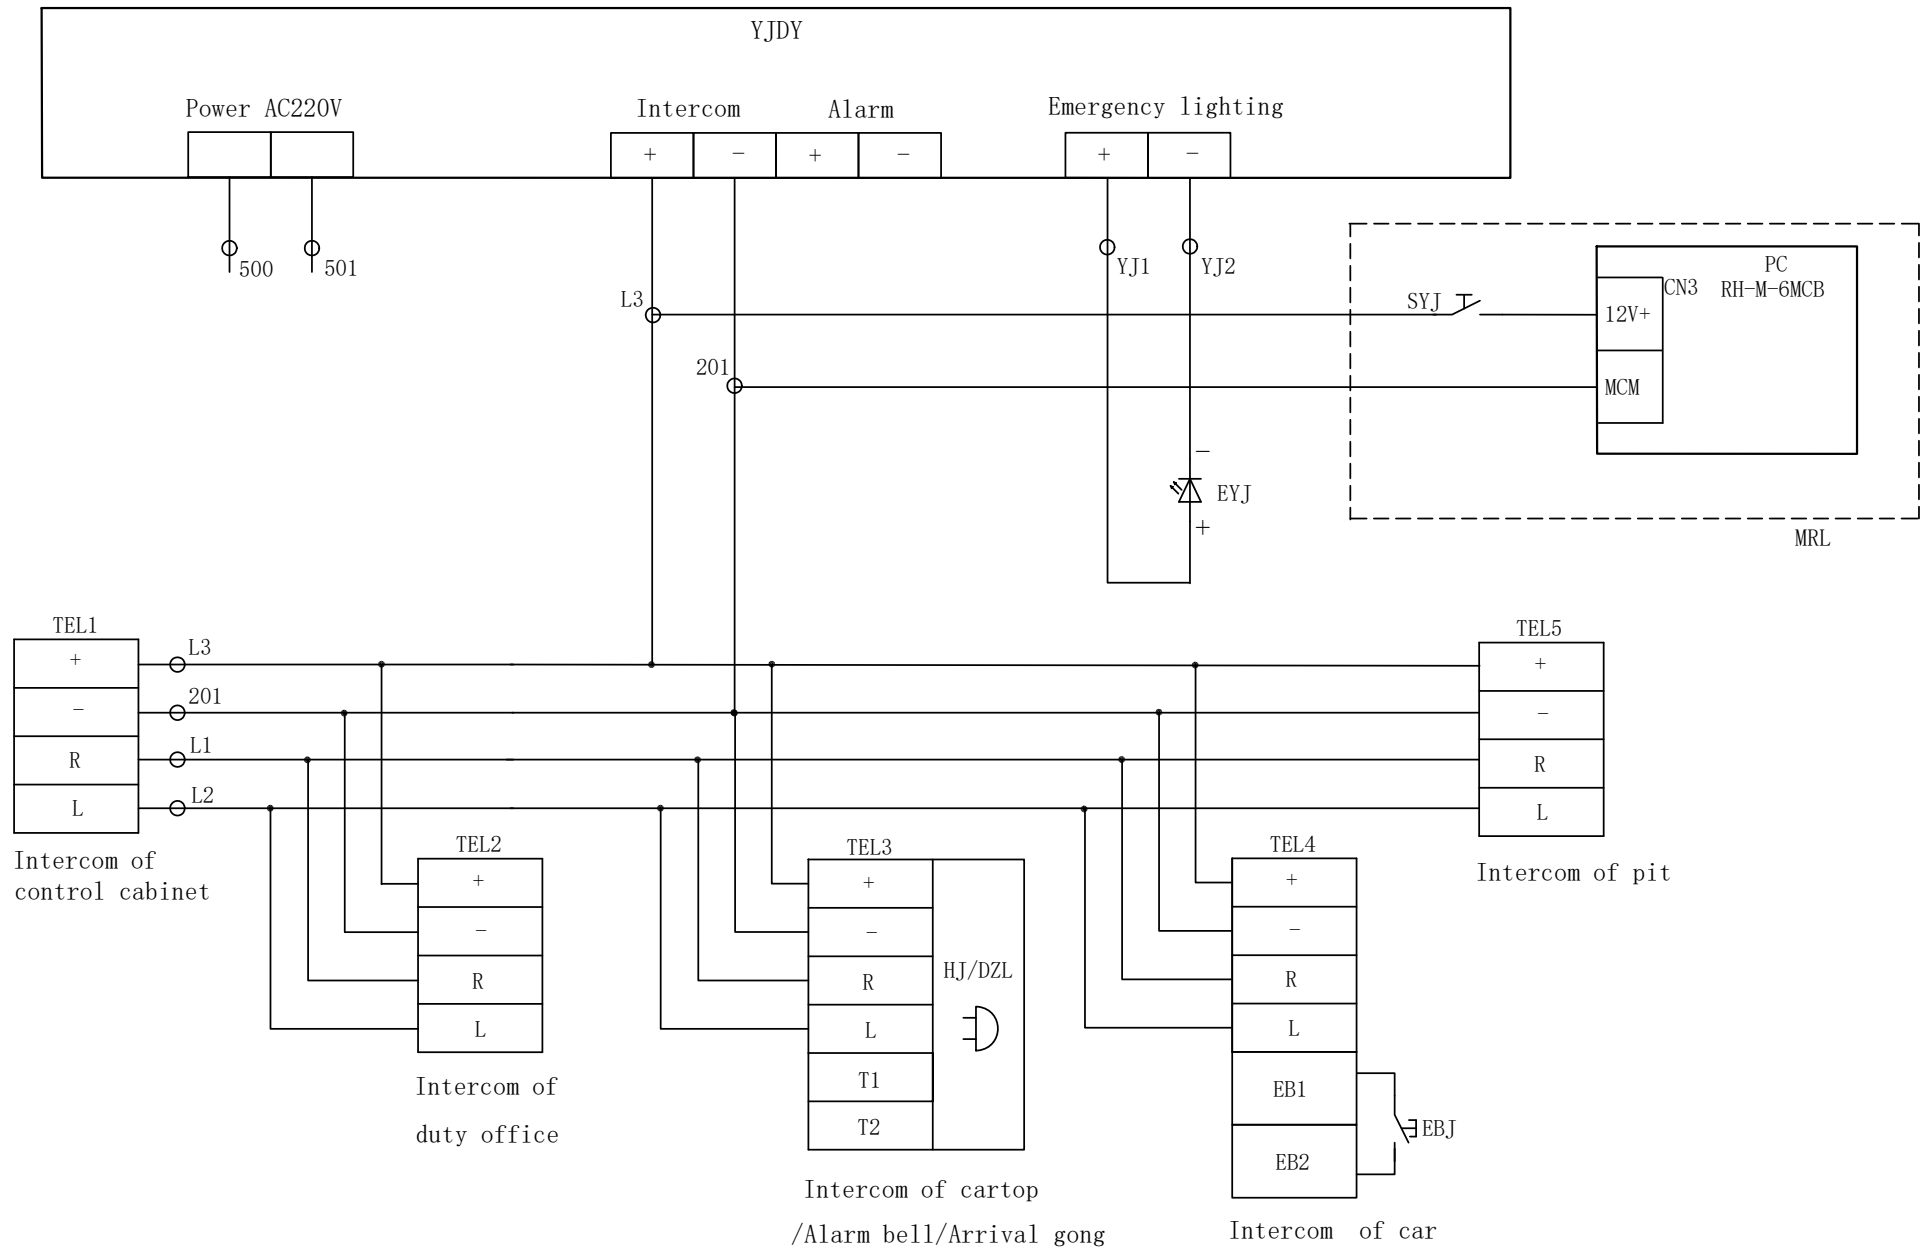

SRH		Sicher Elevator CO., LTD			
GR30023AA-YL01-FB(EN)		Emergency power circuit			
Design	XinfengLuo	Check	JianxueShen	Page	12
Standardize	GuopingZhou	Approve	XiaoyingRu	Date	25/09/2021

1

2

3

4

D

C

B


A

D

C

B

A

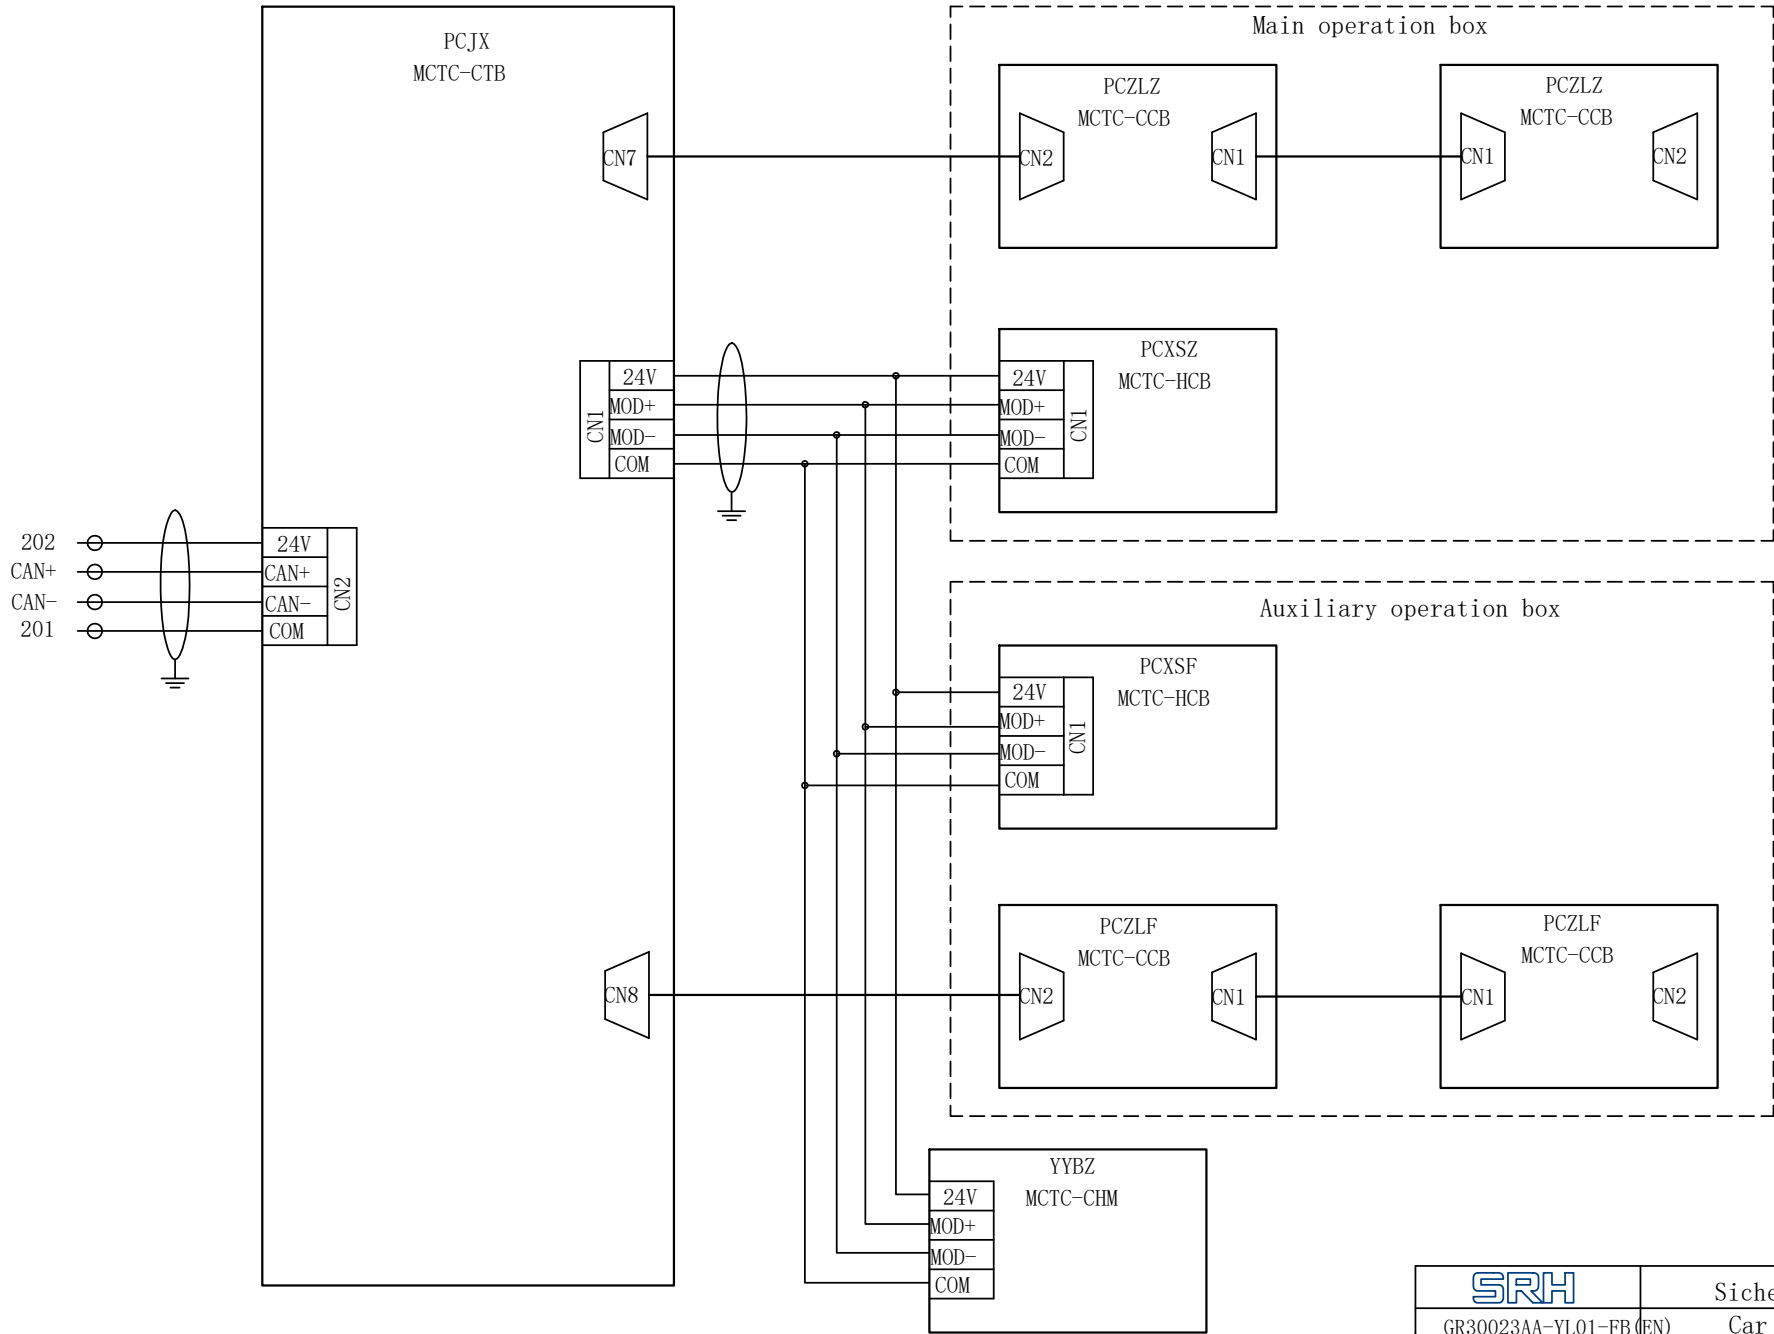

SRH		Sicher Elevator CO., LTD			
GR30023AA-YL01-FB(EN)		Car communication circuit			
Design	XinfengLuo	Check	JianxueShen	Page	13
Standardize	GuopingZhou	Approve	XiaoyingRu	Date	25/09/2021

D

C

B


A

D

C

B

A

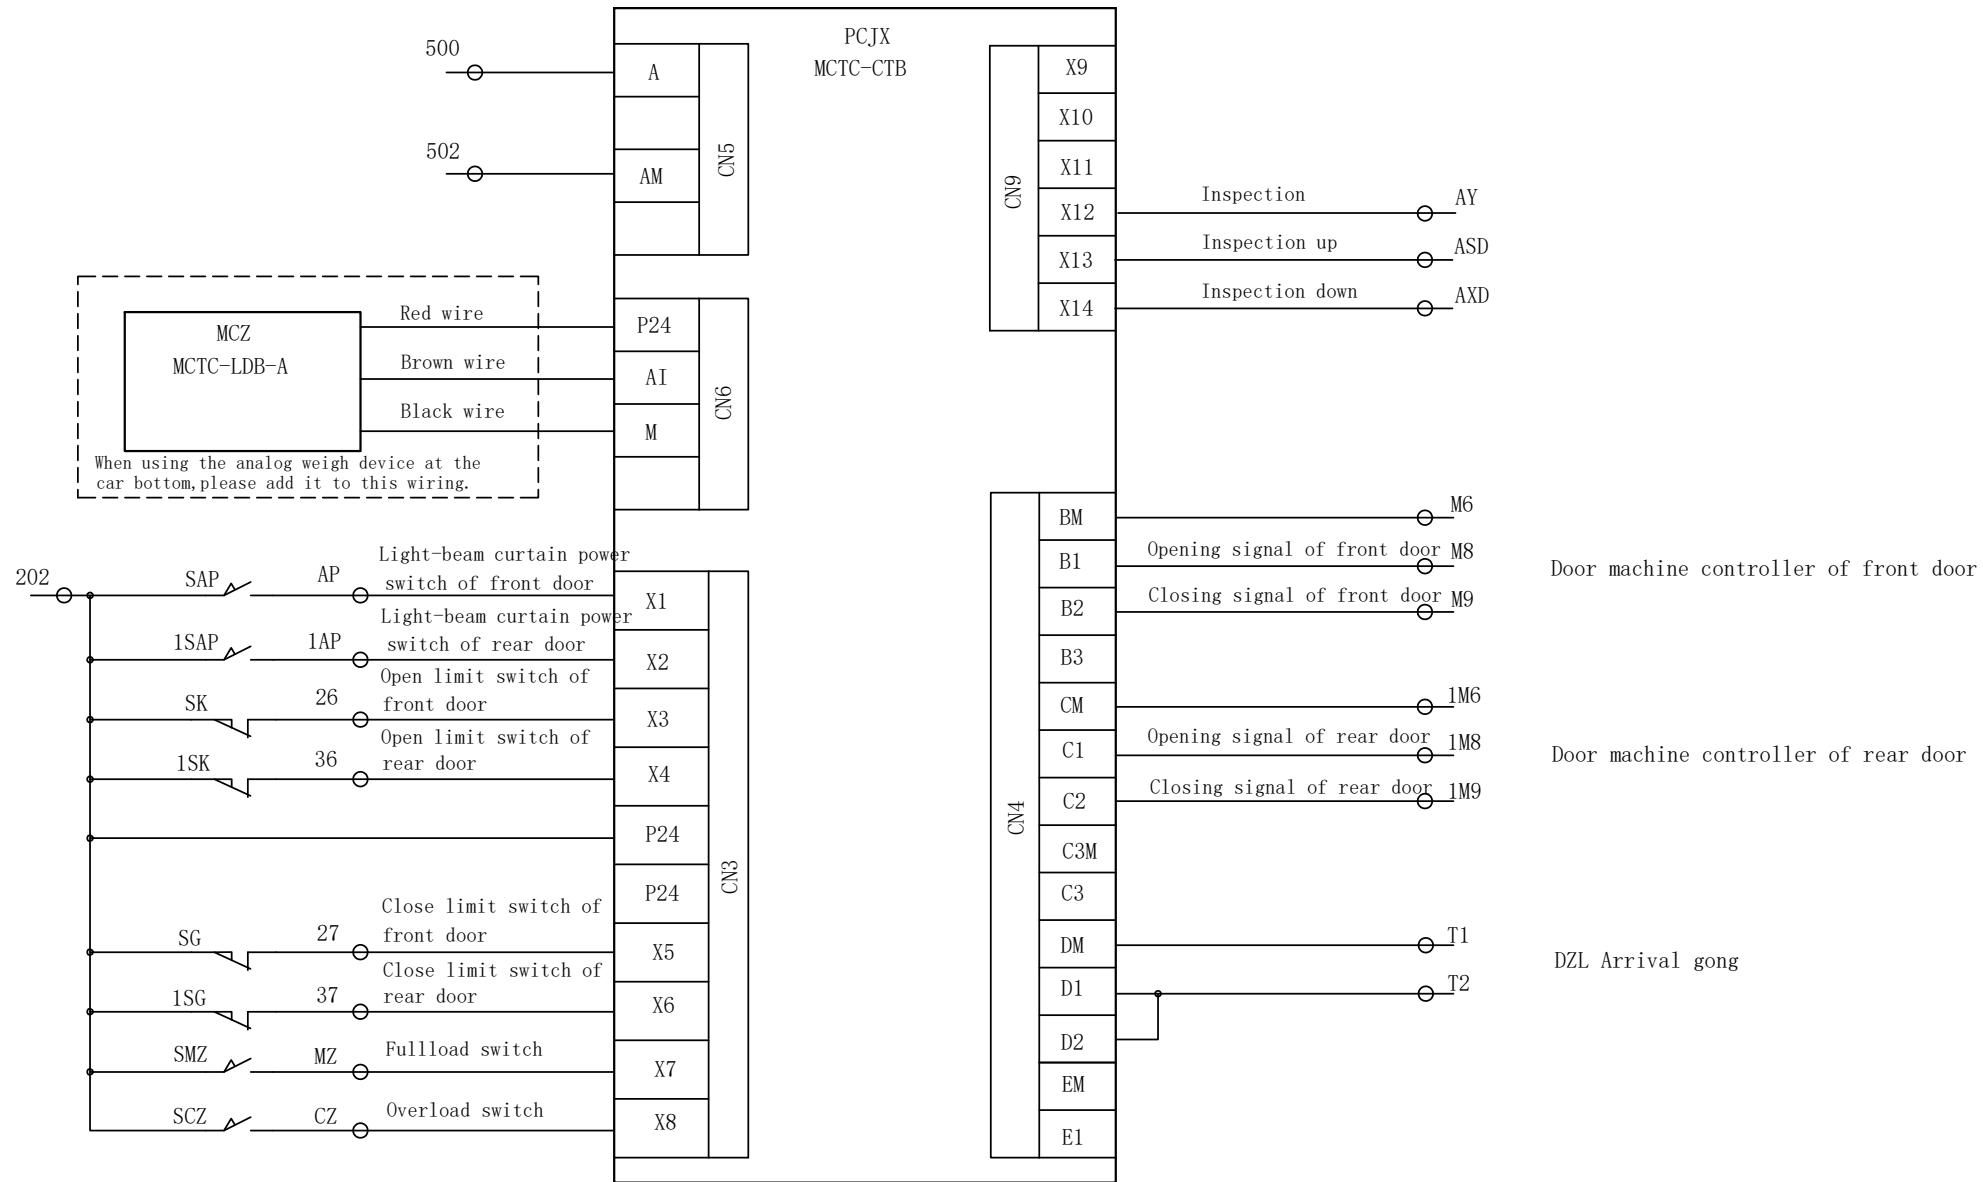

SRH		Sicher Elevator CO., LTD			
GR30023AA-YL01-FB(EN) Car top control board circuit					
Design	XinfengLuo	Check	JianxueShen	Page	14
Standardize	GuopingZhou	Approve	XiaoyingRu	Date	25/09/2021

D

D

C



C

B


B

A

A

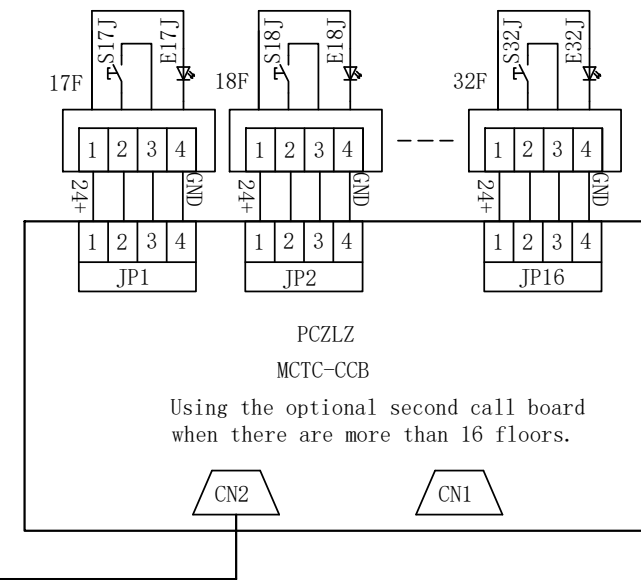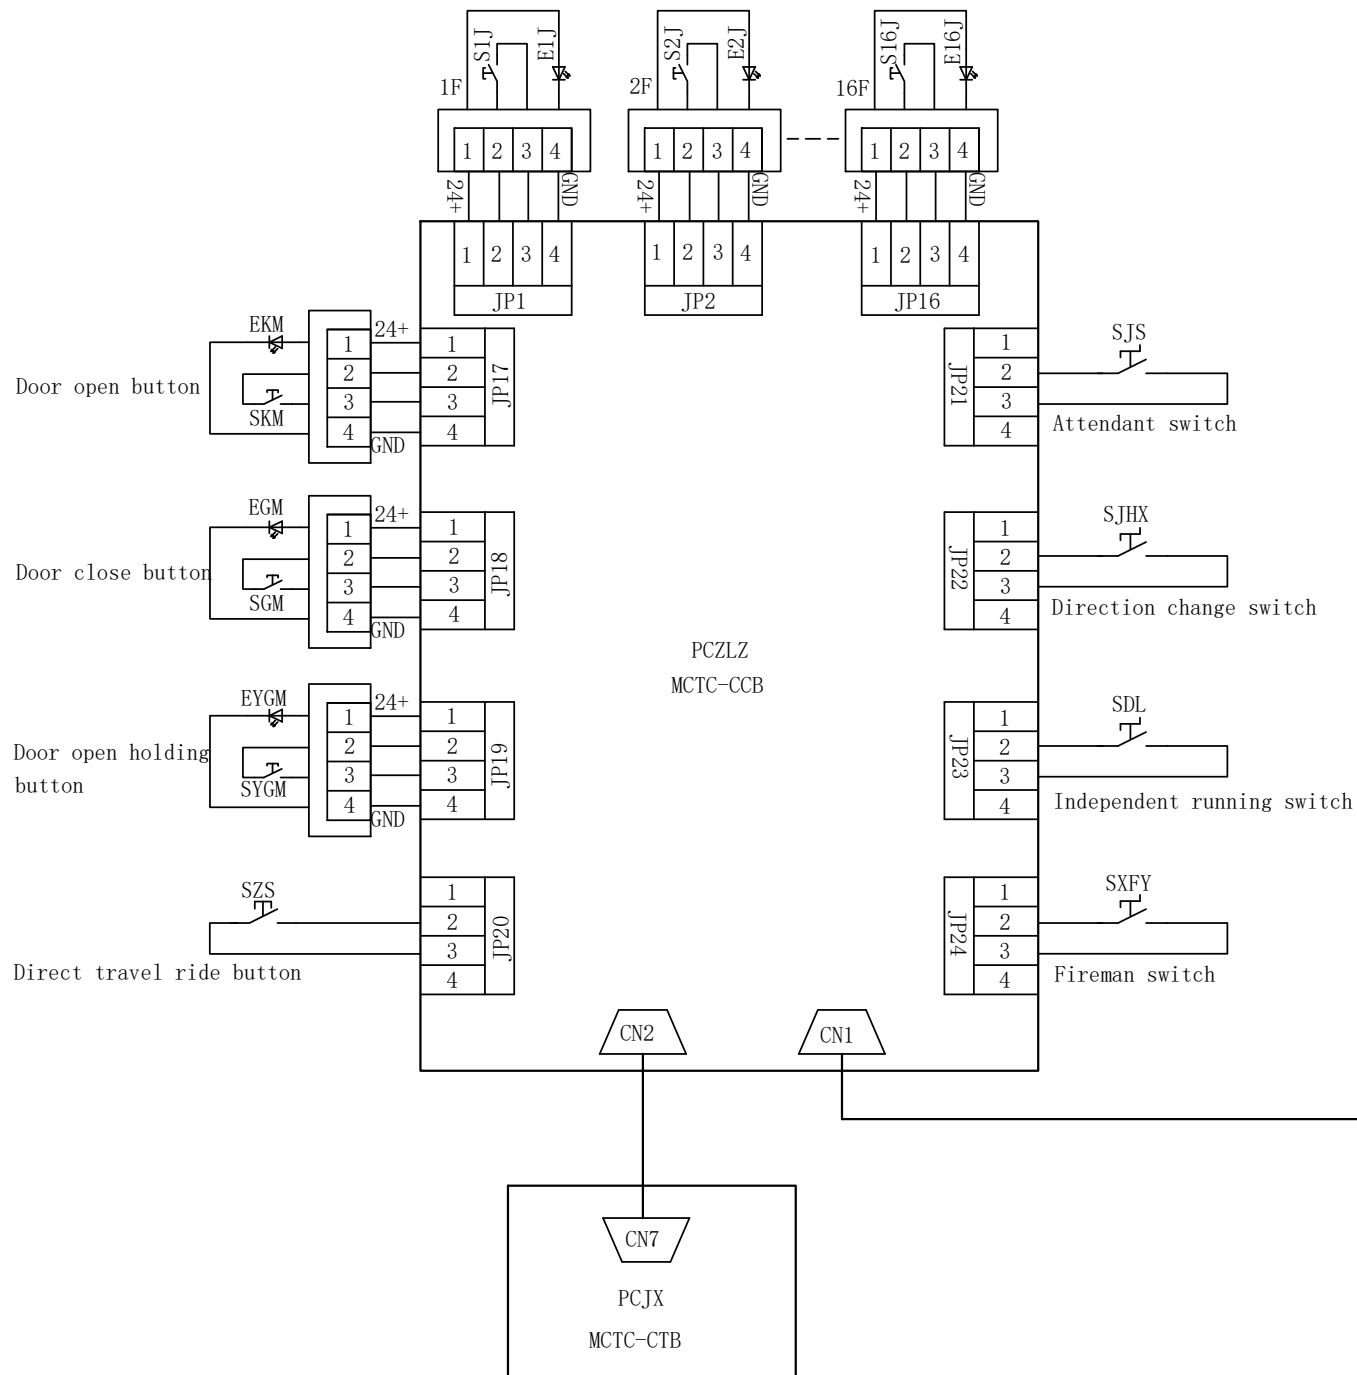

SRH		Sicher Elevator CO., LTD			
GR30023AA-YL01-FB(EN) Main operation box control					
Design	XinfengLuo	Check	JianxueShen	Page	15
Standardize	GuopingZhou	Approve	XiaoyingRu	Date	25/09/2021

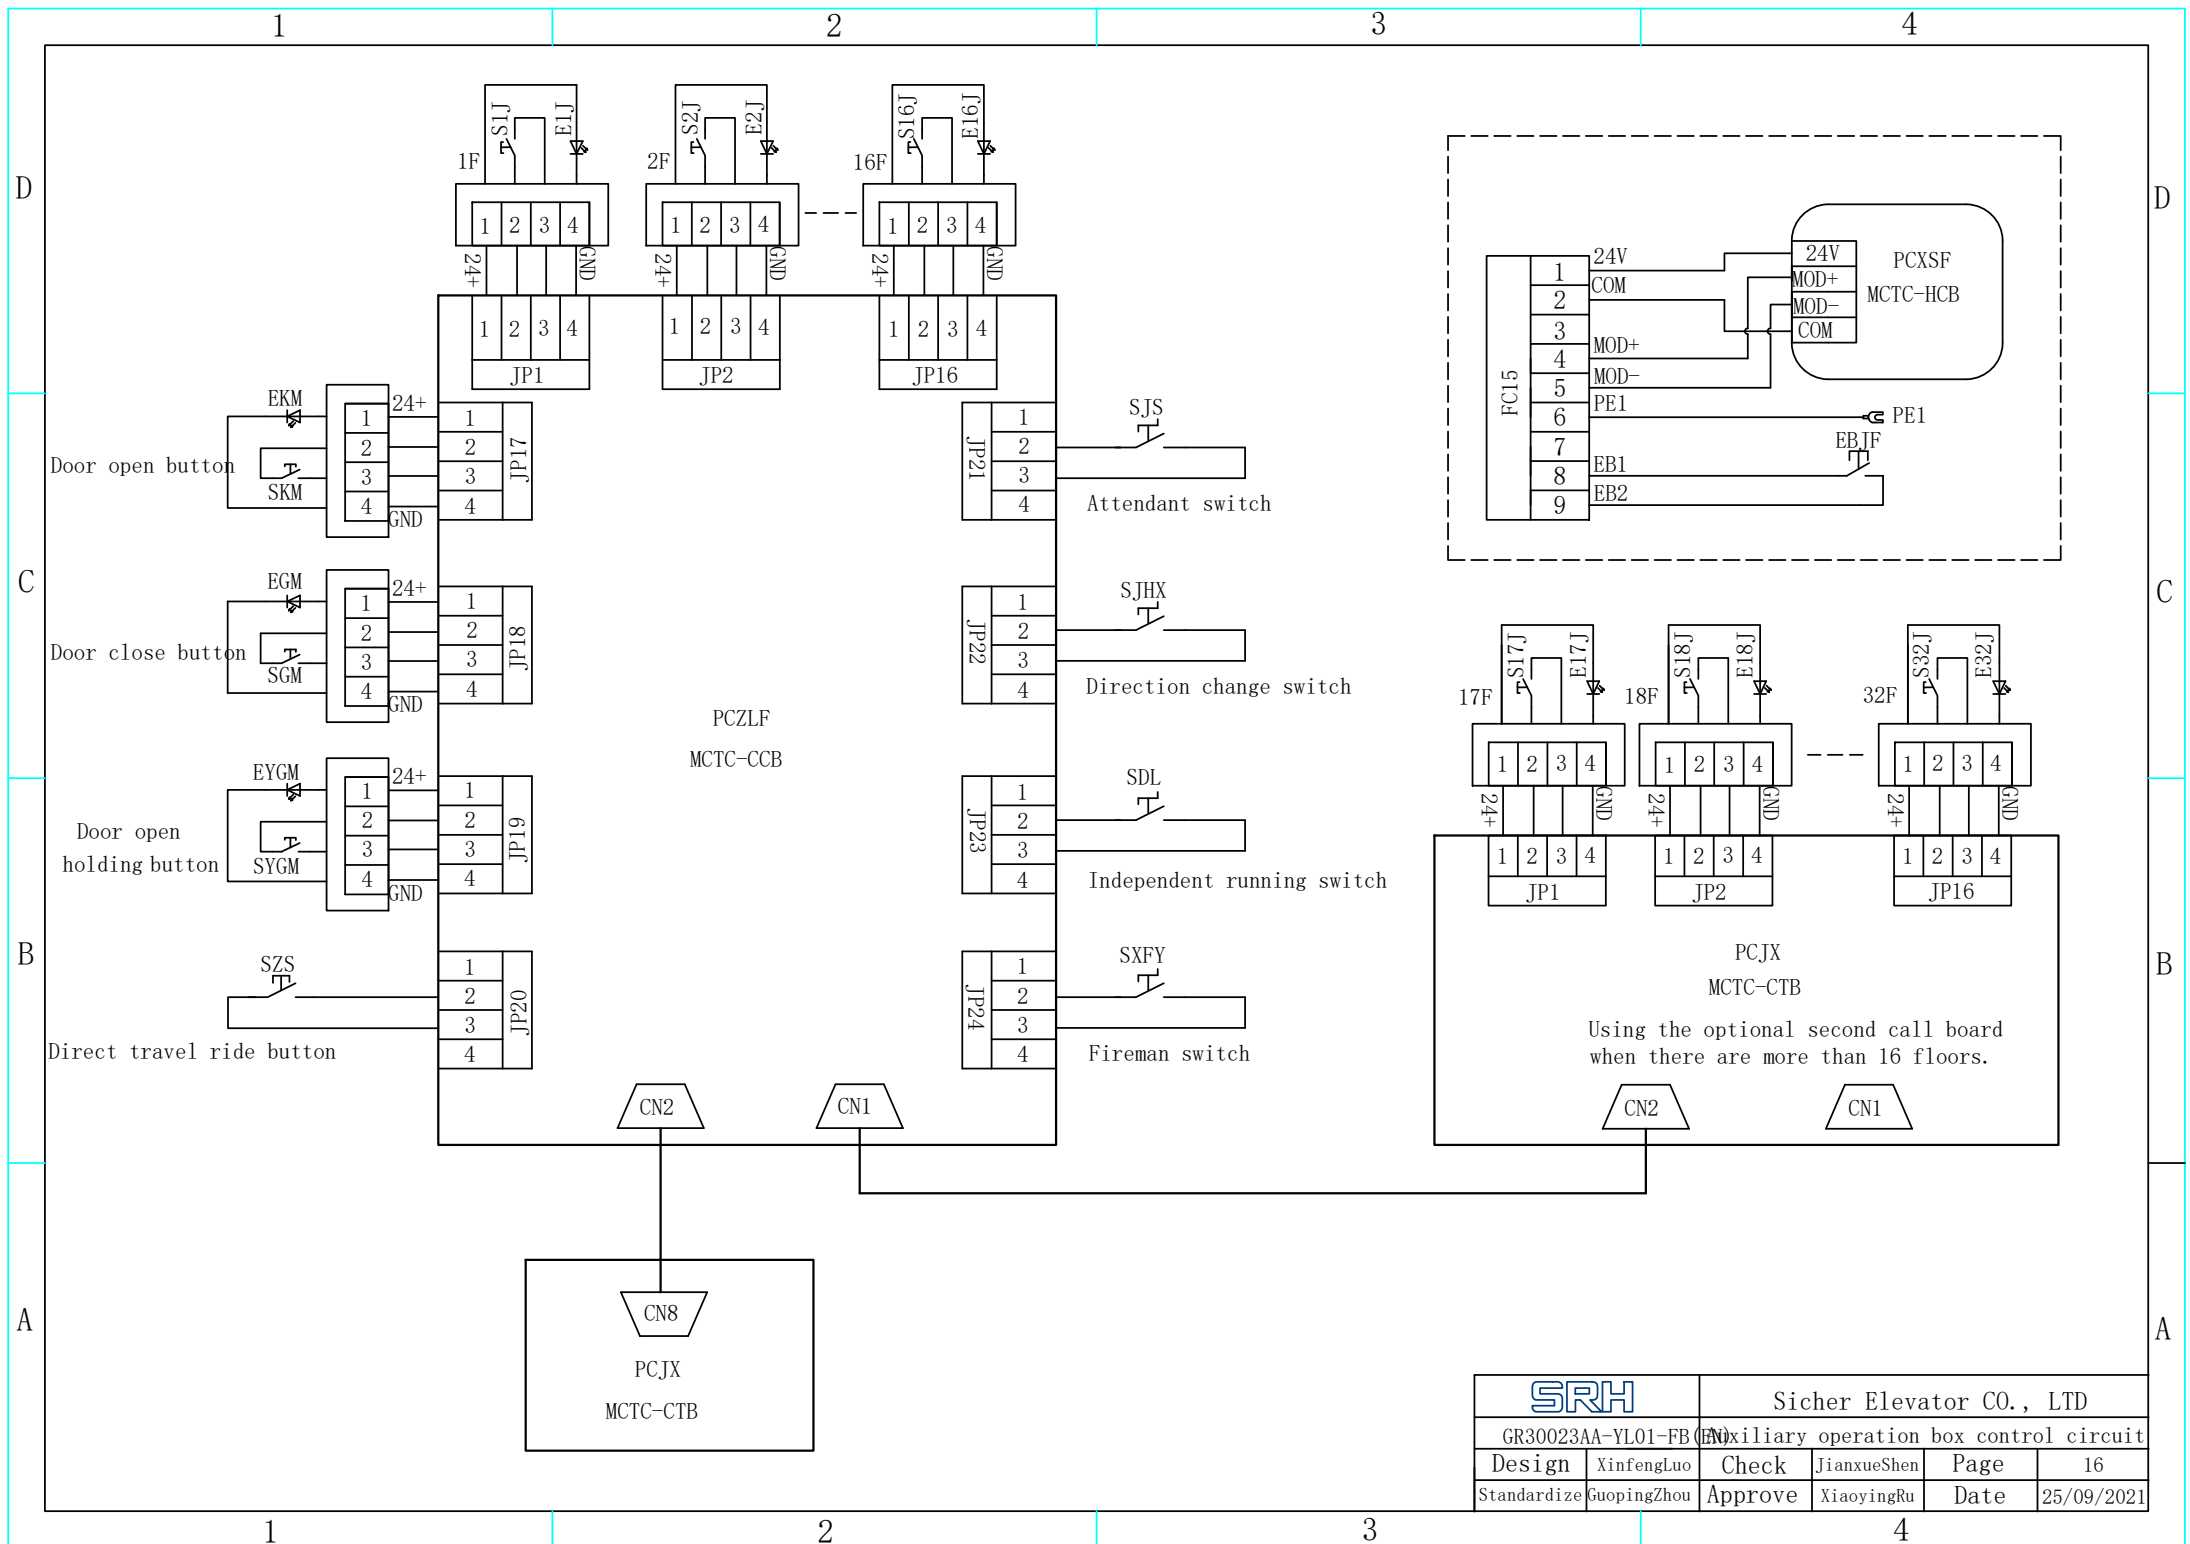

D

C

B




A

D

C

B

A

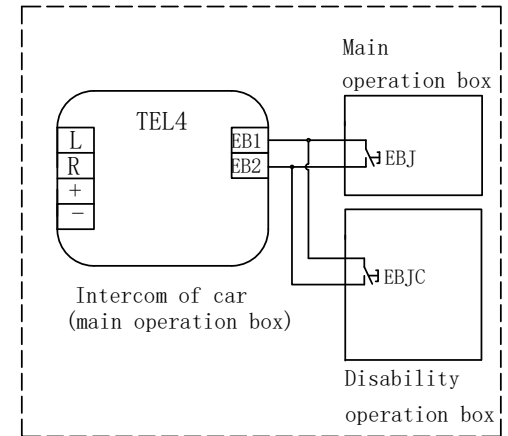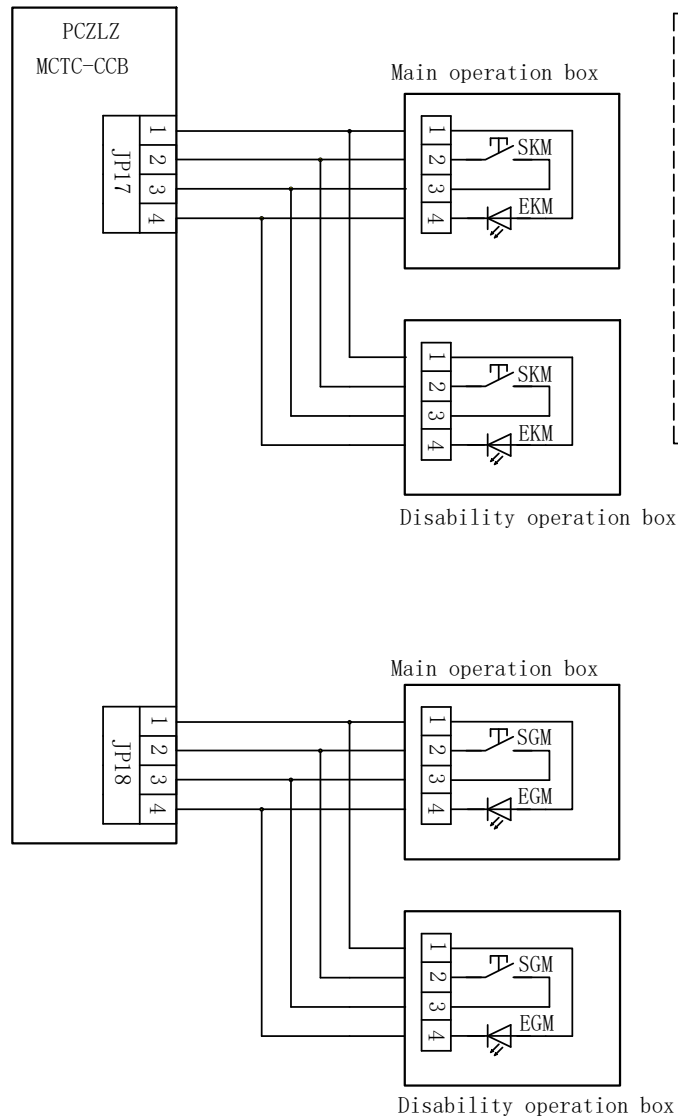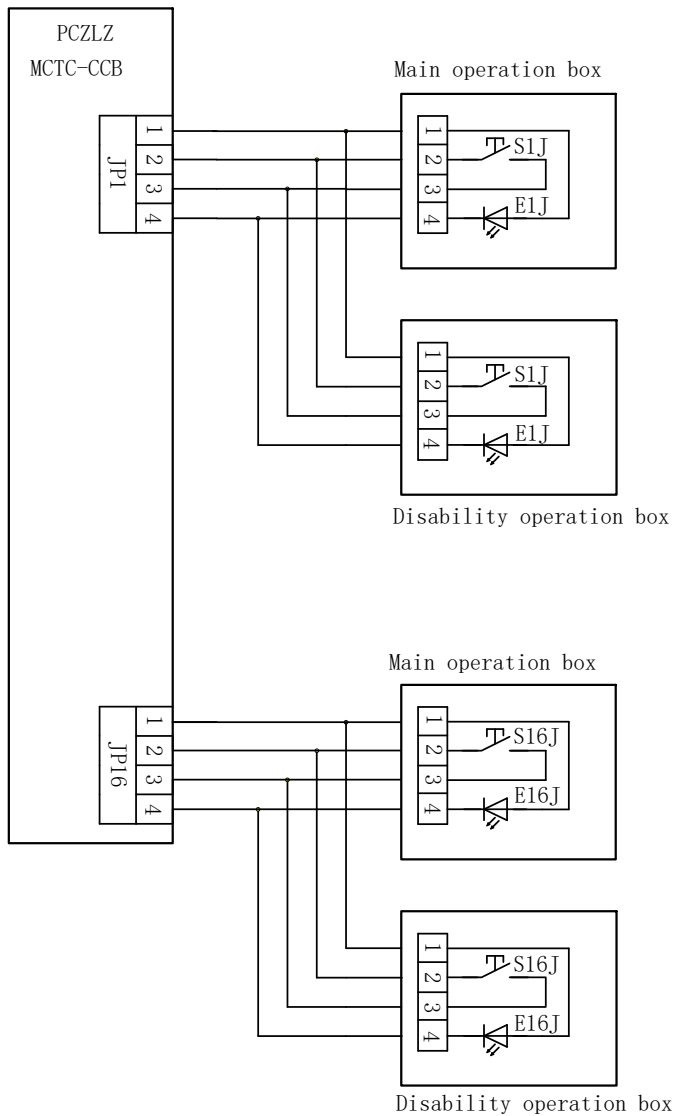

This page applies to: When has auxiliary operation box and disability operation box,
the buttons are connected in parallel.

SRH		Sicher Elevator CO., LTD			
GR30023AA-YL01-FB(EN)		Disabled operation box control circuit			
Design	XinfengLuo	Check	JianxueShen	Page	17A
Standardize	GuopingZhou	Approve	XiaoyingRu	Date	25/09/2021

D

C

B


A

D


C


B

A

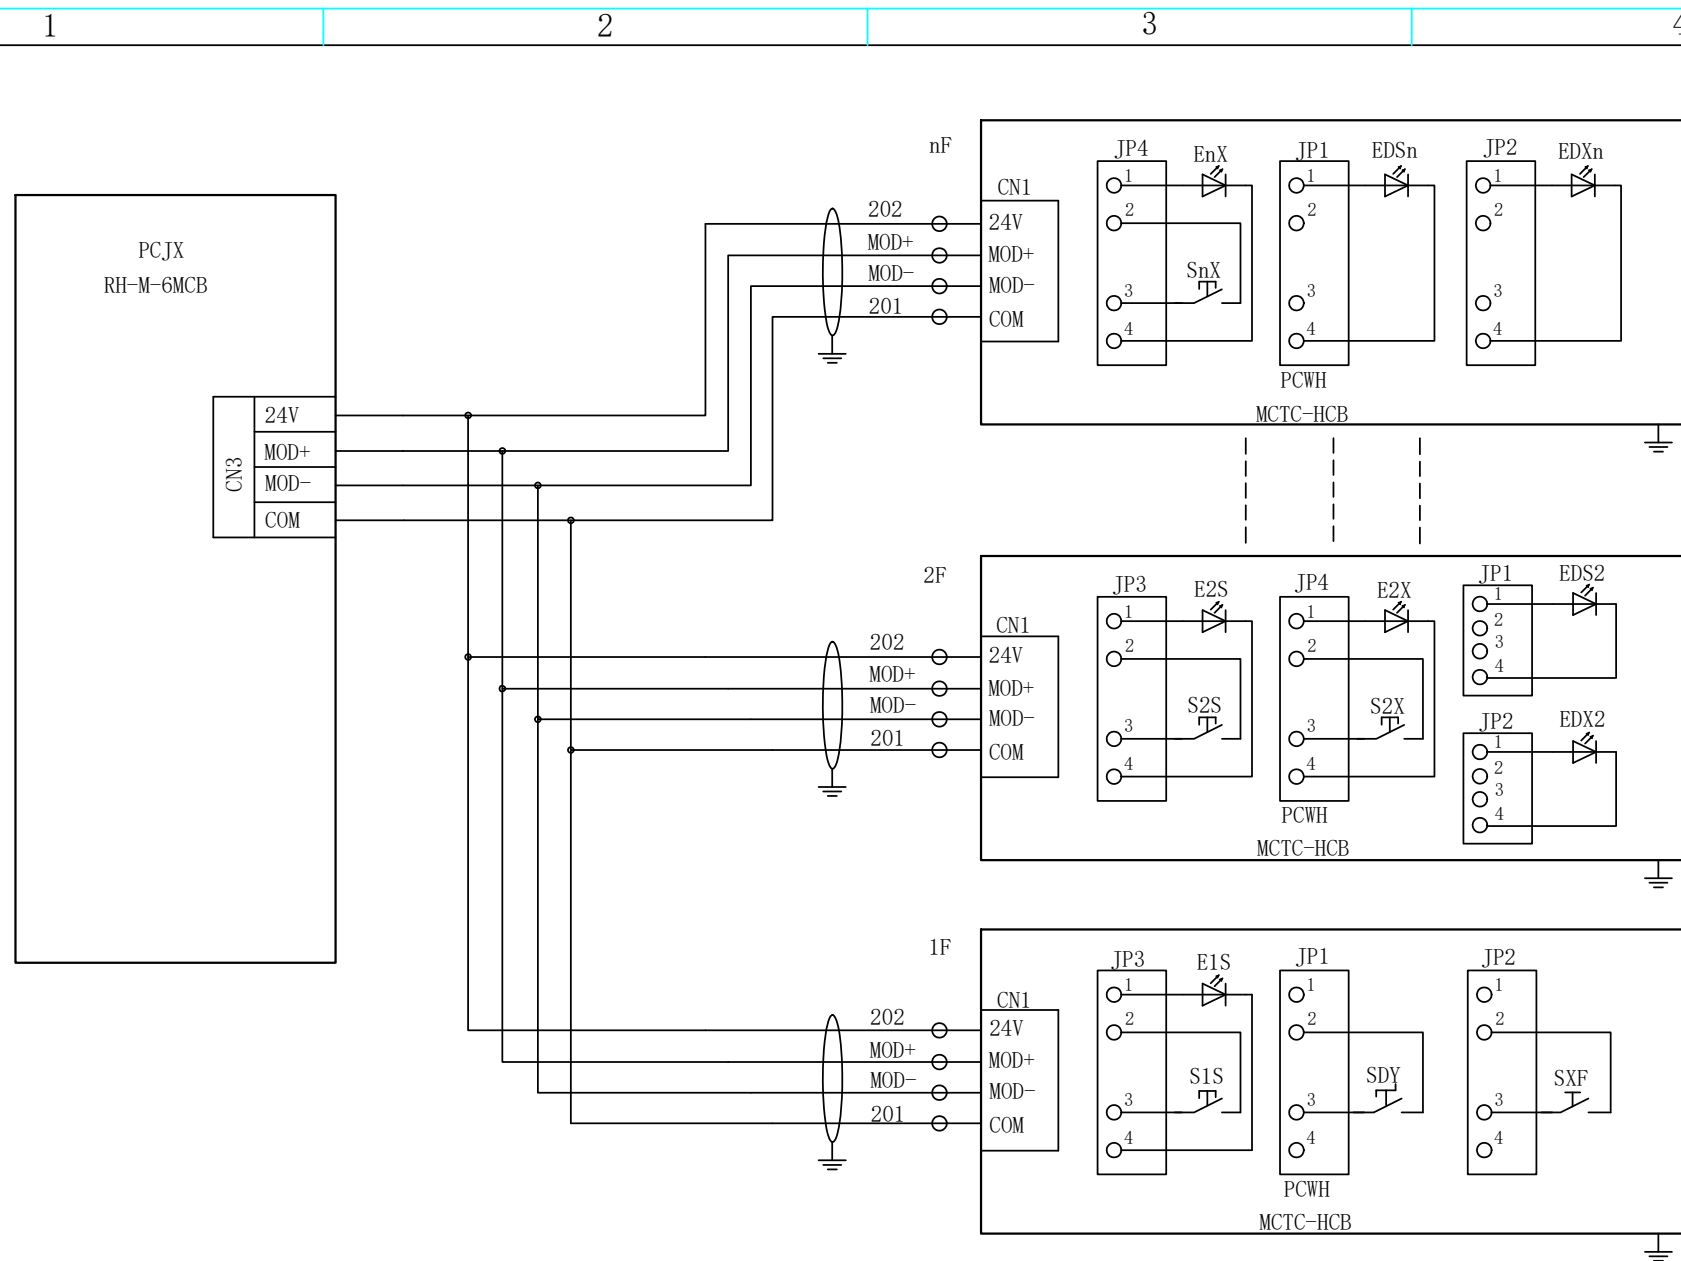

SRH		Sicher Elevator CO., LTD			
GR30023AA-YL01-FB (EN)		Landing communication			
Design	XinfengLuo	Check	JianxueShen	Page	18
Standardize	GuopingZhou	Approve	XiaoyingRu	Date	25/09/2021

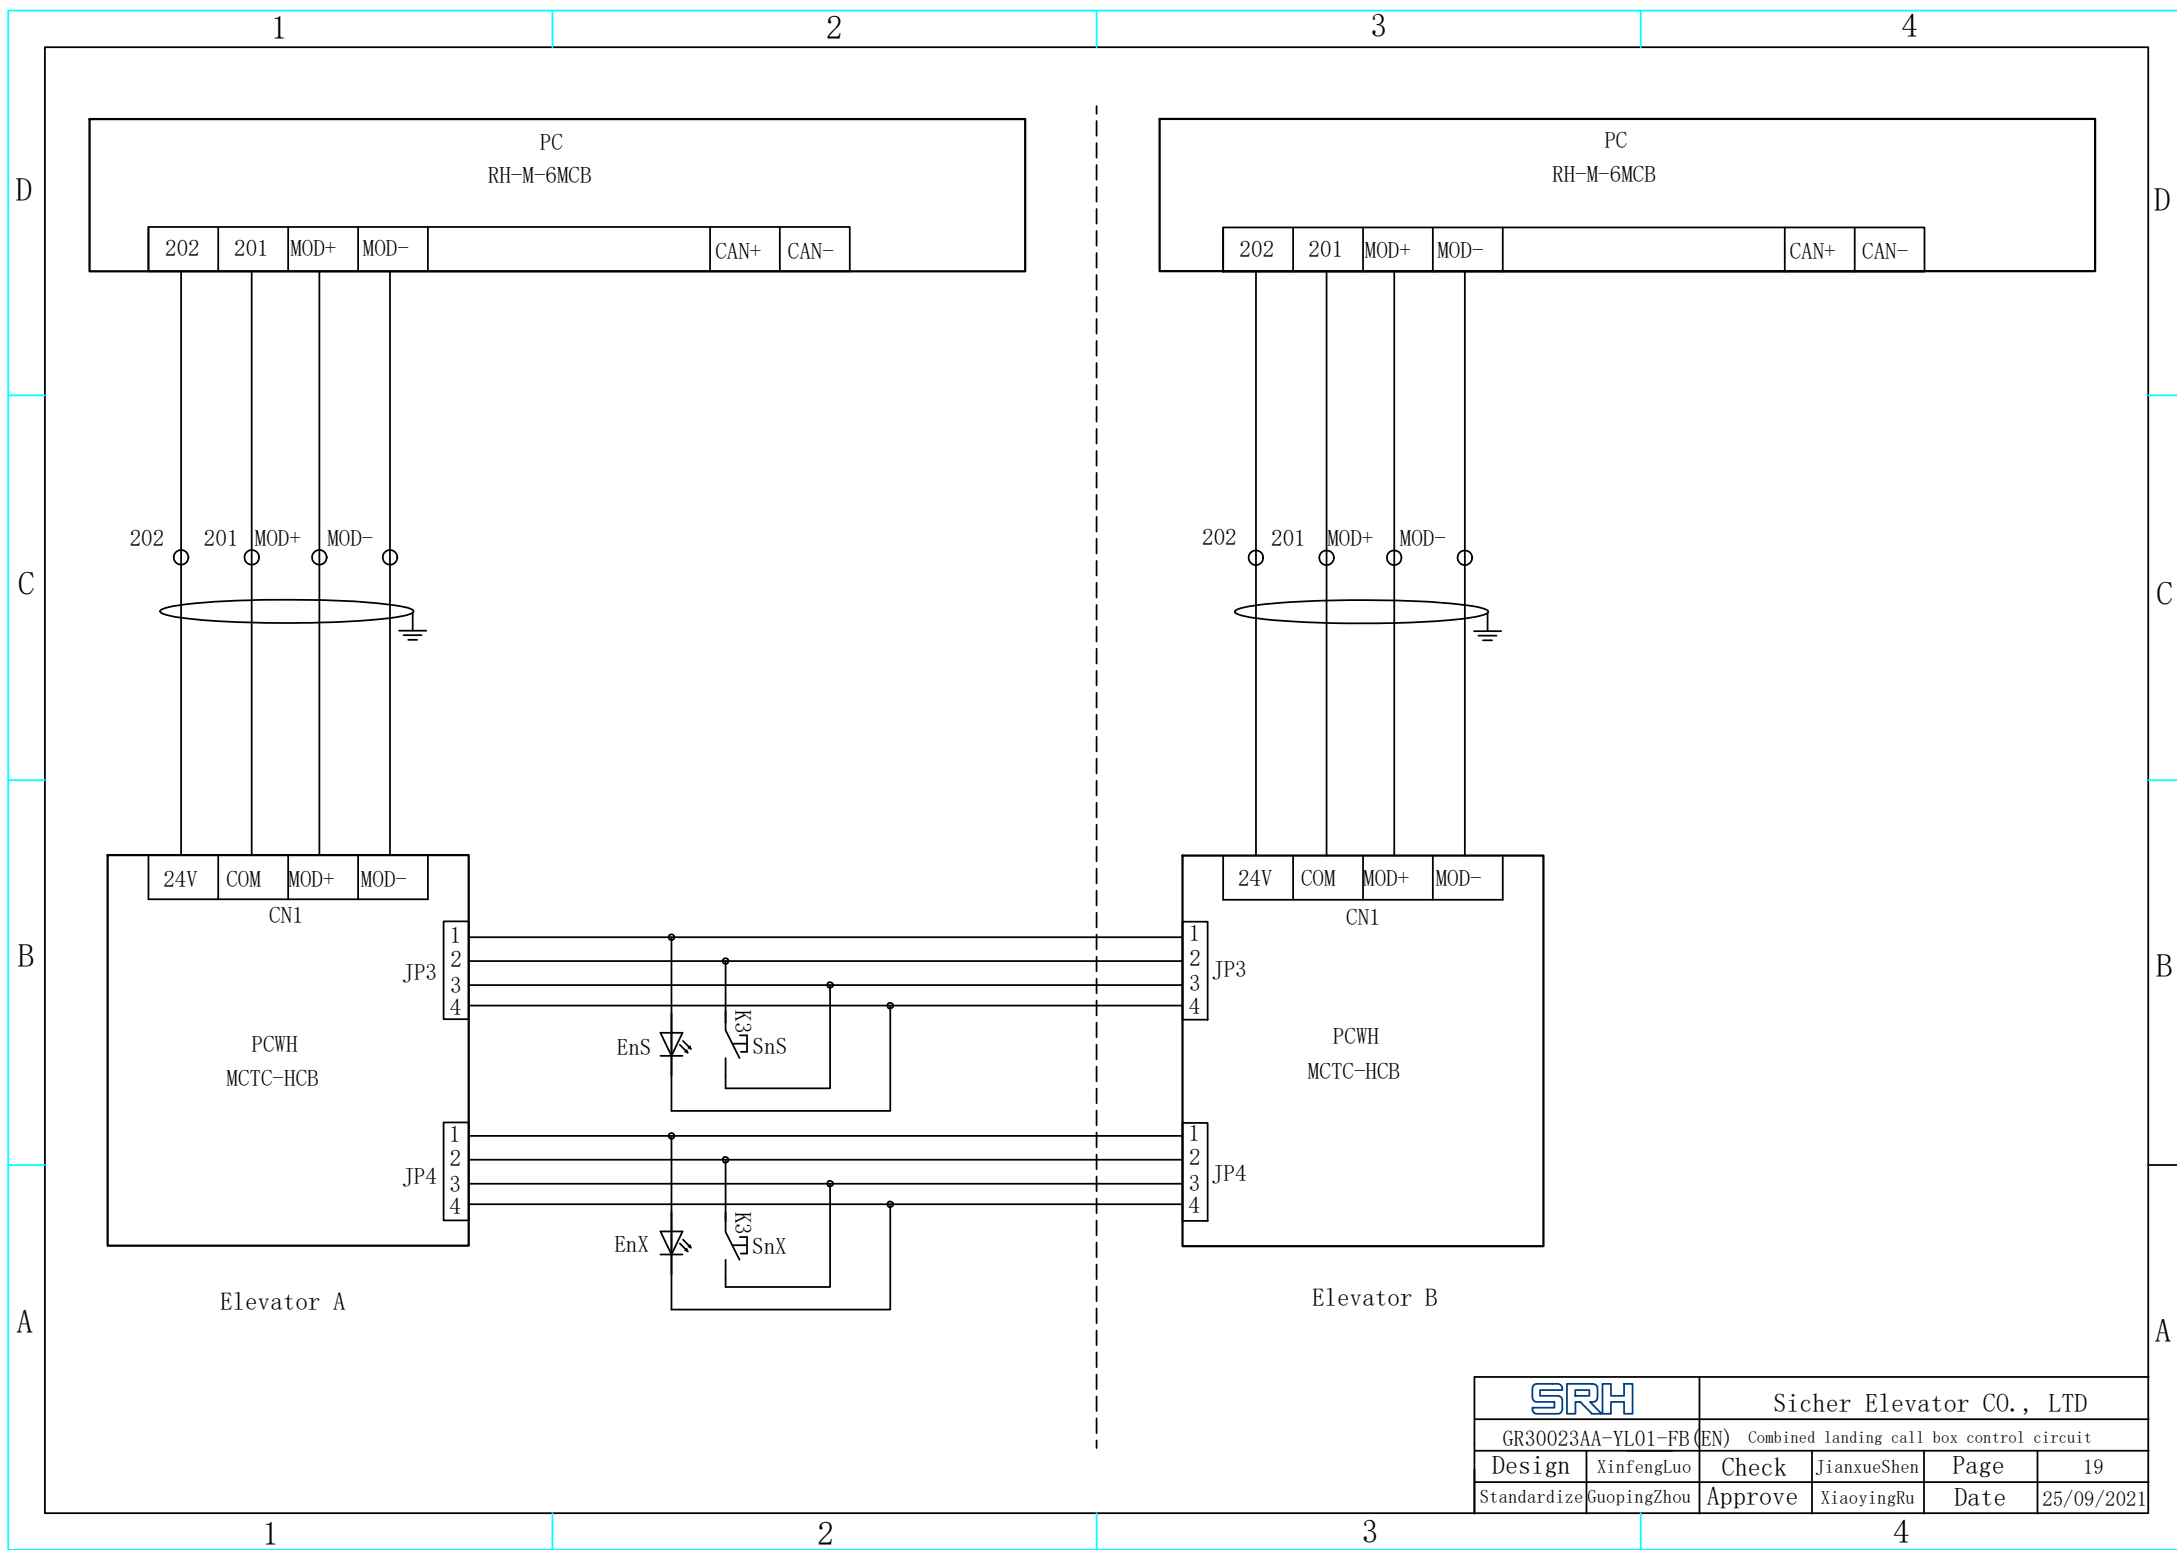

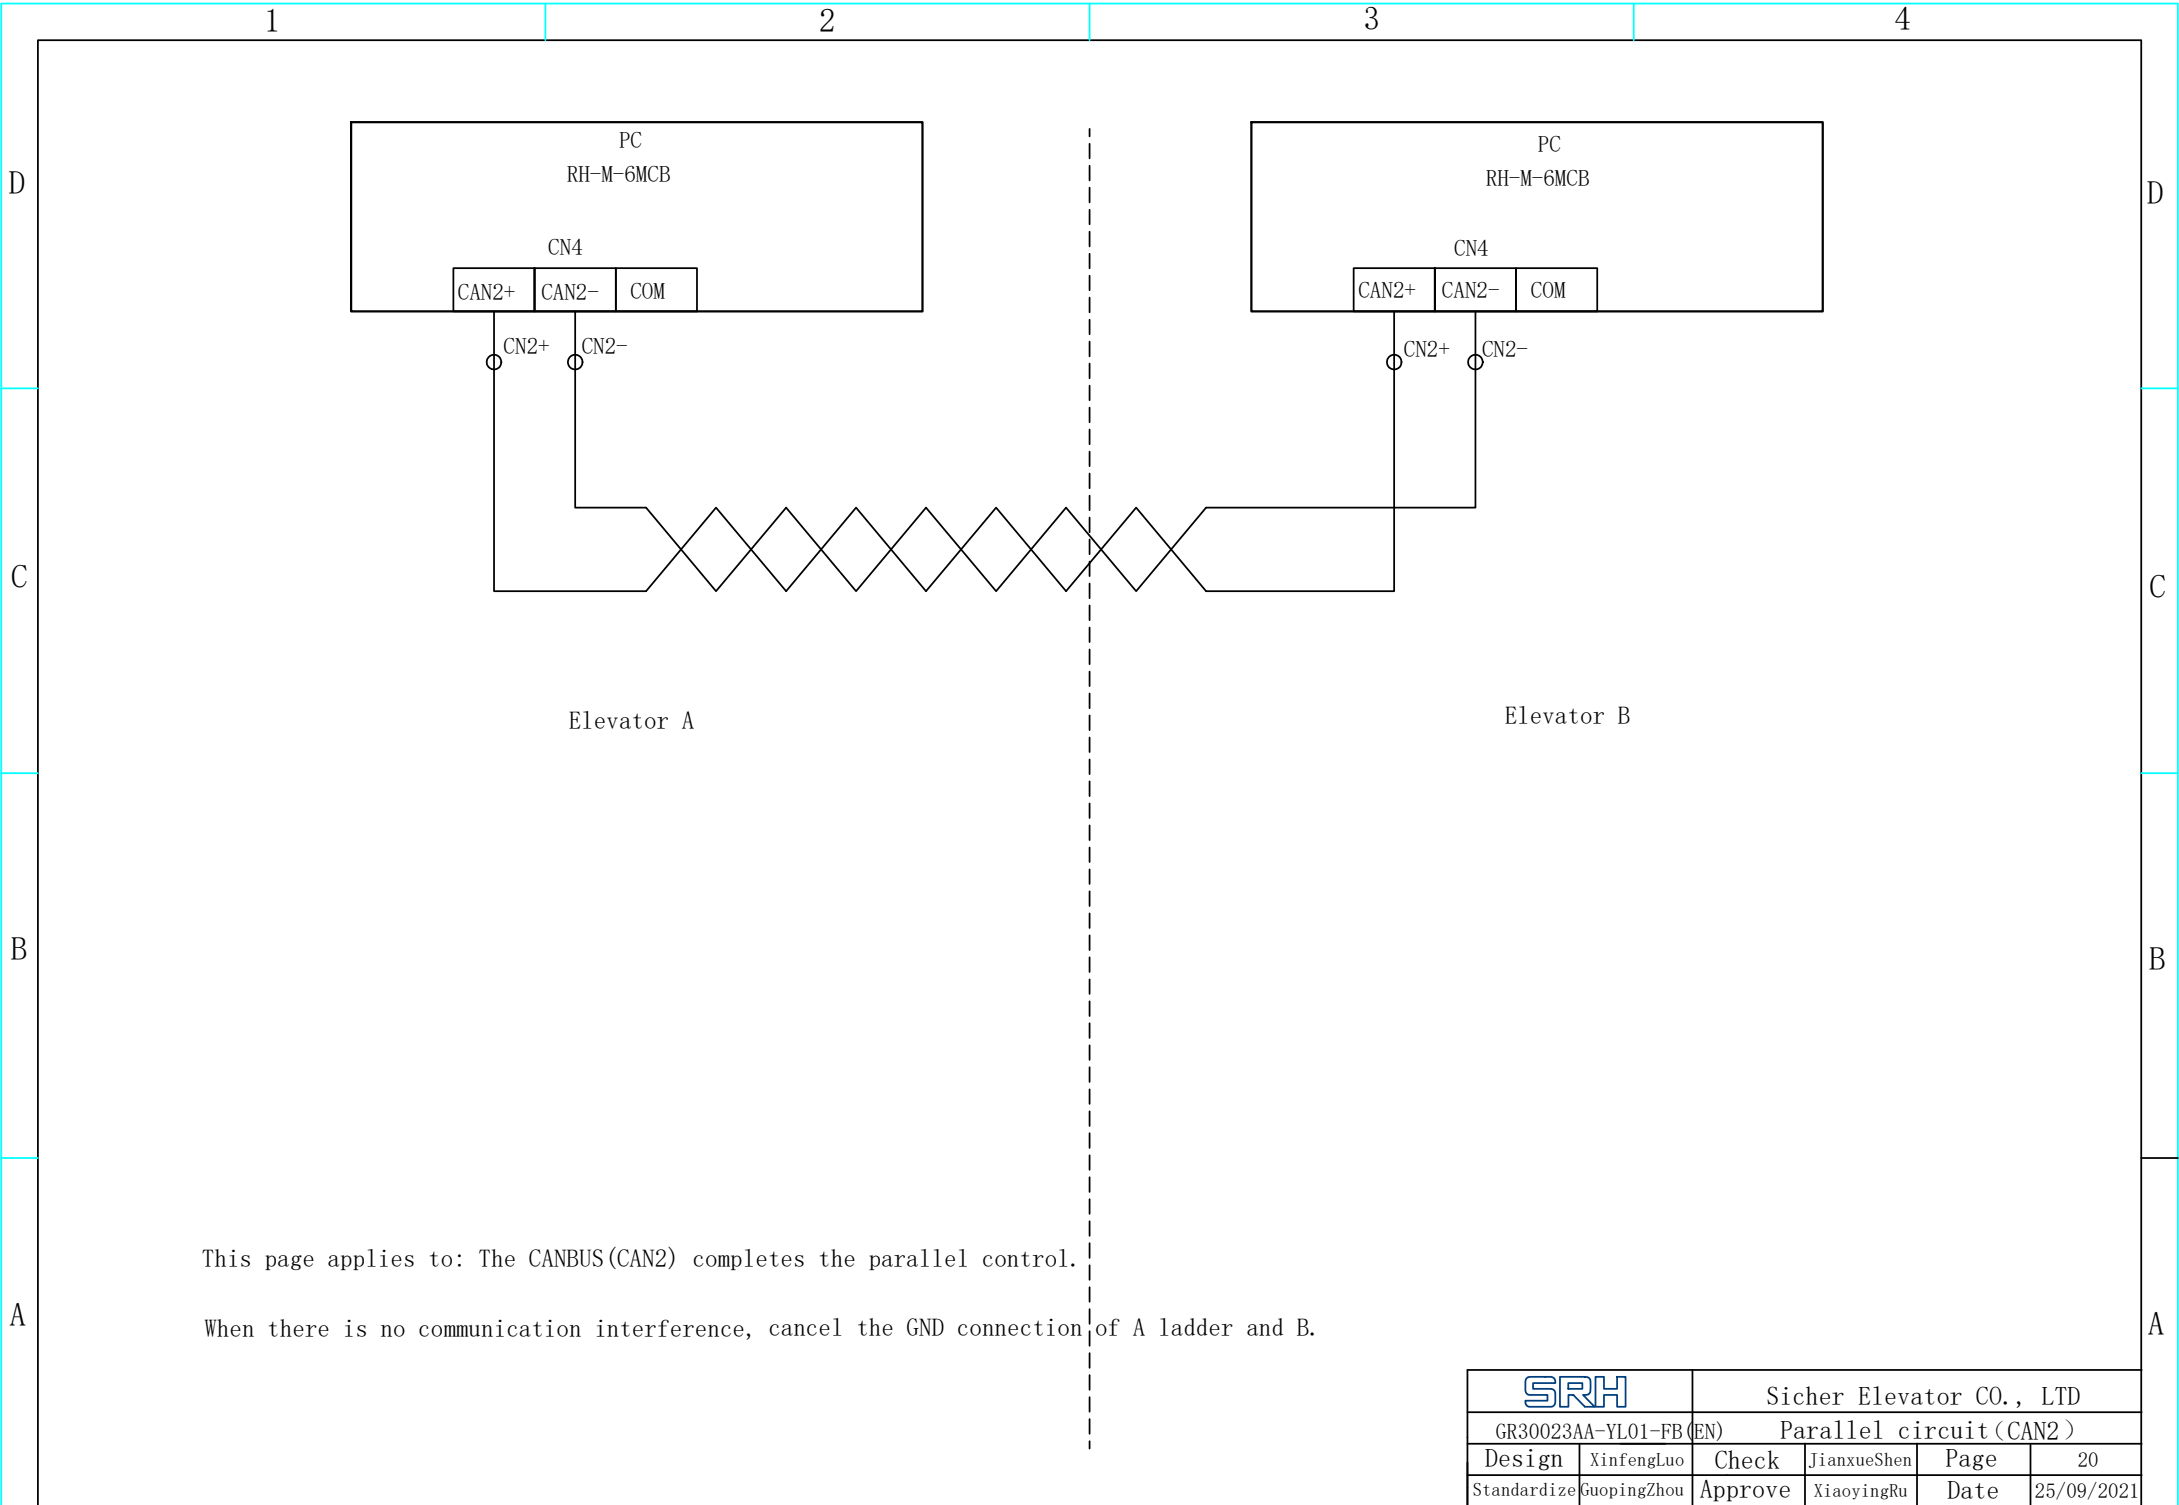

D

C

B

A

D

C

B

A

1

2

3




4

1




2

3

4

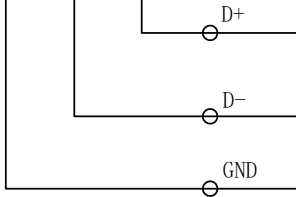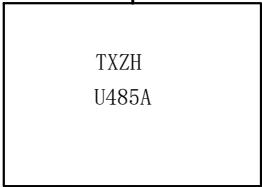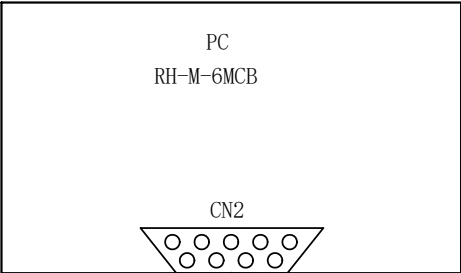

Elevator A

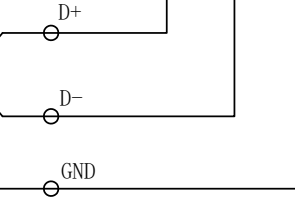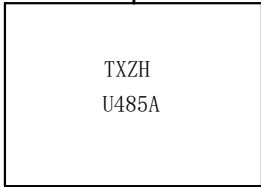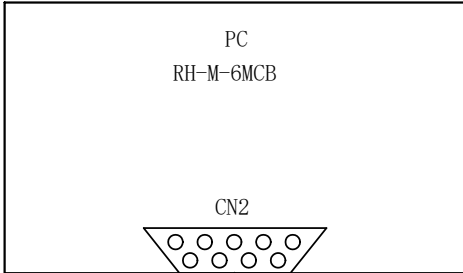

Elevator B

This page applies to: The 232-485 completes the parallel control.

SRH		Sicher Elevator CO., LTD			
GR30023AA-YL01-FB (EN)		Parallel circuit (232-485)			
Design	XinfengLuo	Check	JianxueShen	Page	20A
Standardize	GuopingZhou	Approve	XiaoyingRu	Date	25/09/2021

D

C

B


A

D

C

B


A

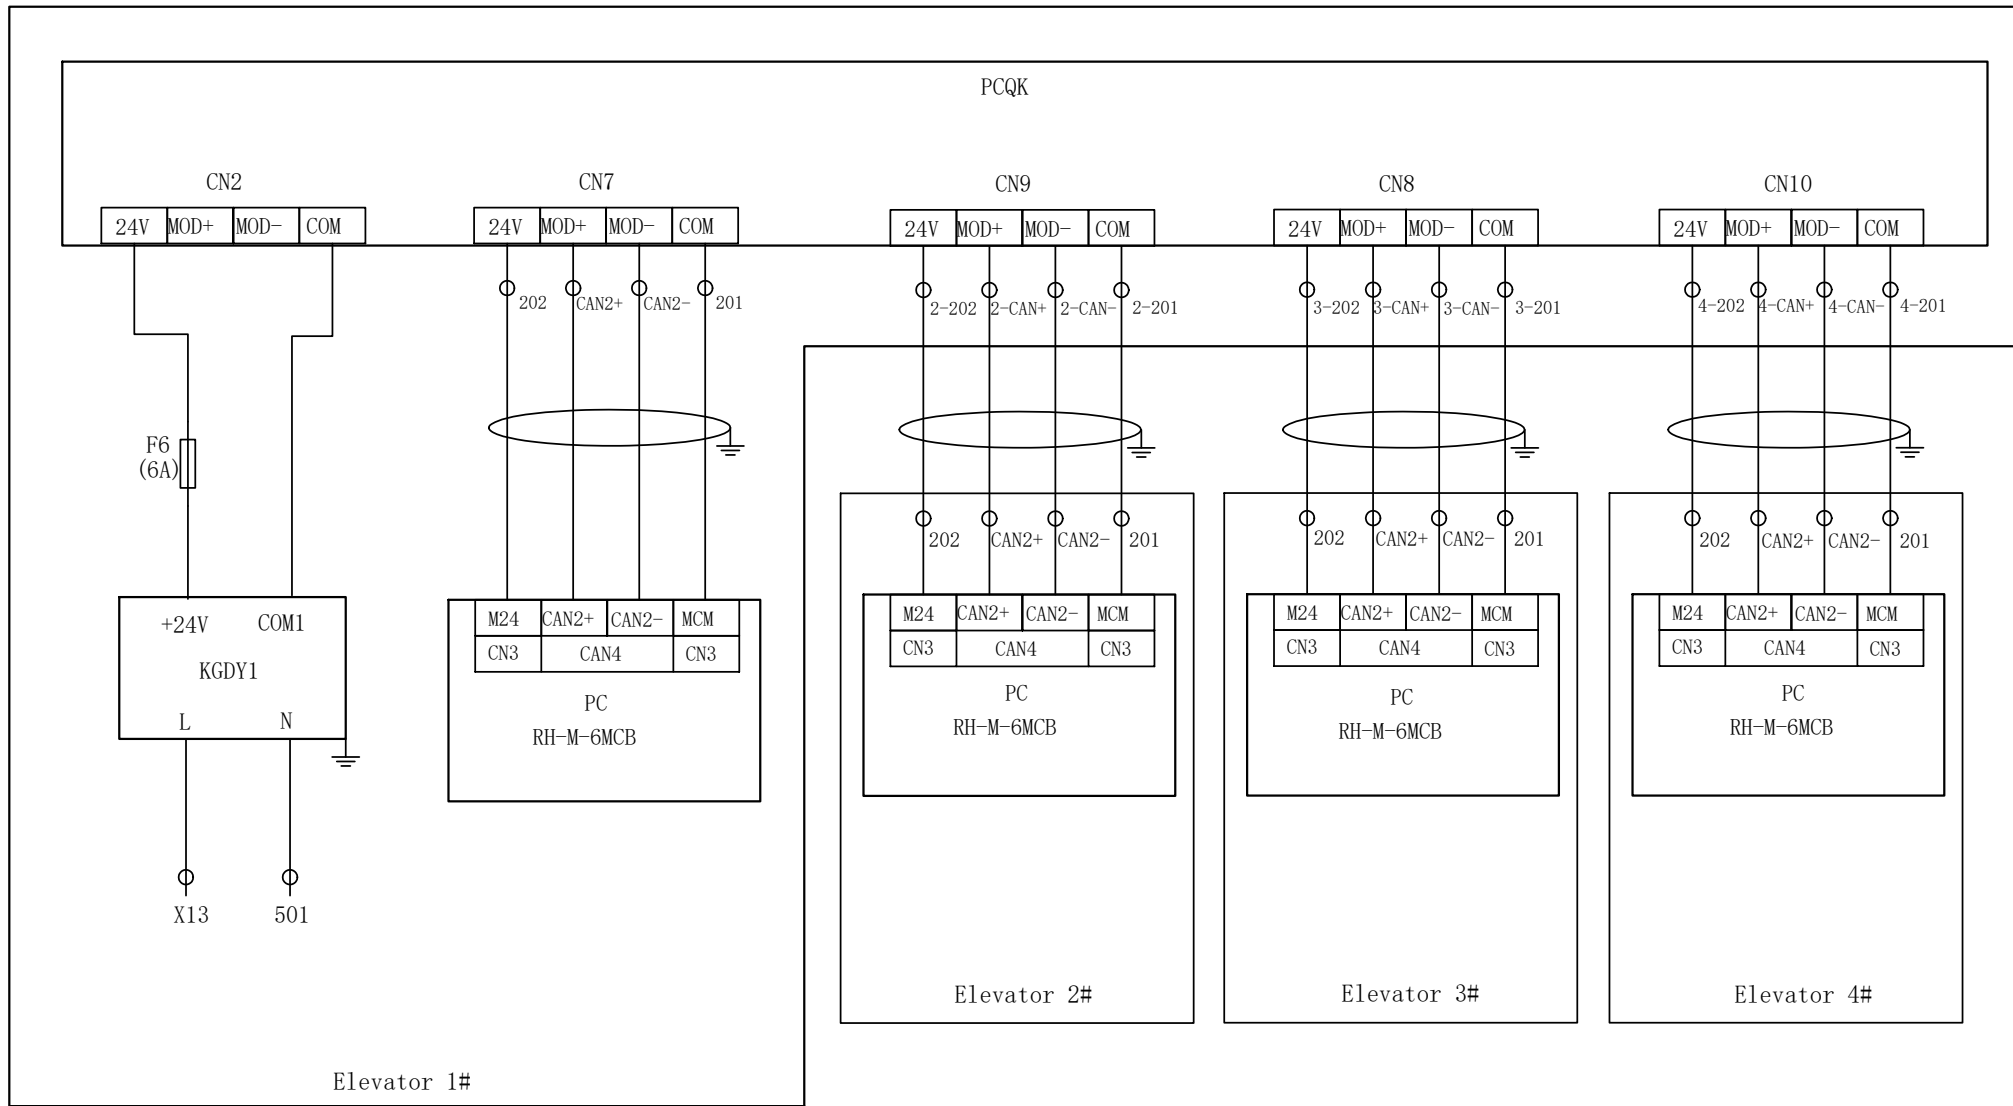



Note: 1, This page applies to supporting group control of a maximum of 4 elevators.


2, The communication line was made of two pairs of twisted pair wire, 202 / 201 twisted pair wire, CAN + / CAN- twisted pair wire.


SRH		Sicher Elevator CO., LTD			
GR30023AA-YL01-FB (EN)		Group control circuit			
Design	XinfengLuo	Check	JianxueShen	Page	21
Standardize	GuopingZhou	Approve	XiaoyingRu	Date	25/09/2021

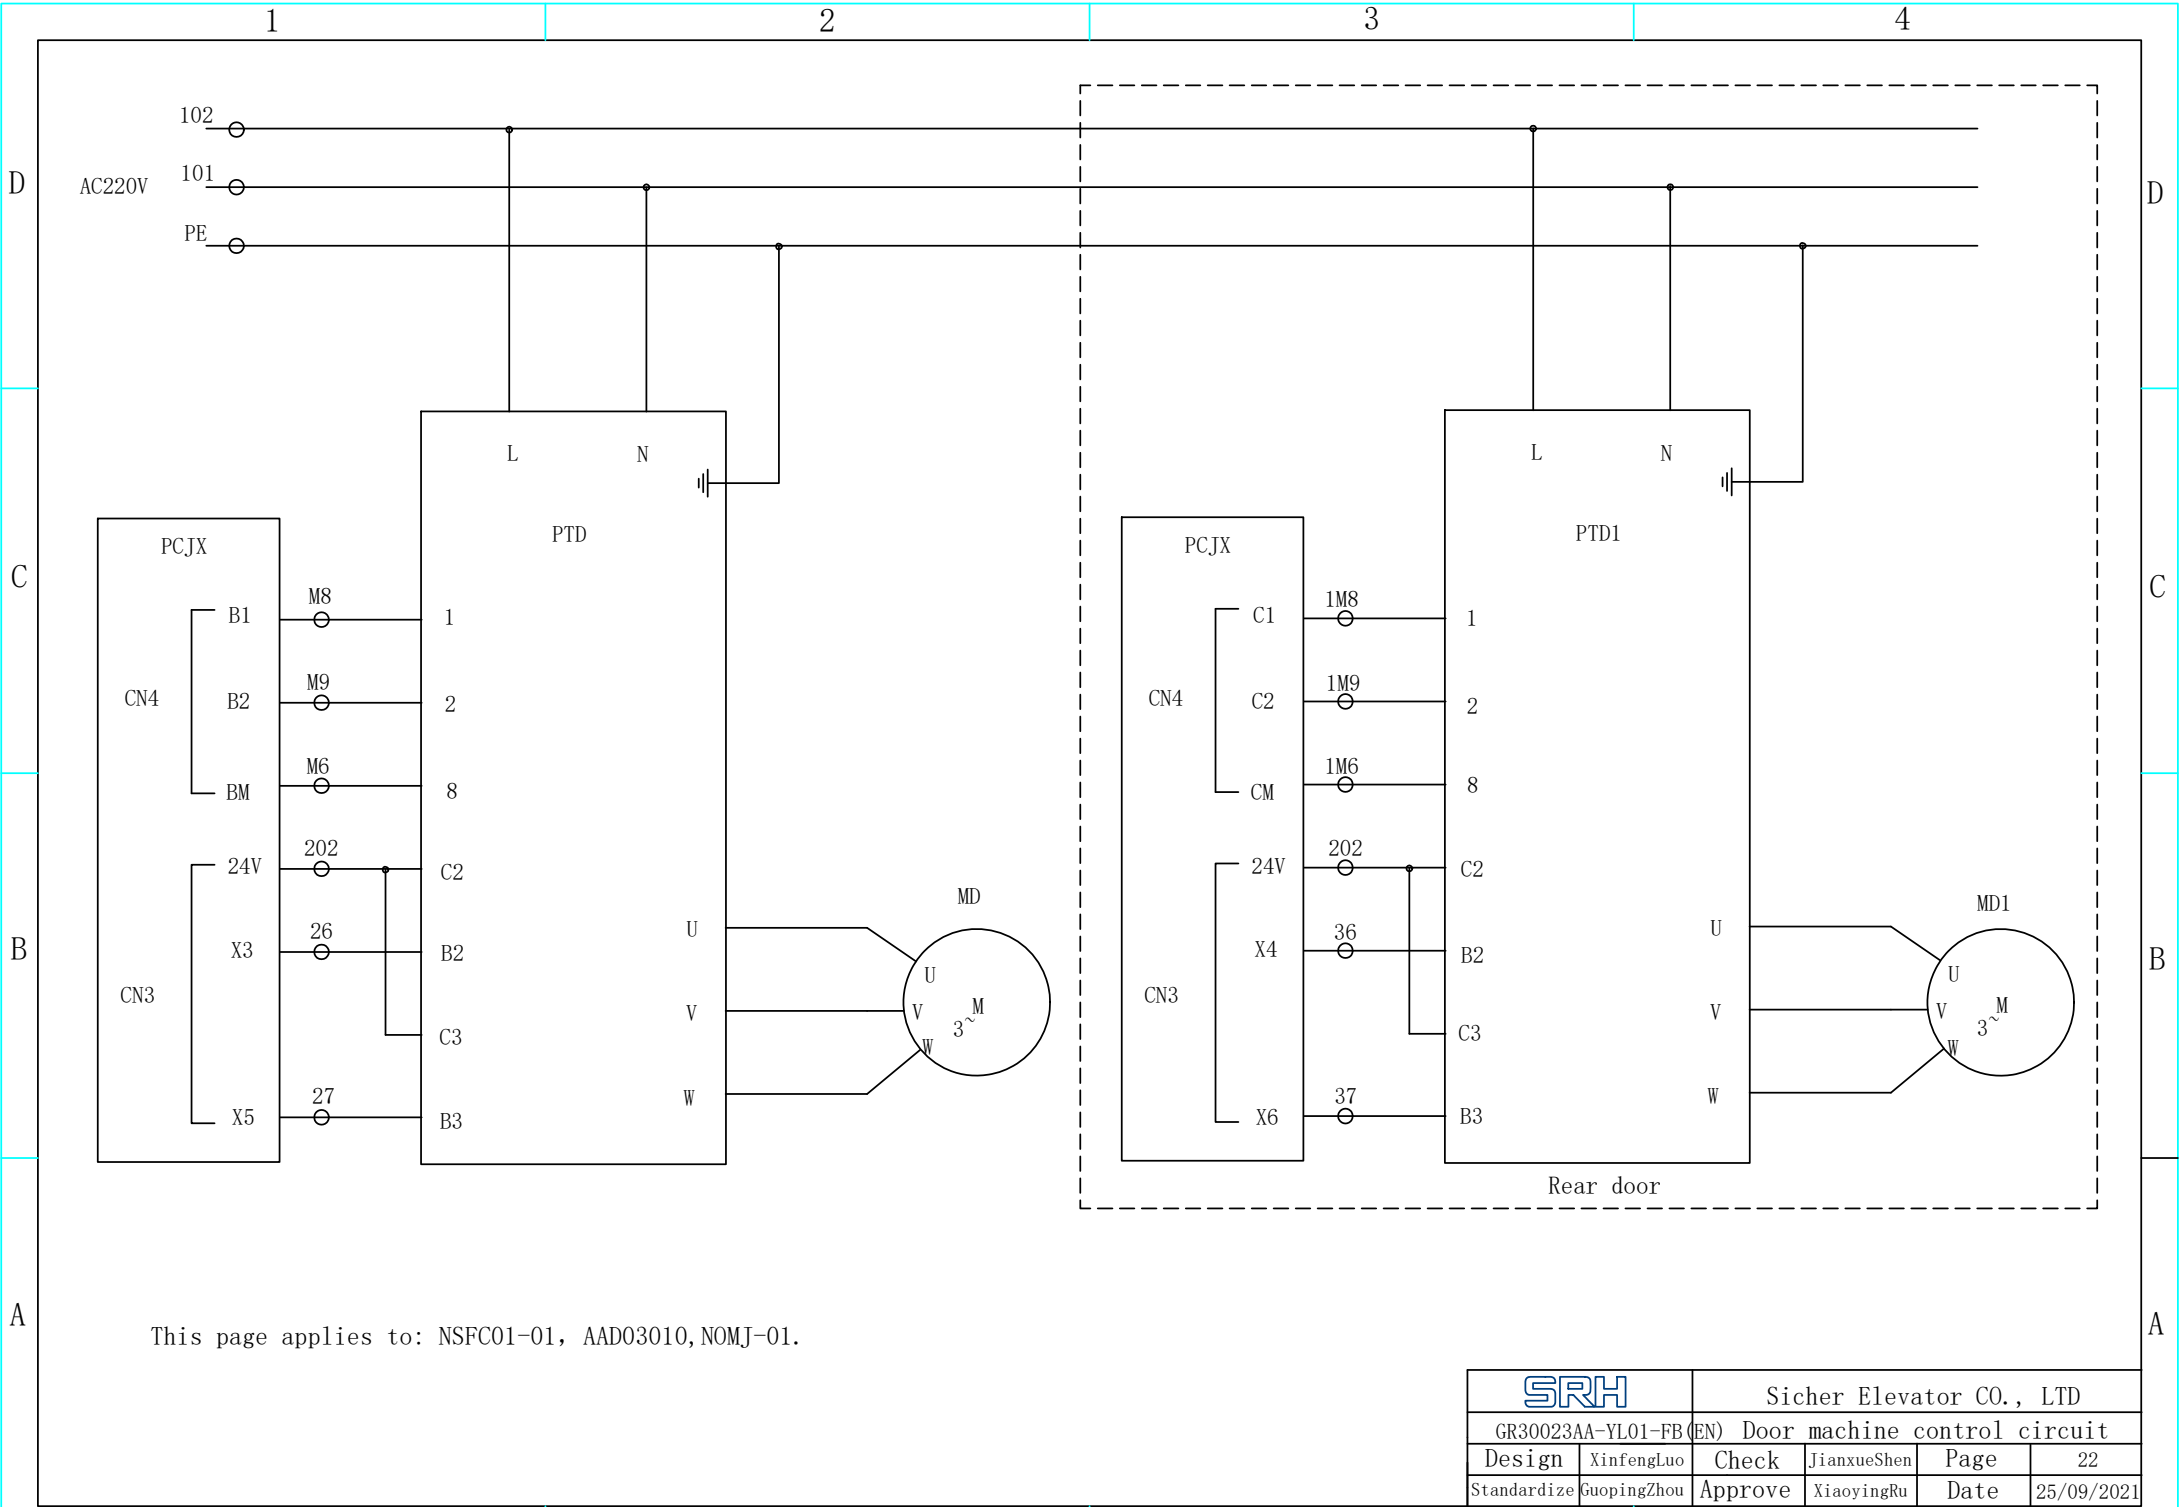

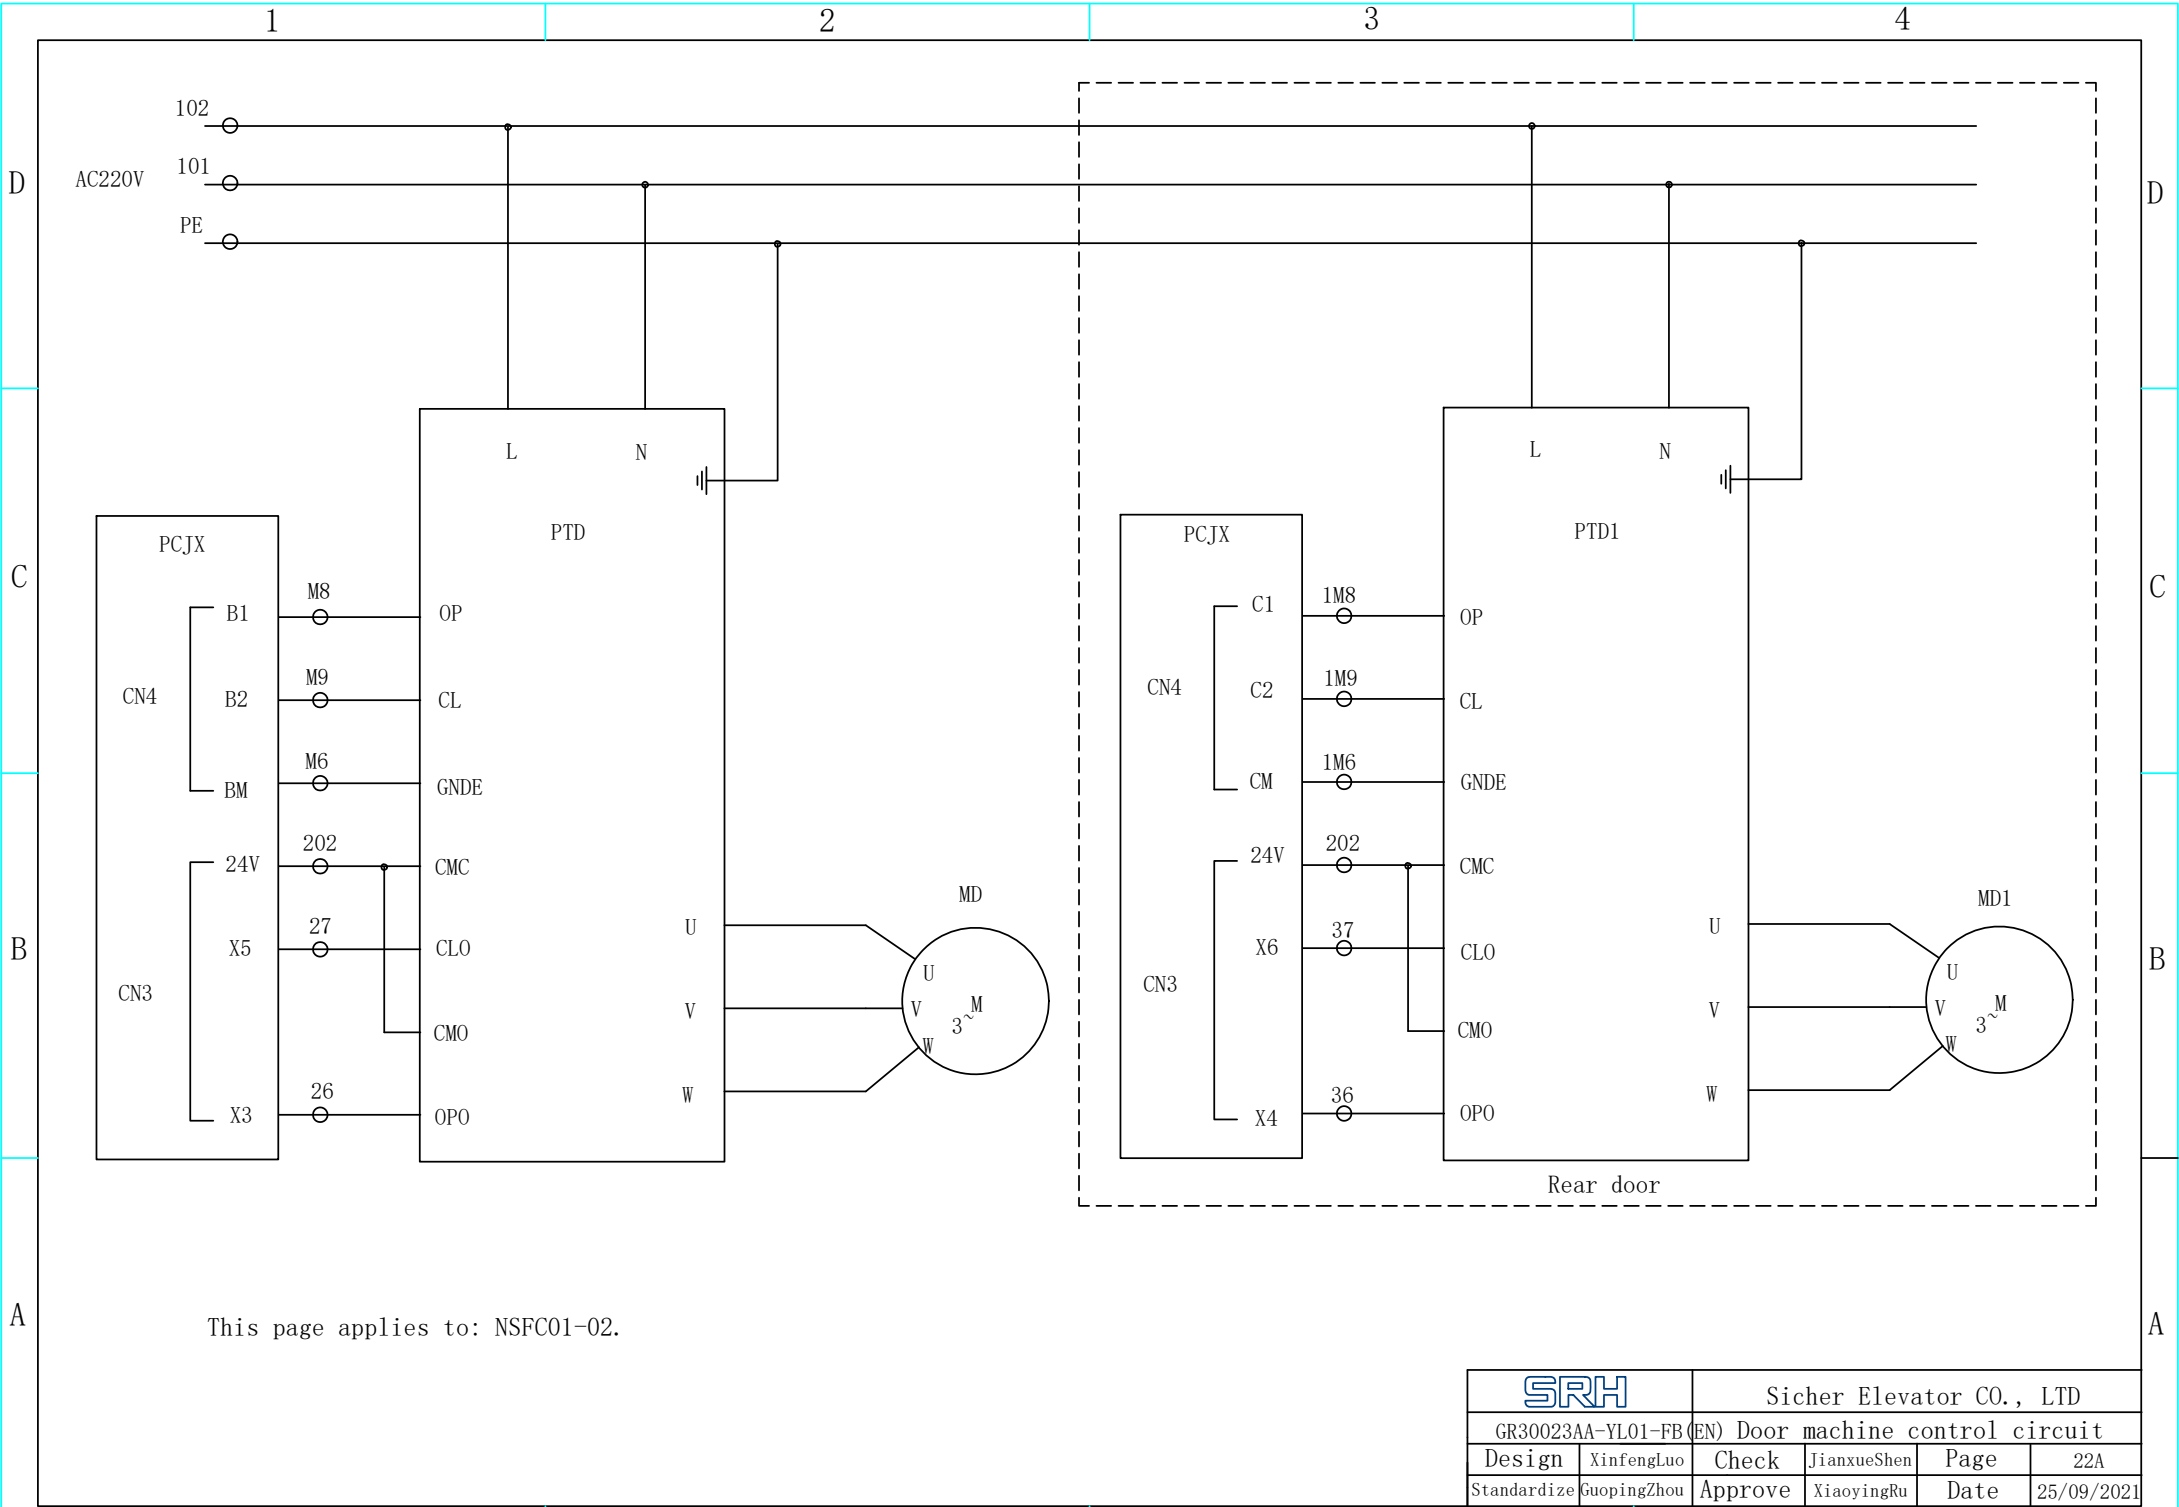

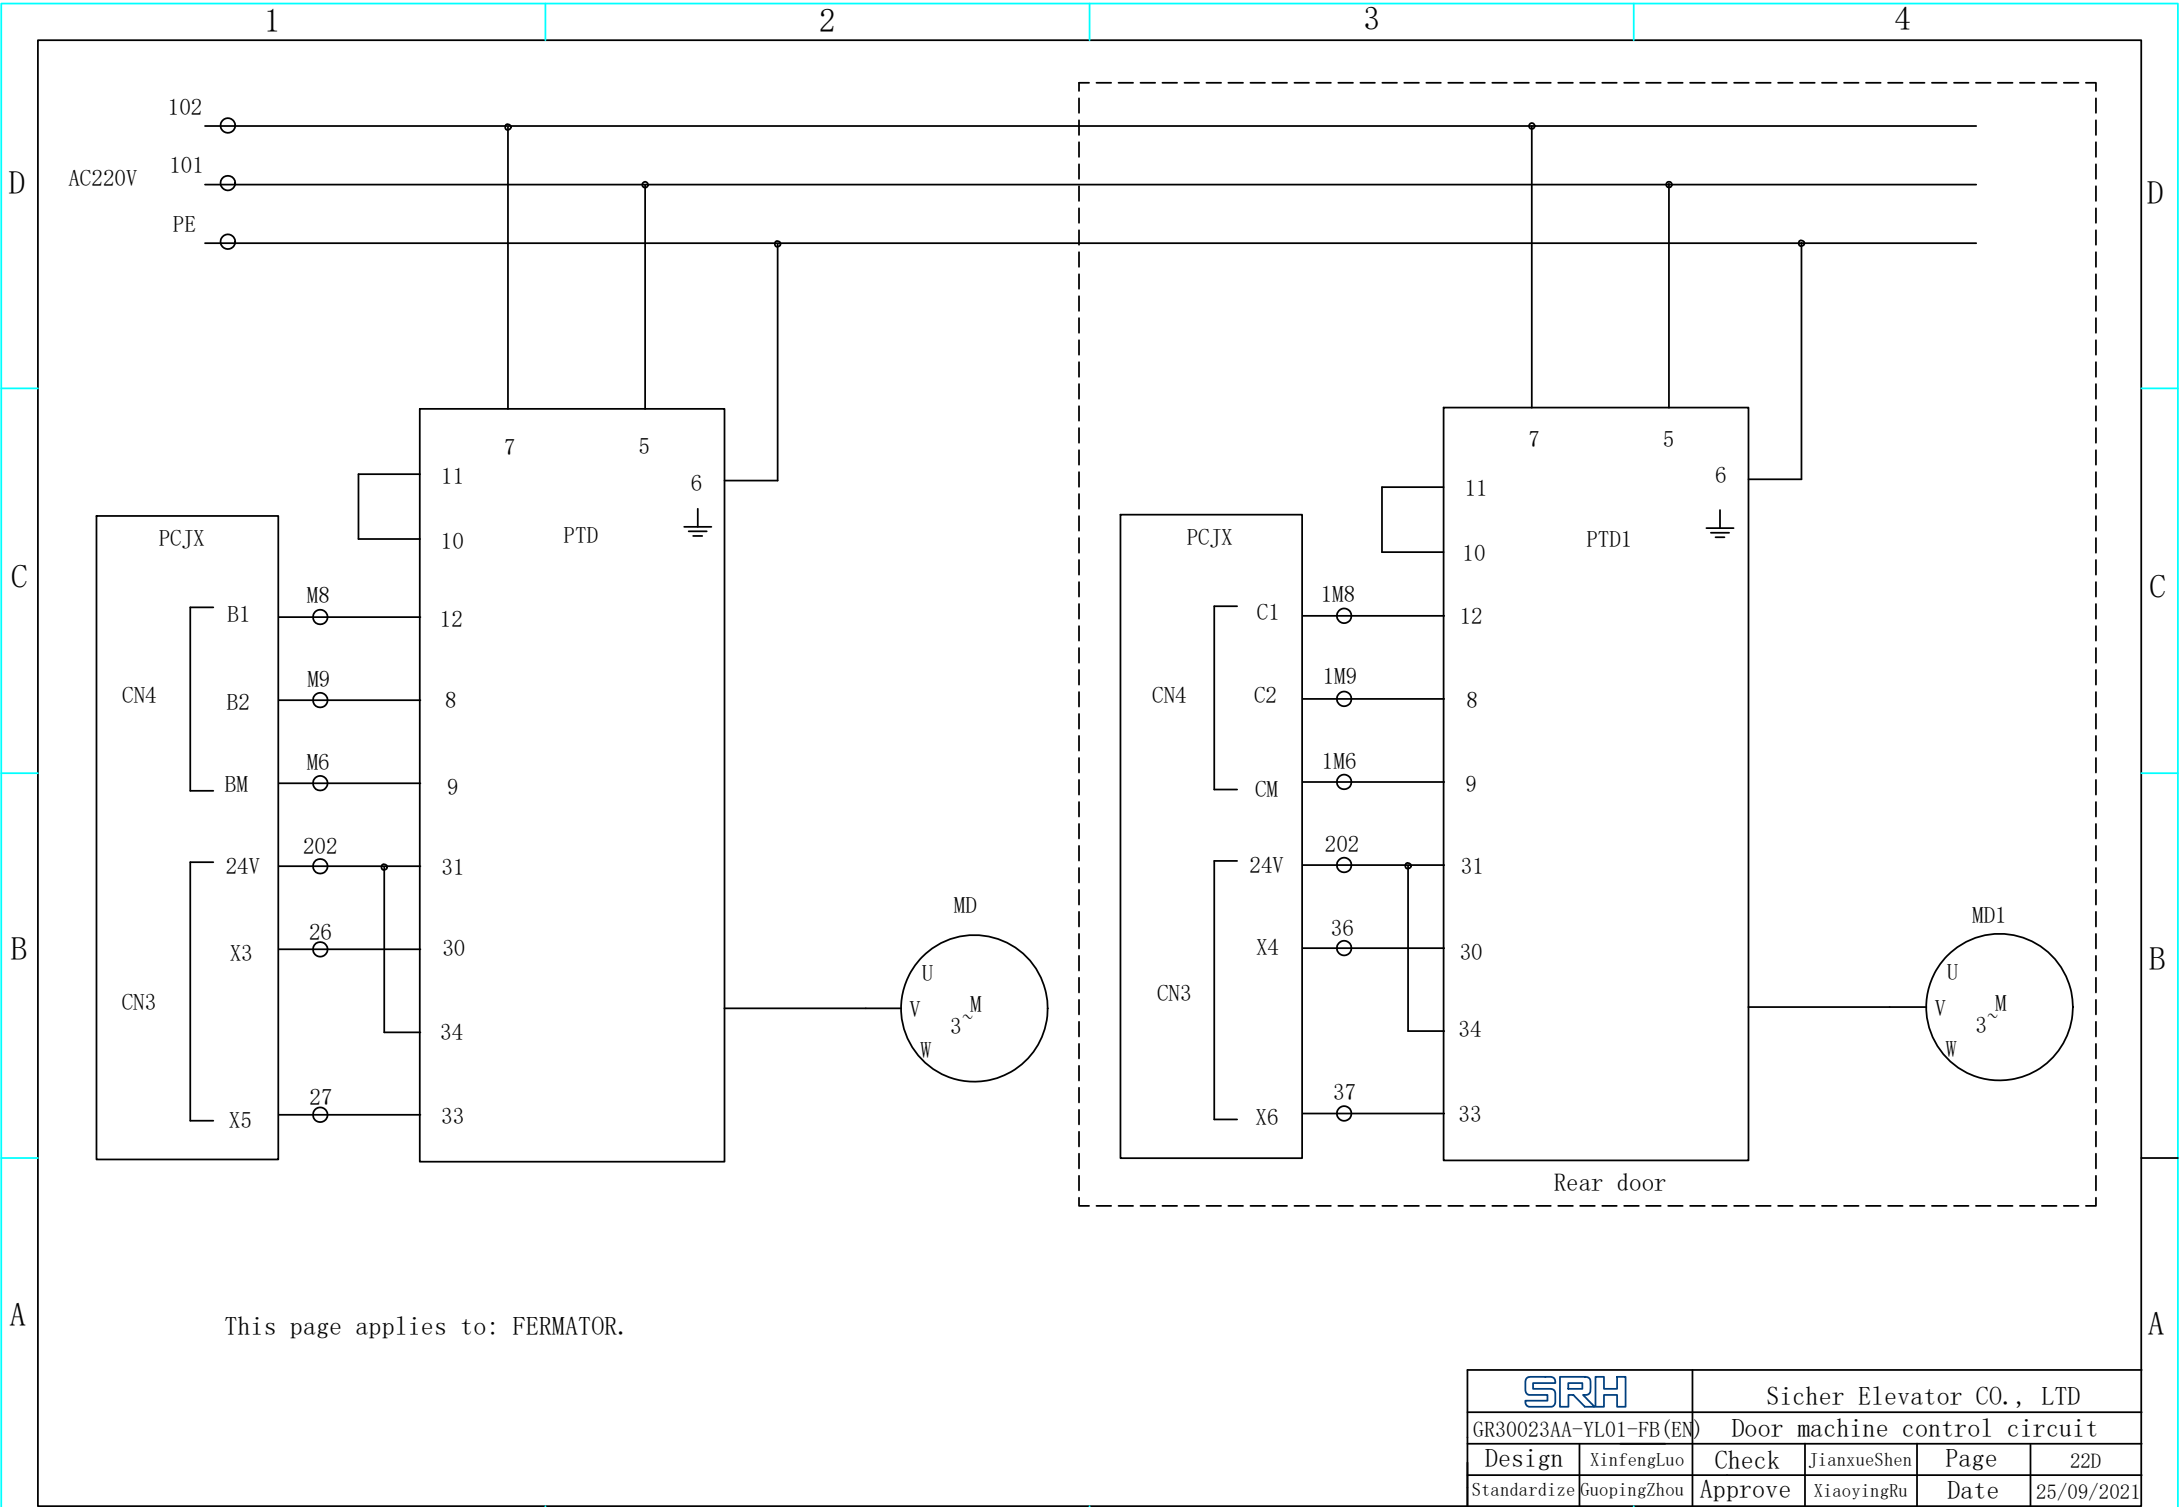

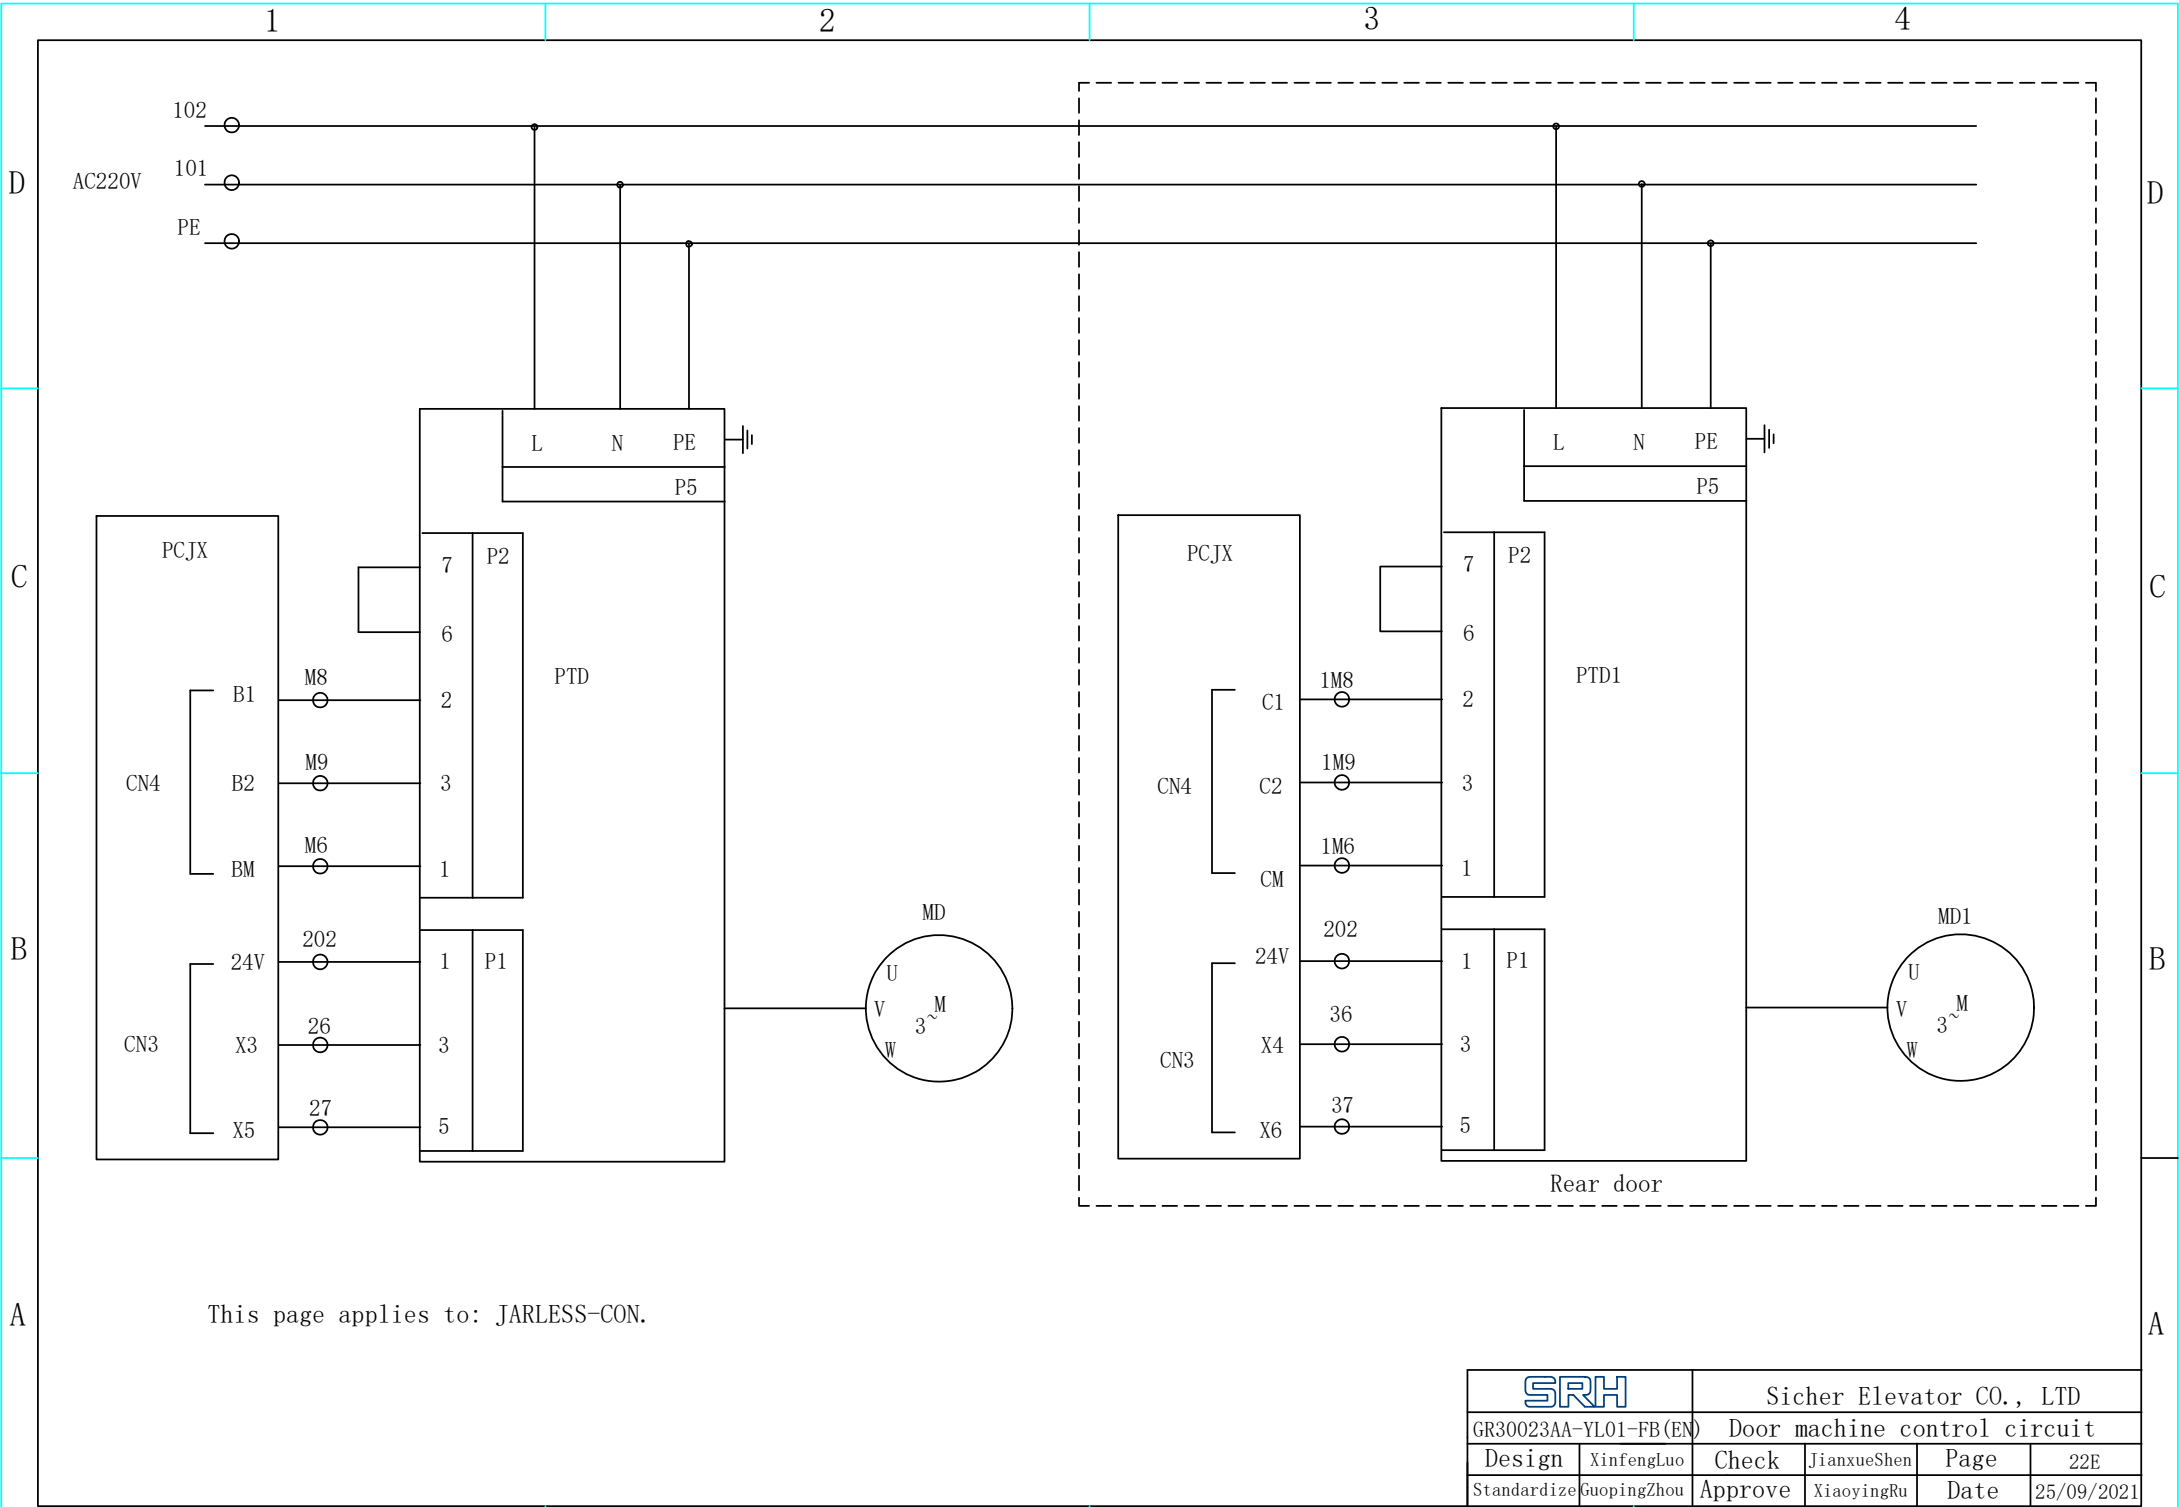

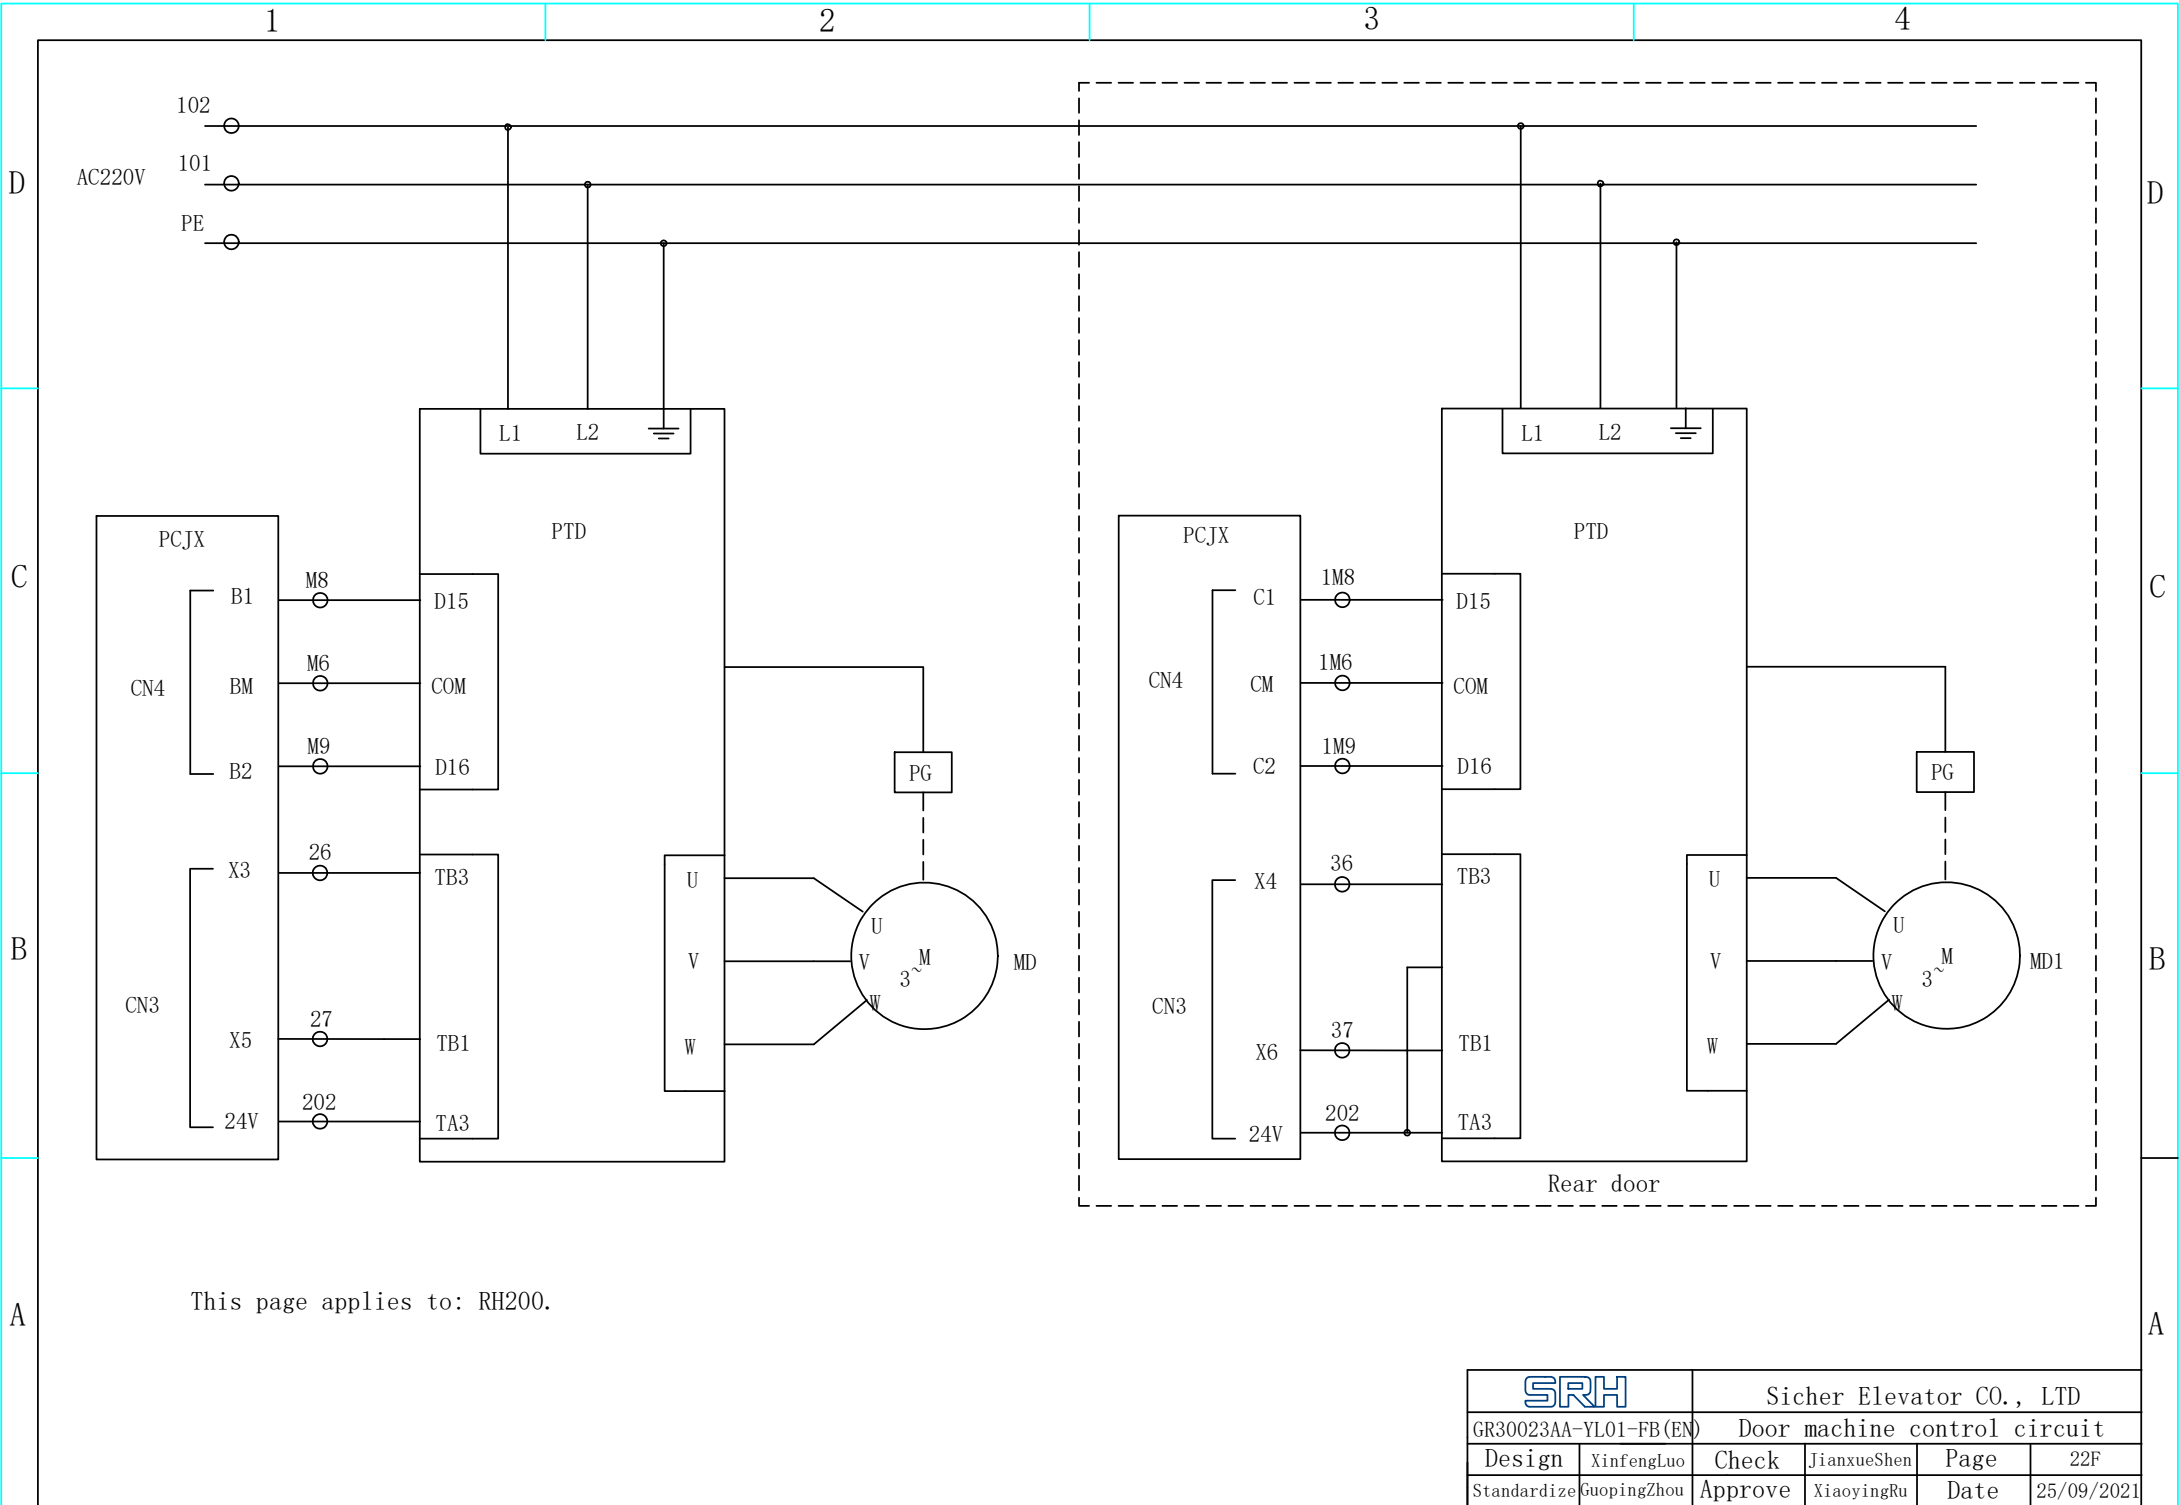

D

C

B


A

D


C

B


A

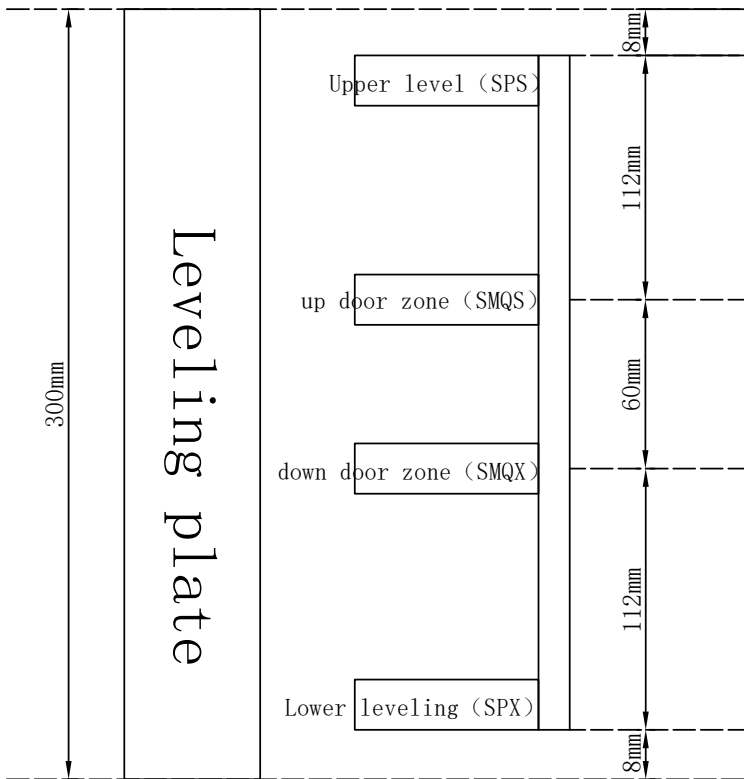


Installation of leveling switches

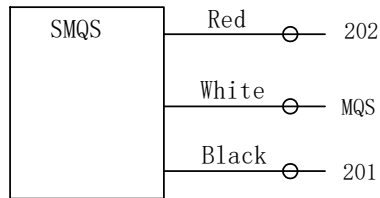


Leveling switches type: SGD31-GG-TZ2B2

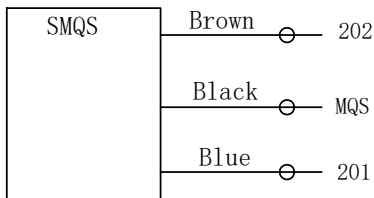

Leveling switches type: HLES-M1

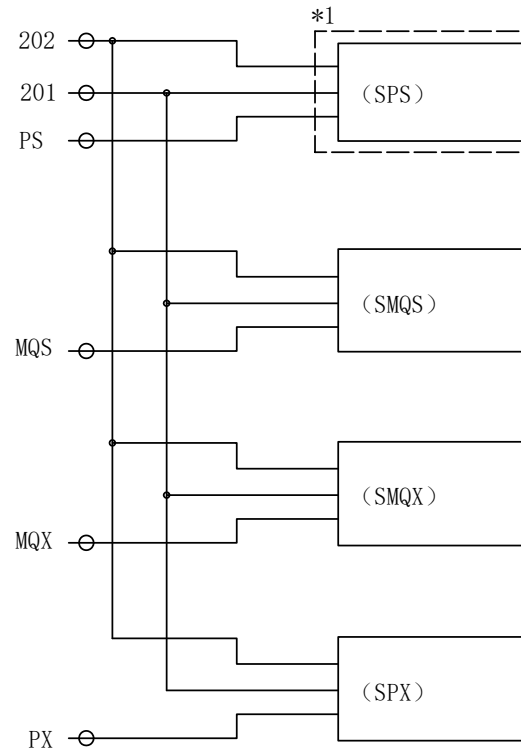

SRH		Sicher Elevator CO., LTD			
GR30023AA-YL01-FB(EN)		Installation and wiring diagram of leveling switches			
Design	XinfengLuo	Check	JianxueShen	Page	23
Standardize	GuopingZhou	Approve	XiaoyingRu	Date	25/09/2021

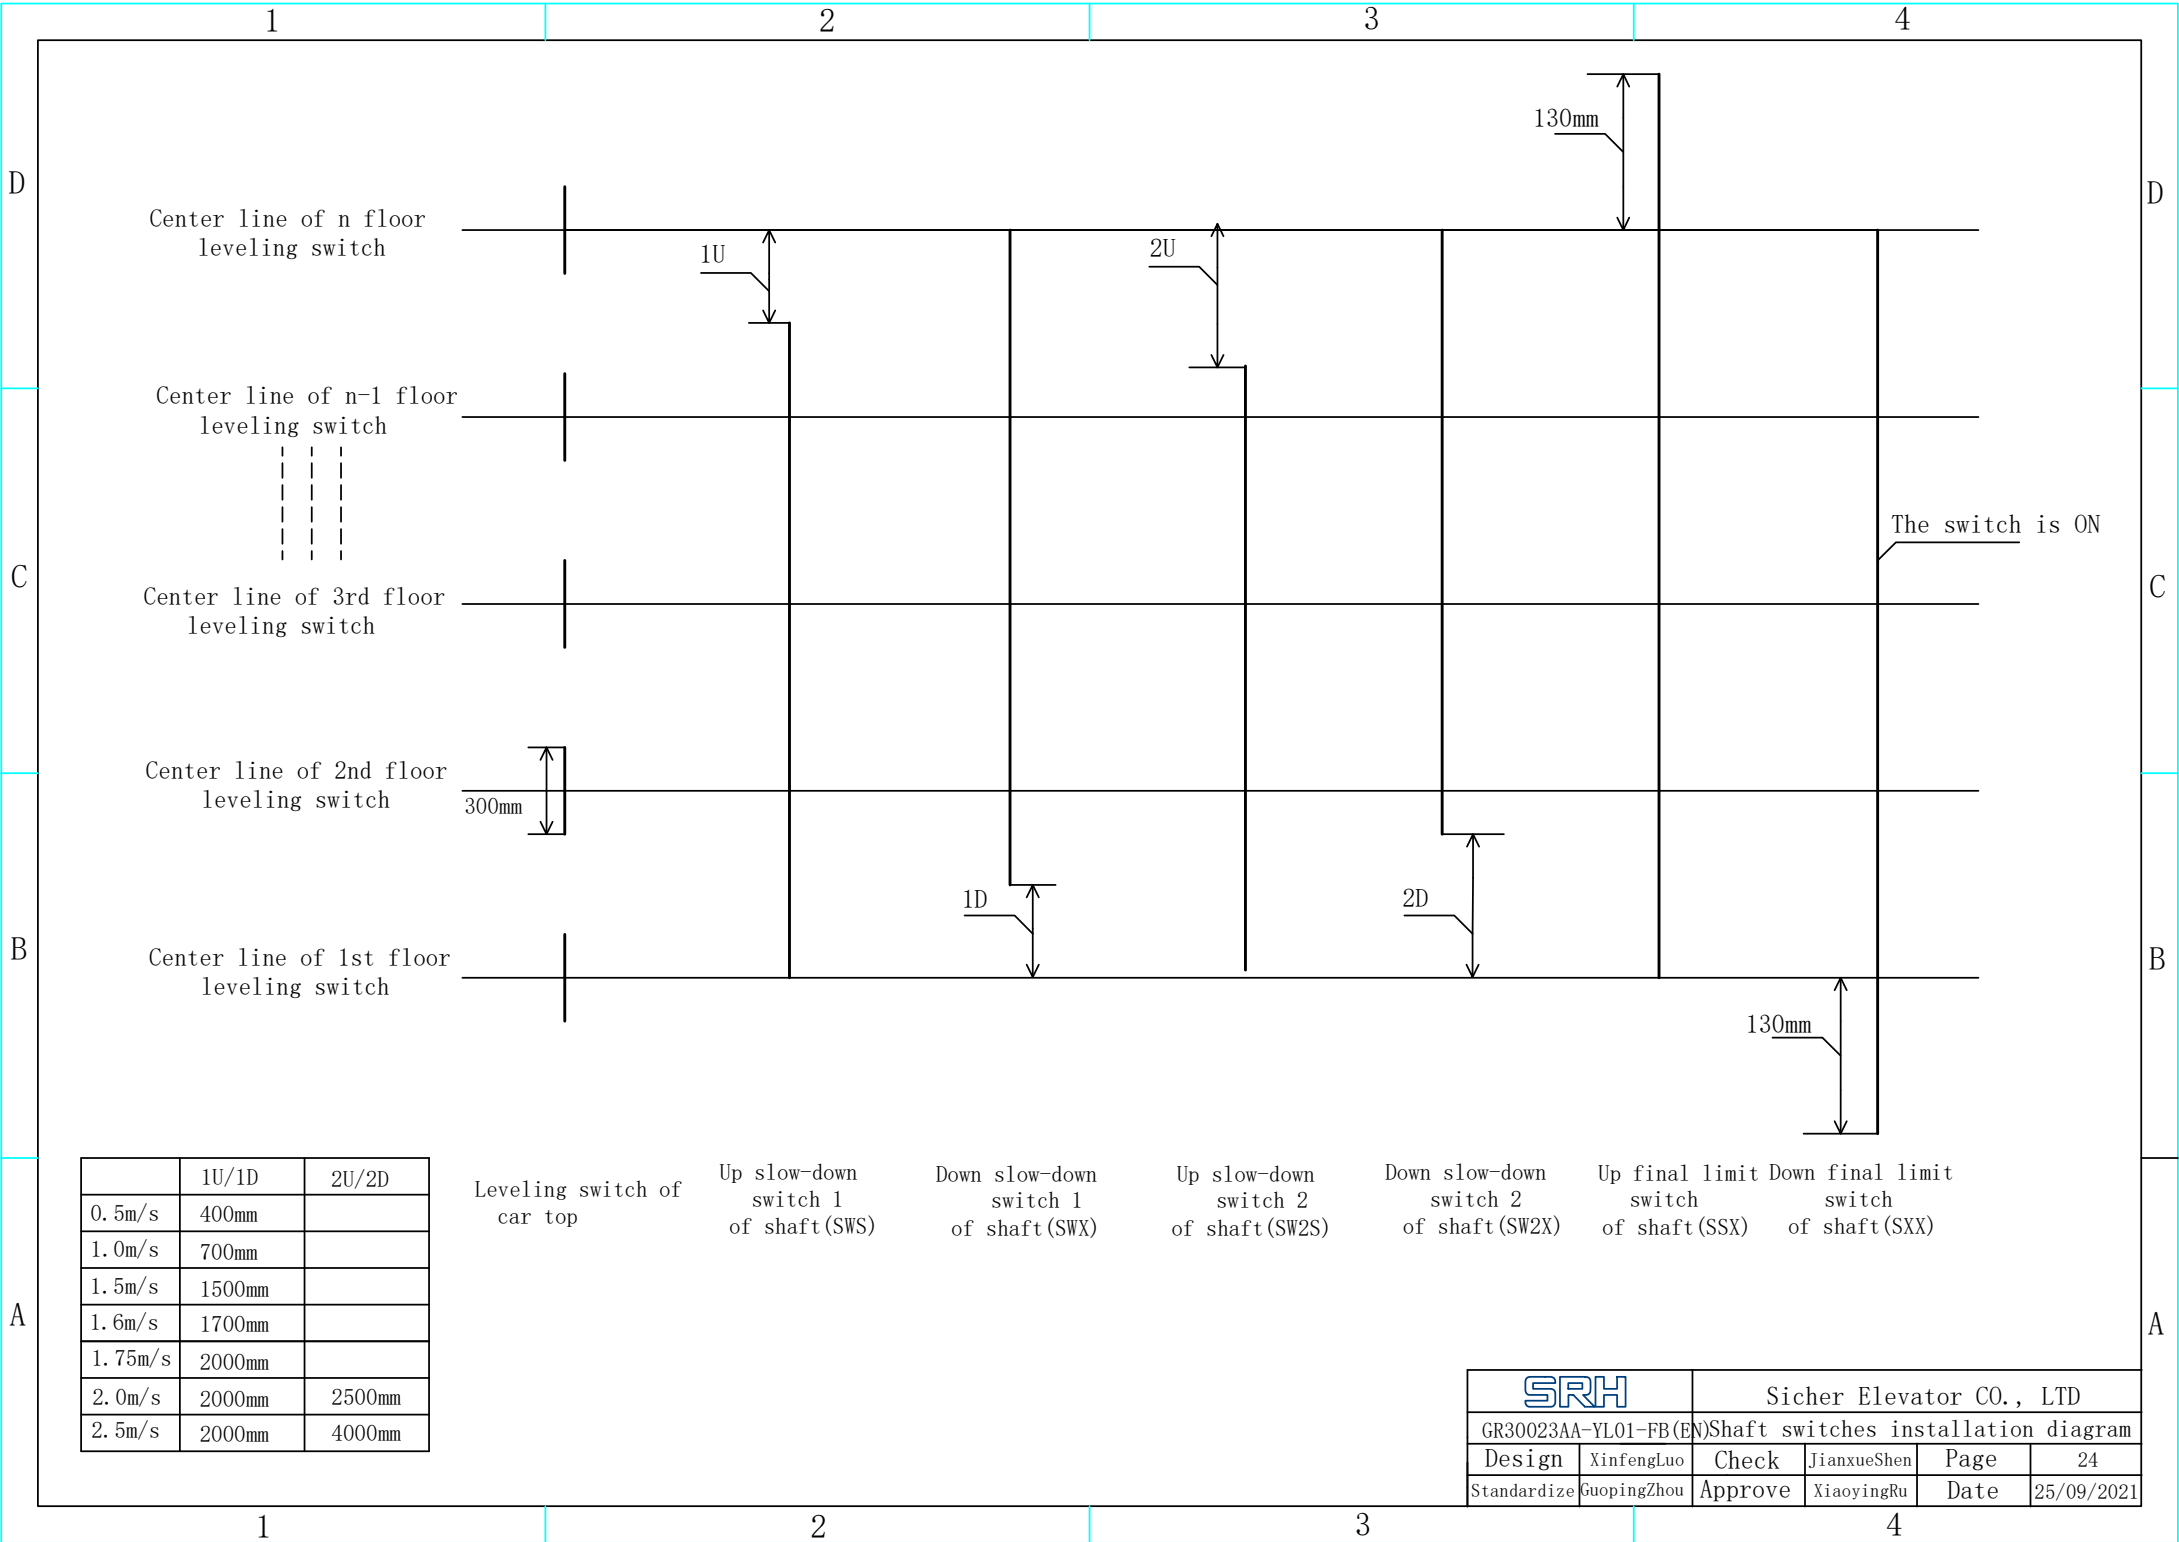

D

C

B


A

D

C

B

A

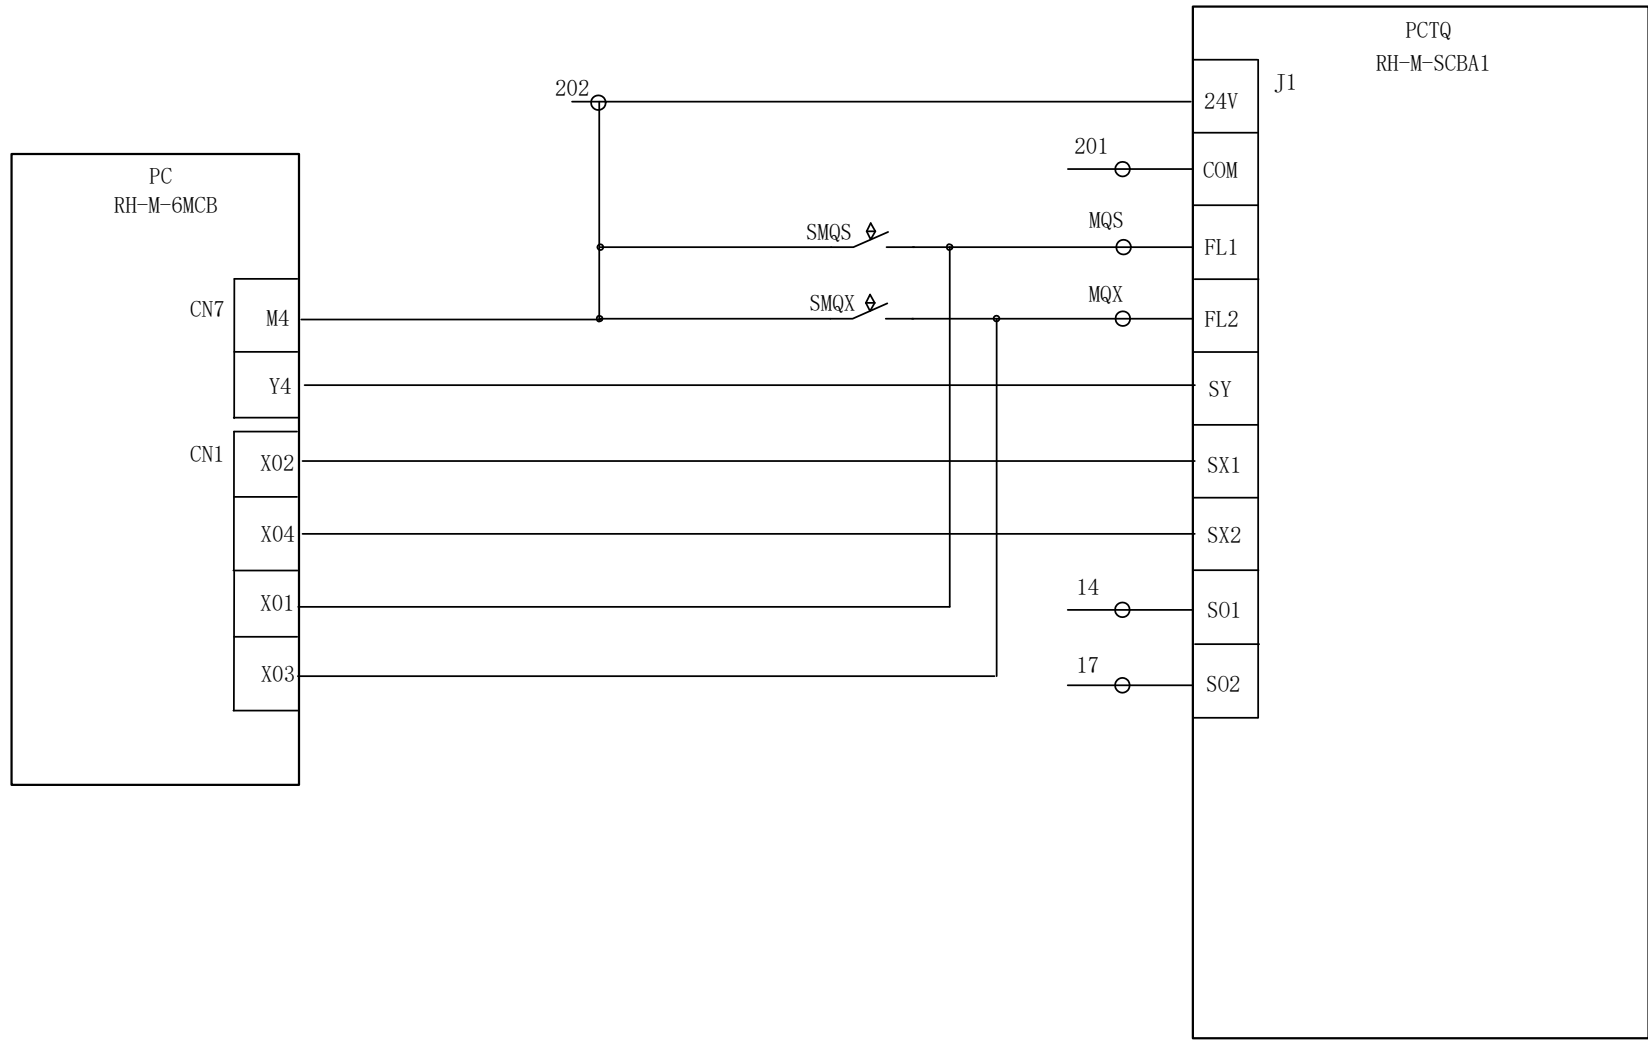

SRH		Sicher Elevator CO., LTD			
GR30023AA-YL01-FB(EN)		UCMP diagram(Single door)			
Design	XinfengLuo	Check	JianxueShen	Page	25
Standardize	GuopingZhou	Approve	XiaoyingRu	Date	25/09/2021

D

C

B


A

D

C

B

A

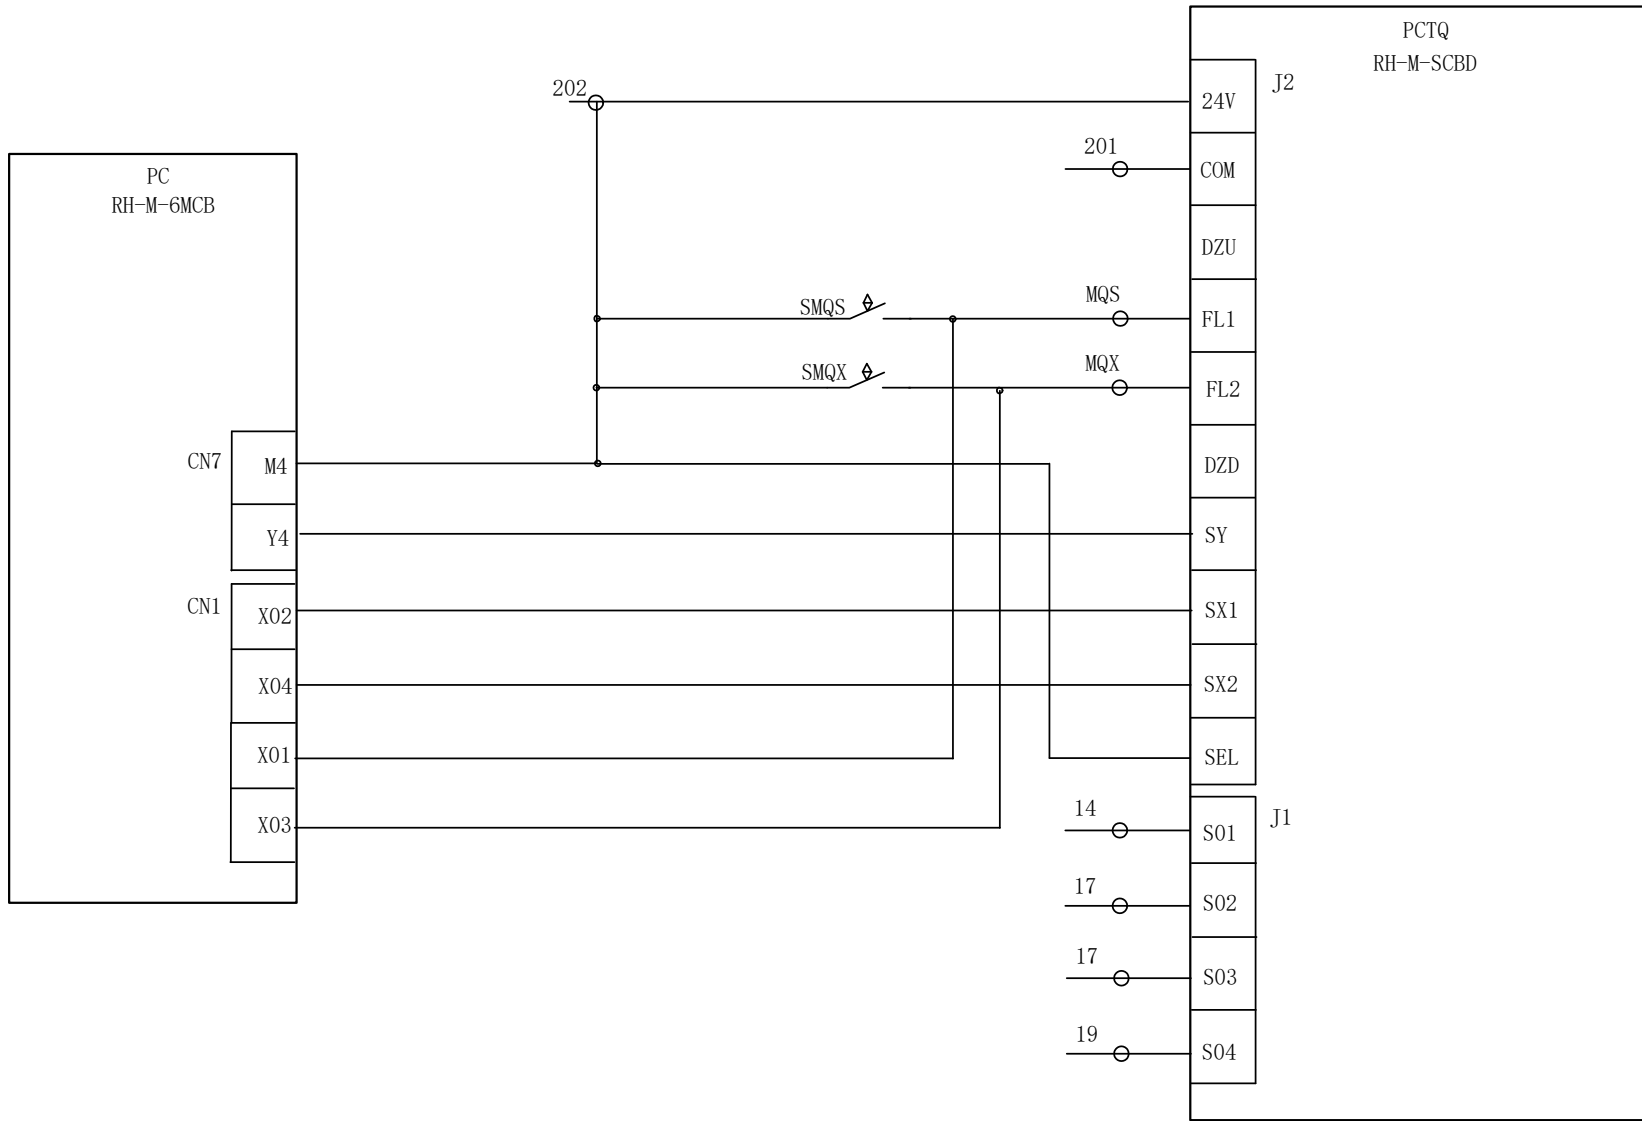

SRH		Sicher Elevator CO., LTD			
GR30023AA-YL01-FB(EN)		UCMP diagram(Double door)			
Design	XinfengLuo	Check	JianxueShen	Page	25A
Standardize	GuopingZhou	Approve	XiaoyingRu	Date	25/09/2021

D

C

B

A


D

C


B

A

a

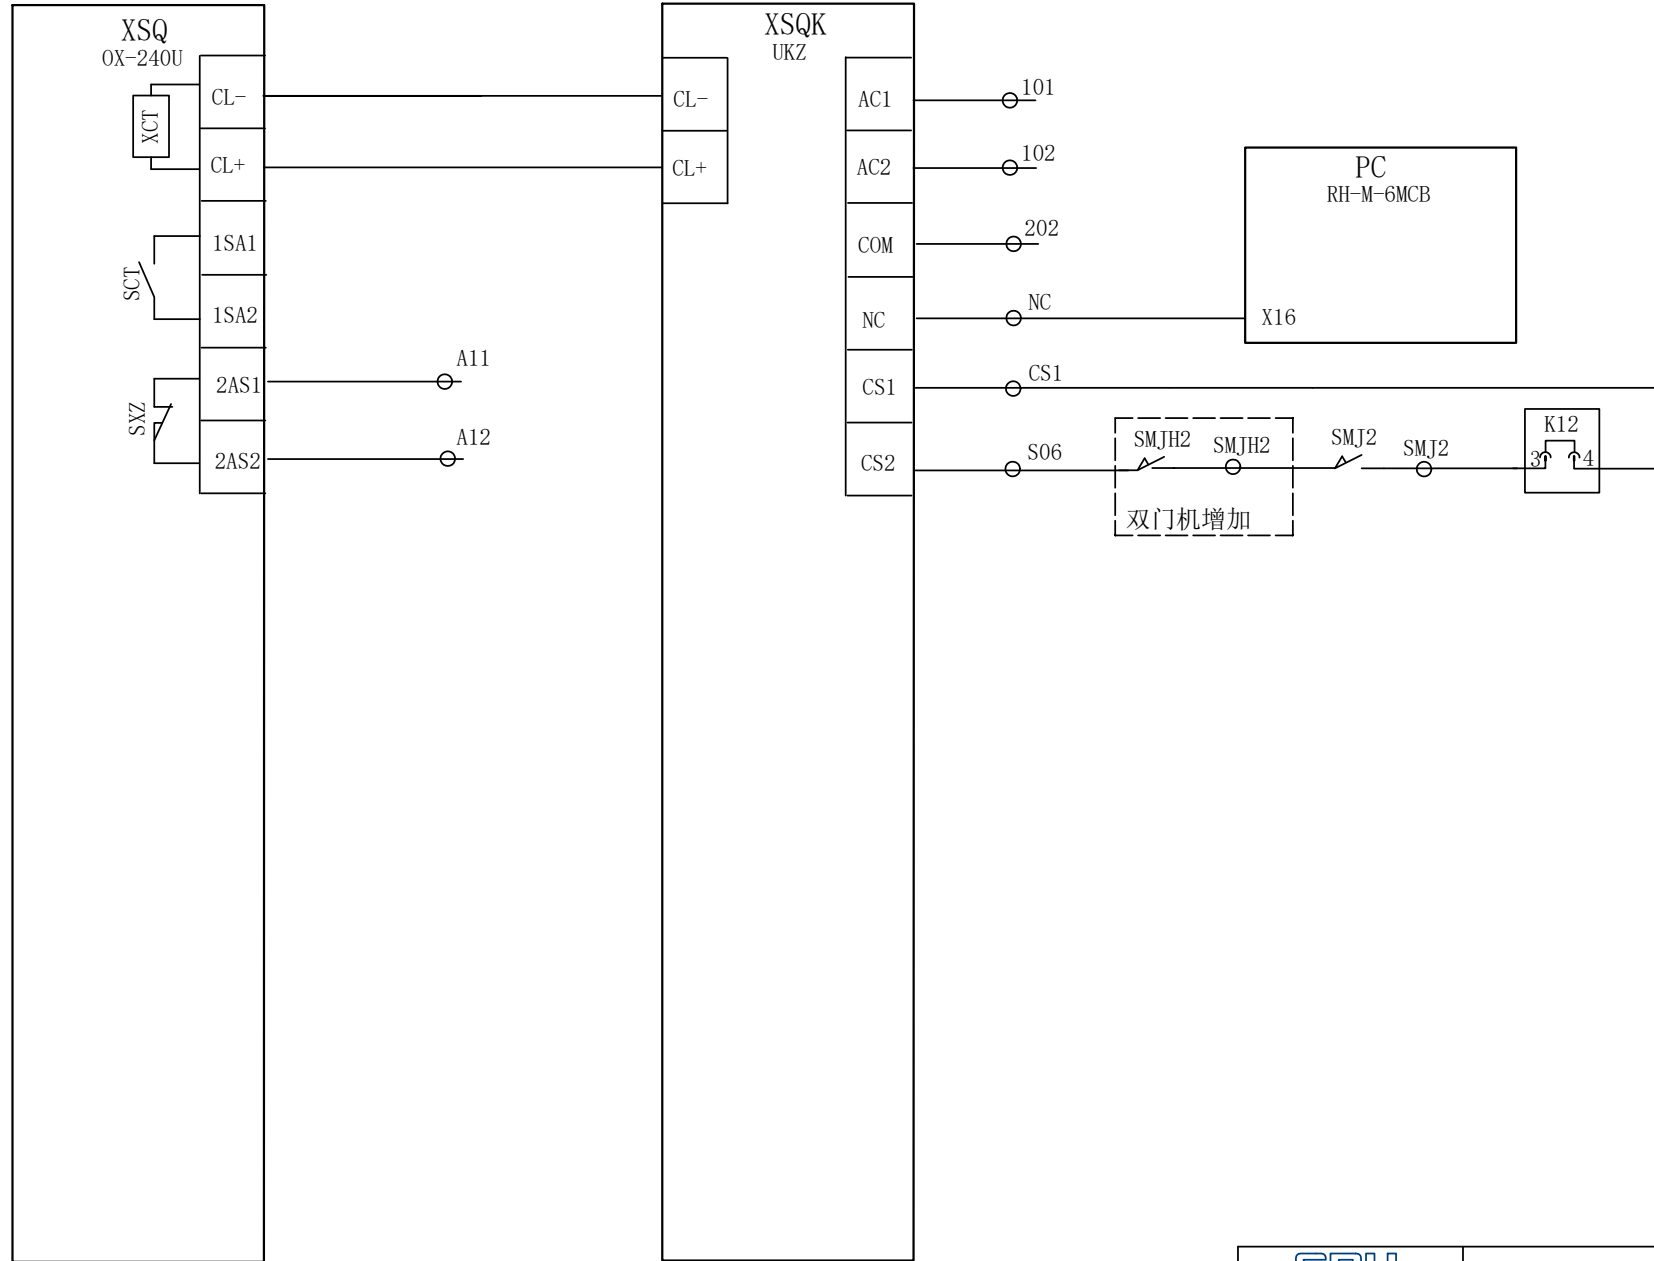

SRH		Sicher Elevator CO., LTD			
GR30023AA-YL01-FB(EN)		UCMP diagram(asynchronous)			
Design	XinfengLuo	Check	JianxueShen	Page	25B
Standardize	GuopingZhou	Approve	XiaoyingRu	Date	25/09/2021

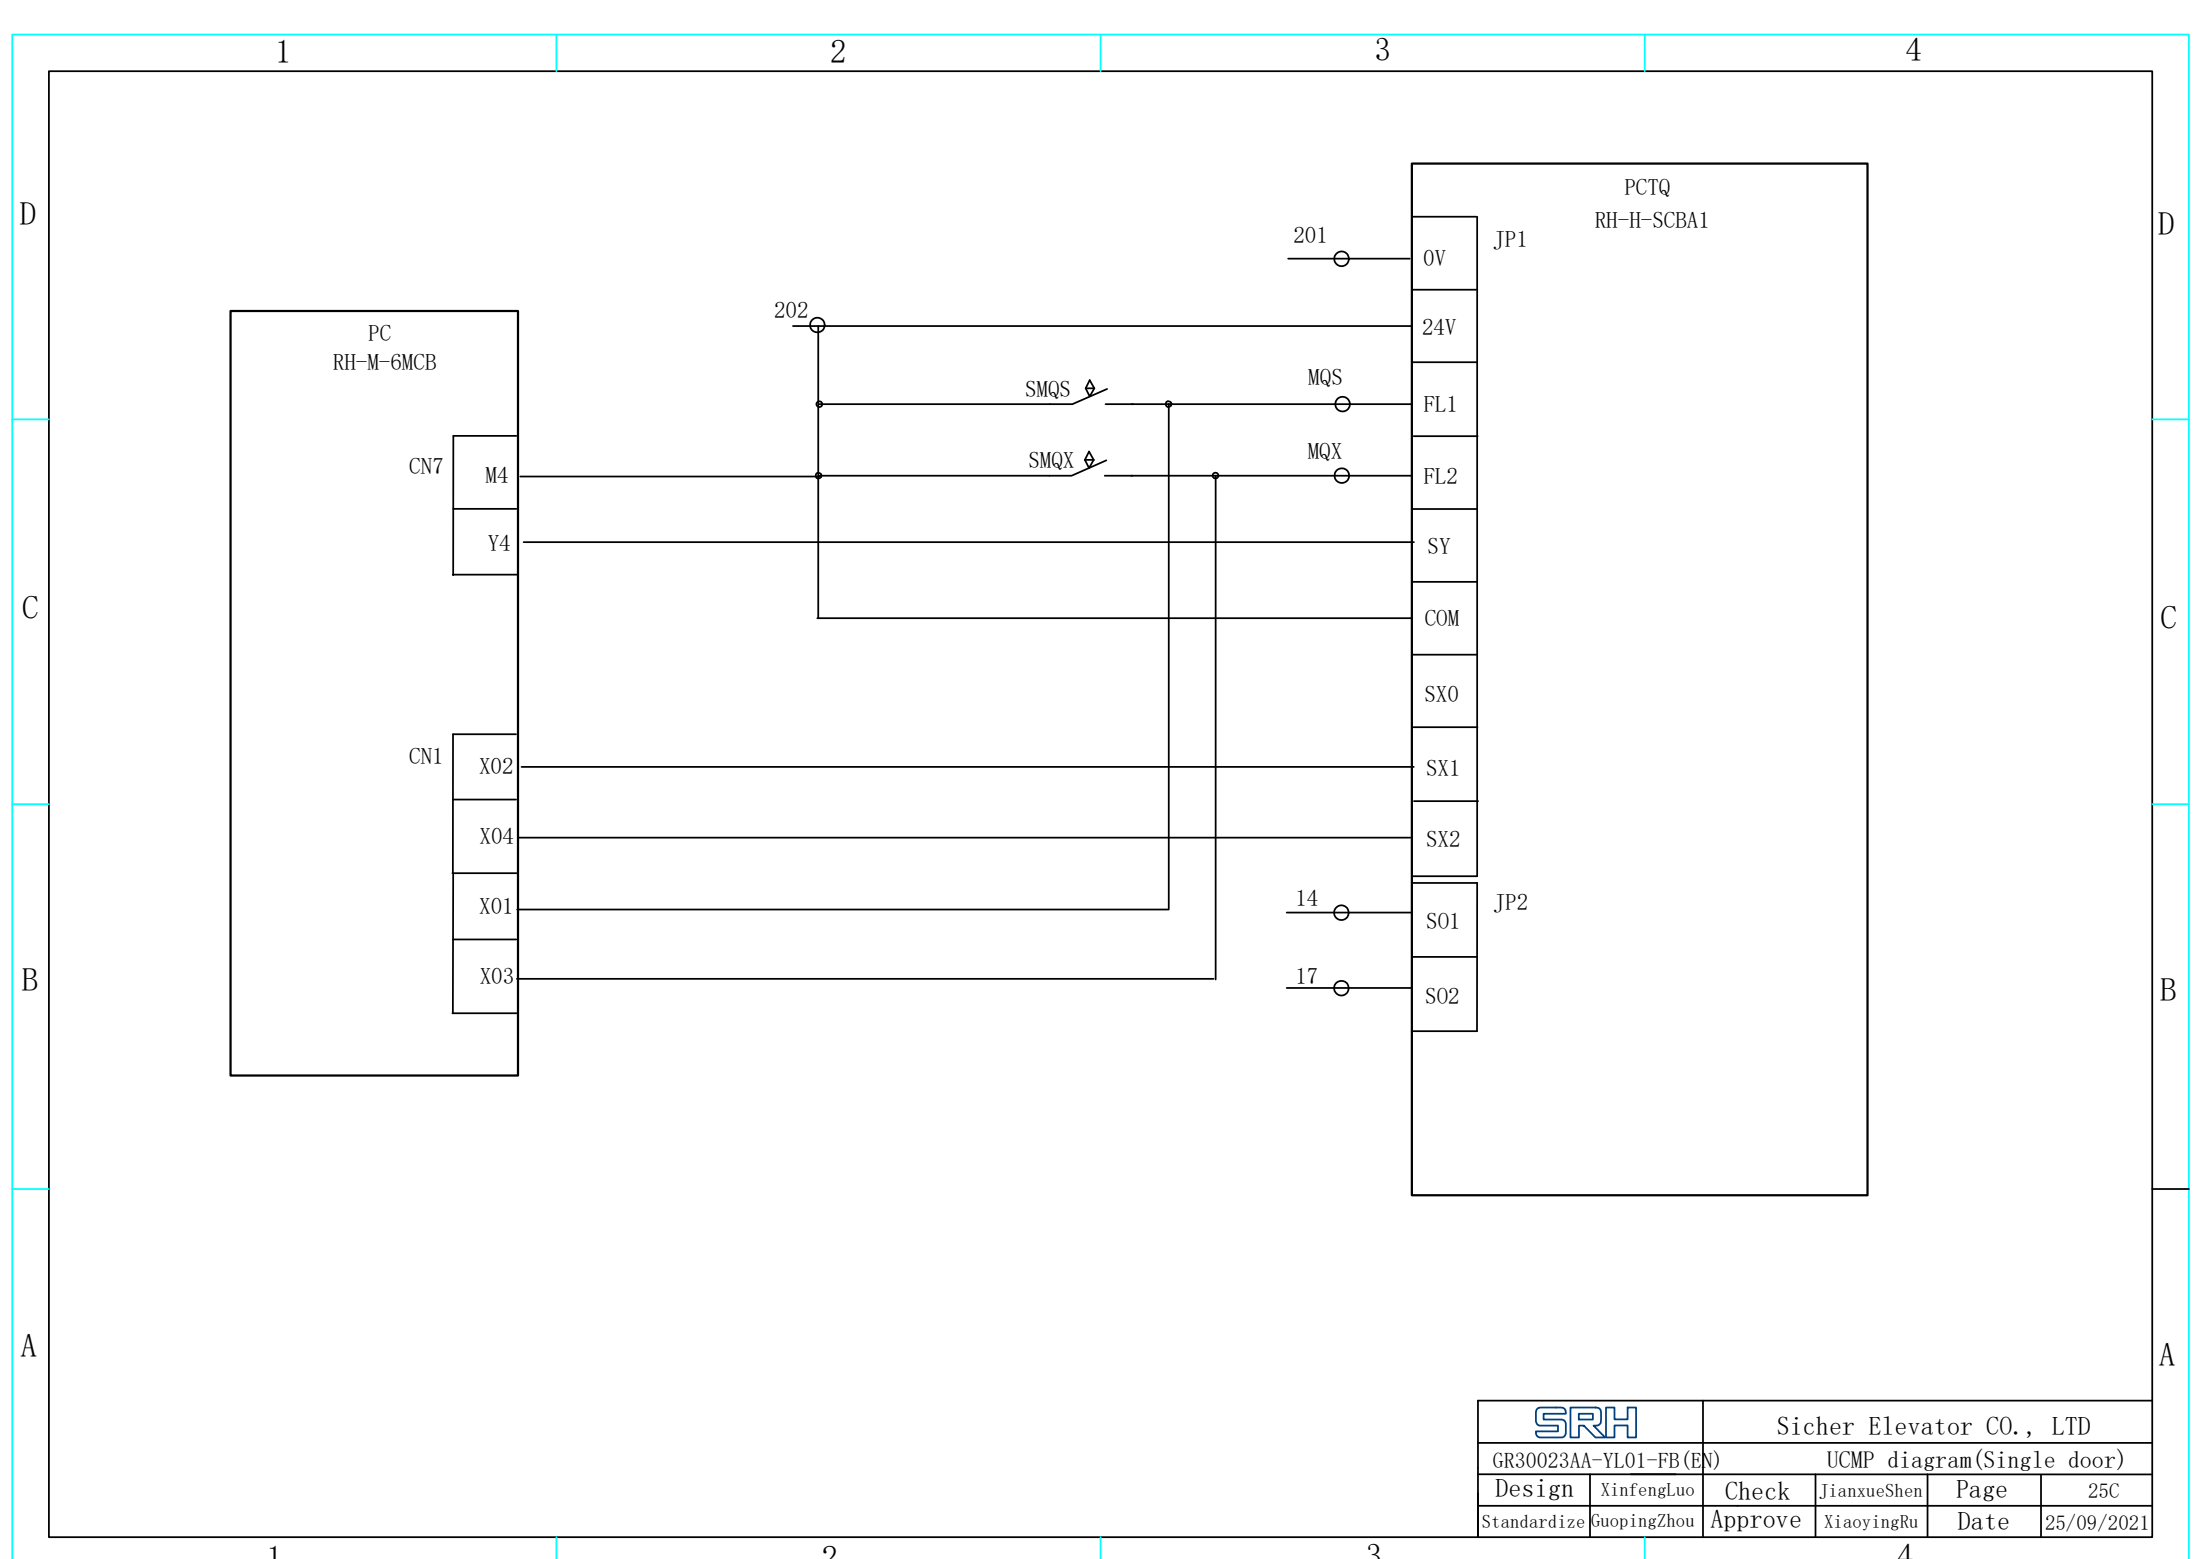

D

C

B


A

D

C

B

A

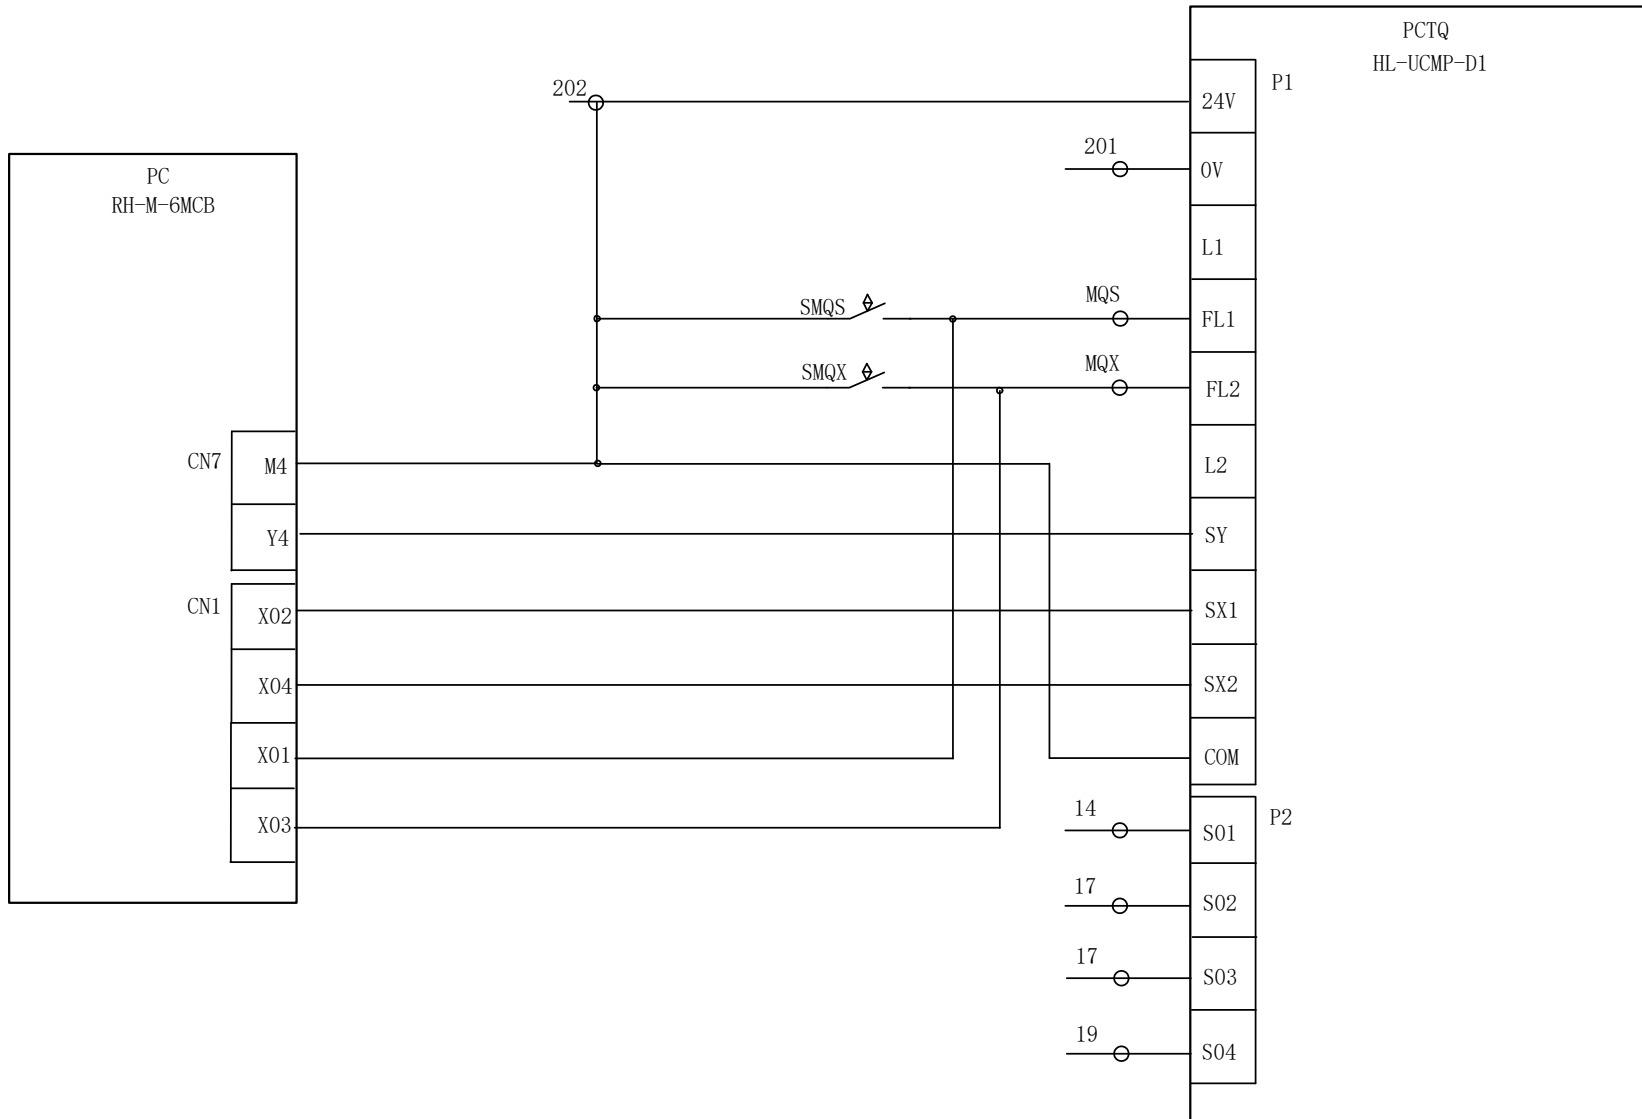

SRH		Sicher Elevator CO., LTD			
GR30023AA-YL01-FB(EN)		UCMP diagram(Double door)			
Design	XinfengLuo	Check	JianxueShen	Page	25D
Standardize	GuopingZhou	Approve	XiaoyingRu	Date	25/09/2021

Prefabricated Cable Diagram

Control system: RH6000

Drawing No. : GR31423AA-DL01. EN

Version: A

Matched drawing No. : GR30023AA-YL01. EN (A)
GR30023AA-YL02. EN (A)

Design: XinfengLuo 07/10/2021

Check: JianxueShen 07/10/2021

Standardize: GuopingZhou 07/10/2021

Approve: XiaoyingRu 07/10/2021

Sicher Elevator CO., LTD

1		2		3		4	
Catalog							
Page	Content	Remarks	Page	Content	Remarks		
1	Drawing catalog		10E	Shaft cable	L5A (MR)		
2	Drawing description & Changed record		10F	Shaft cable,Machine room cable	L1C, FL16A (MRL)		
3	Cable specification table		10G	Shaft cable,Machine room cable	L1D, FL16A (MRL)		
3A	Cable specification table		10H	Shaft cable,Machine room cable	L2B, FL17, FL9 (MRL)		
3B	Cable specification table		10I	Shaft cable,Machine room cable	L3B, FL12A/B (MRL)		
3C	Cable specification table		10J	Shaft cable,Machine room cable	L4C/D, FL15A (MRL)		
3D	Cable specification table		10K	Shaft cable	L5B (MRL)		
4	Parameter table,Calculation formula		11	Machine room cable	FL1, FL2, FL3, FL13		
5	Traveling cable selection table		11A	Machine room cable	FL4, FL5, FL6, FL7, FL14		
6	Power cable selection table		12	Branch cable of pit	KL1, KL2, KL3, KL4, KL5		
7	Traveling cable SXA	Gearless & Single door					
7A	Traveling cable SXB	Gearless & Single door					
7B	Traveling cable SXC	Gearless & Double door/Geared					
7C	Traveling cable SXD	Gearless & Double door/Geared					
7D	Traveling cable SXE	Gearless & Double door/Geared					
8	Branch cable of car top	JL11, JL13A/B/C					
8A	Branch cable of car top	JL14, JL15A/B, JL16					
8B	Branch cable of car top	JL17A/B, JL18A/B/C, JL19A/B					
8C	Branch cable of car top	JL20, JL21A/B, JL22A/B					
8D	Branch cable of car top	JL23, JL23A, JL24A/B					
9	Branch cable of car	CL15A/B, CL16					
10	Shaft cable,Machine room cable	L1A, FL16A (MR)					
10A	Shaft cable,Machine room cable	L1B, FL16A (MR)					
10B	Shaft cable,Machine room cable	L2A, FL17, FL9 (MR)					
10C	Shaft cable,Machine room cable	L3A, FL12A/B (MR)					
10D	Shaft cable,Machine room cable	L4A/B, FL15A (MR)					

SRH

GR31423AA-DL01. EN

DesignXinfengLuo

StandardizeGuopingZhou

Sicher Elevator CO., LTD

Drawing catalog

CheckJianxueShen

ApproveXiaoyingRu

Page1

Date07/10/2021

D

C

B

A

D

C

B

A

NO.	Plug-in types	Head end	Marks	Cable types	Cable specification	Cable length	Tail end	Plug-in types	Remarks
1	AMP 1-480708-0	K1	SXA~ SXE	TVVB	According to traveling cable selection table	MR:ZG+12 MRL:LH+10	J1	AMP 1-480708-0	Traveling cable
	AMP 1-480708-0	K2					J2	AMP 1-480708-0	
	AMP 1-480704-0	K4					J4	AMP 1-480704-0	
2	AMP 1-480704-0	J11	JL11	RVV	6*0.75	According to BOM	C11	AMP 1-480704-0	Car lighting, fan,emergency stop switch
3	AMP 1-480710-0	J13	JL13A	RVV	6*0.75	According to BOM	Pin terminal	VE040009	Door machine signals of rear door (with double door)
			JL13B	RVV	2*0.75	According to BOM	Pin terminal	VE040009	Light curtain signals of rear door (with double door)
			JL13C	RVV	6*0.75+1*2	According to BOM	C13	AMP 1-480706-0	Intercom of car,Emergency
4	AMP 1-480704-0	J14	JL14	RVVSP3	2*2P*0.75	According to BOM	C14	AMP 1-480704-0	Car communication
5	AMP 1-480704-0	J15	JL15A	RVV	2*0.75+1*2	According to BOM	U shape terminal	SV1.25-3	Light lamps of car
			JL15B	RVV	2*0.75+1*2	According to BOM	U shape terminal	SV1.25-3	Car fan
6	AMP 1-480700-0	J16	JL16	RVV	2*0.75+1*2	According to BOM	U shape terminal	SV1.25-3	Door machine power & light curtain power of front door
7	AMP 1-480704-0	J17	JL17A	RVV	2*0.75+1*2	According to BOM	U shape terminal	SV1.25-3	Car door lock of front door,Safety gear switch (with single door)
			JL17B	RVV	2*0.75+1*2	According to BOM	U shape terminal	SV1.25-3	
8	AMP 1-480706-0	J18	JL18A	RVV	2*0.75+1*2	According to BOM	U shape terminal	SV1.25-3	Car door lock of front door,Car door lock of rear door, Safety gear switch (with double door)
			JL18B	RVV	2*0.75+1*2	According to BOM	U shape terminal	SV1.25-3	
			JL18C	RVV	2*0.75+1*2	According to BOM	U shape terminal	SV1.25-3	
9	AMP 1-480702-0	J19	JL19A	RVV	2*0.75	According to BOM	U shape terminal	SV1.25-3	Car door lock detection switch of UCMP (with geared & double door)
			JL19B	RVV	2*0.75	According to BOM	U shape terminal	SV1.25-3	
10	AMP 1-480700-0	J20	JL20	RVV	2*0.75+1*2	According to BOM	U shape terminal	SV1.25-3	Door machine power & light curtain power of rear door (with double door)
11	AMP 1-480704-0	J21	JL21A	RVV	2*0.75+1*2	According to BOM	U shape terminal	SV1.25-3	Safety inspection pin switch(MRL)
			JL21B	RVV	2*0.75	According to BOM	U shape terminal	SV1.25-3	Car door lock detection switch of UCMP (with geared & single door)
12	AMP 1-480706-0	J22	JL22A	RVV	6*0.75	According to BOM	U shape terminal	VE040009	Door machine signals of front door
			JL22B	RVV	2*0.75	According to BOM	Pin terminal	VE040009	Light curtain signals of front door
13	AMP 1-480706-0	J23	JL23	RVV	6*0.75	According to BOM	U shape terminal	SV1.25-3	Door zone
			JL23A	RVV	3*0.75	According to BOM	U shape terminal	SV1.25-3	Door zone(non UCMP)

SRH		Sicher Elevator CO., LTD			
GR31423AA-DL01.EN		Cable specification table			
Design	XinfengLuo	Check	JianxueShen	Page	3
Standardize	GuopingZhou	Approve	XiaoyingRu	Date	07/10/2021

D

C

B

A

D

C

B

A

NO.	Plug-in types	Head end	Marks	Cable types	Cable specification	Cable length	Tail end	Plug-in types	Remarks
14	AMP 1-480704-0	J24	JL24A	RVV	3*0.75	According to BOM	U_shape terminal	SV1.25-3	Digital weigh device of car bottom (for passenger lift)
			JL24B	RVV	2*0.75	According to BOM	U_shape terminal	SV1.25-3	Acoustooptic alarming device
15	AMP 1-480706-0	FC15	CL15A	RVVSP3	2*2P*0.75	According to BOM	FC15	AMP 1-480706-0	Communication of auxiliary operation box (with auxiliary operation box)
			CL15B	RVV	2*0.75	According to BOM			Intercom of auxiliary operation box (with auxiliary operation box)
16	SV1.25-3	U shaped terminal	CL16	RVV	2*0.75	According to BOM	U_shape terminal	SV1.25-3	Intercom of disabled operation box (wiht disabled operation box)
17	AMP 1-480708-0	K5	L1A		6*0.75+1*2	KD1	DK5	AMP 1-480706-0	Safety, door lock(single door & LH ≤120m)
					6*1.5+1*2				Safety, door lock(single door & LH >120m)
			FL16A	RVV	2*0.75	According to BOM	U_shape terminal	SV1.25-3	Group control power connect to power distribution box (single door)
			L1B	RVV	7*0.75+1*2	KD1	DK5	AMP 1-480706-0	Safety, door lock(double door & LH ≤120m)
					7*1.5+1*2				Safety, door lock(double door & LH >120m)
			FL16A		2*0.75	According to BOM	U_shape terminal	SV1.25-3	Group control power connect to power distribution box (double door)
18	AMP 1-480708-0	K6	L2A	RVV	4*0.75	KD2	DK6	AMP 1-480704-0	Shaft lighting
			FL17	RVV	2*0.75	According to BOM	U_shape terminal	SV1.25-3	Wire rope lighting(MRL)
			FL9	RVV	4*0.75	According to BOM	U_shape terminal	SV1.25-3	Intercom of control cabinet

SRH		Sicher Elevator CO., LTD			
GR31423AA-DL01.EN		Cable specification table			
Design	XinfengLuo	Check	JianxueShen	Page	3A
Standardize	GuopingZhou	Approve	XiaoyingRu	Date	07/10/2021

D

C

B

A

D

C

B

A

NO.	Plug-in types	Head end	Marks	Cable types	Cable specification	Cable length	Tail end	Plug-in types	Remarks
19	AMP 1-480708-0	K7	L3A	RVV	4*0.5	KD3	U_shape terminal	SV1.25-3	Intercom of pit
			FL12A	RVV	2*0.75+1*2	According to BOM	U_shape terminal	SV1.25-3	Overspeed governor(gearless)
			L3A	RVV	4*0.5	KD3	U_shape terminal	SV1.25-3	Intercom of pit
			FL12B	RVV	4*0.75+1*2	According to BOM	Pin terminal	VE040009	Overspeed governor(gearless)
20	AMP 1-480708-0	K8	L4A	RVV	3*0.75+1*2	KD4	U_shape terminal	SV1.25-3	Shaft switch $V \leq 1.75m/s$
			FL15A	RVV	4*0.75	According to BOM	Pin terminal	VE040009	Overspeed governor(gearless)
			L4B	RVV	5*0.75+1*2	KD4	U_shape terminal	SV1.25-3	Shaft switch $2.0m/s \leq V \leq 2.5m/s$
			FL15A	RVV	4*0.75	According to BOM	Pin terminal	VE040009	Overspeed governor(gearless)
21	AMP 1-480704-0	K9	L5A	RVVSP3	2*2P*0.75	KD5	communication plug-in	/	Landing call communication LH $\leq$ 120
					2*2P*1.5				Landing call communication LH $>$ 120
22	AMP 1-480710-0	K10	FL1	RVV	2*0.75+1*2	According to BOM	Pin terminal	VE040009	Brake coil
			FL2	RVV	4*0.75+1*2	According to BOM	U_shape terminal	SV1.25-3	AC220V connect to the power distribution box(MR)
			FL3	RVV	3*0.75	According to BOM	U_shape terminal	SV1.25-3	Overspeed governor mechanical and reset(MRL)
			FL13	RVV	4*0.75	According to BOM	U_shape terminal	SV1.25-3	The digital weigh device of machine room

SRH		Sicher Elevator CO., LTD			
GR31423AA-DL01.EN		Cable specification table			
Design	XinfengLuo	Check	JianxueShen	Page	3B
Standardize	GuopingZhou	Approve	XiaoyingRu	Date	07/10/2021

D

C

B

A

NO.	Plug-in types	Head end	Marks	Cable types	Cable specification	Cable length	Tail end	Plug-in types	Remarks
23	AMP 1-480710-0	K11	FL4	RVV	2*0.75	According to BOM	U_shape terminal	SV1.25-3	To the power distribution box (with the elevator emergency leveling device)
			FL5	RVV	2*0.75	According to BOM	Pin terminal	VE040009	Motor thermal protection
			FL6	RVV	2*0.75+1*2	According to BOM	U_shape terminal	SV1.25-3	Hand wheel switch(MR) MRL stop switch(MRL)
			FL7	RVV	2*0.75+1*2	According to BOM	U_shape terminal	SV1.25-3	Action on traction Wire holder switch(g geared)
			FL14	RVV	3*0.75	According to BOM	Pin terminal	VE040009	Brake limit switch
24	AMP 1-480700-0	DK11	KL1	RVV	2*0.75+1*2	According to BOM	U_shape terminal	SV1.25-3	Buffer switch
25	AMP 1-480700-0	DK12	KL2	RVV	2*0.75+1*2	According to BOM	U_shape terminal	SV1.25-3	Overspeed governor rope breaking switch
26	AMP 1-480700-0	DK13	KL3	RVV	2*0.75	According to BOM	U_shape terminal	SV1.25-3	Emergency stop switch of pit (pit emergency stop box)
27	AMP 1-480700-0	DK14	KL4	RVV	3*0.75	According to BOM	U_shape terminal	SV1.25-3	Shaft lighting lamps (pit emergency stop box)
28	AMP 1-480700-0	DK15	KL5	RVV	2*0.75	According to BOM	U_shape terminal	SV1.25-3	Shaft lighting lamps
29	AMP 1-480708-0	K5	L1C	RVV	6*0.75+1*2	KD11	DK5	AMP 1-480706-0	Safety, door lock(single door & LH ≤120m)
					6*1.5+1*2				Safety, door lock(single door & LH >120m)
			FL16A		2*0.75	According to BOM	U_shape terminal	SV1.25-3	Group control power connect to power distribution box (single door)
			L1D	RVV	7*0.75+1*2	KD11	DK5	AMP 1-480706-0	Safety, door lock(double door & LH ≤120m)
					7*1.5+1*2				Safety, door lock(double door & LH >120m)
			FL16A		2*0.75	According to BOM	U_shape terminal	SV1.25-3	Group control power connect to power distribution box (double door)
30	AMP 1-480708-0	K6	L2B	RVV	4*0.75	KD21	DK6	AMP 1-480704-0	Shaft lighting
			FL17	RVV	2*0.75	According to BOM	U_shape terminal	SV1.25-3	Wire rope lighting(MRL)
			FL9	RVV	4*0.75	According to BOM	U_shape terminal	SV1.25-3	Intercom of control cabinet

D

C

B

A

SRH		Sicher Elevator CO., LTD			
GR31423AA-DL01.EN		Cable specification table			
Design	XinfengLuo	Check	JianxueShen	Page	3C
Standardize	GuopingZhou	Approve	XiaoyingRu	Date	07/10/2021

D

C

B

A

D

C

B

A

NO.	Plug-in types	Head end	Marks	Cable types	Cable specification	Cable length	Tail end	Plug-in types	Remarks
31	AMP 1-480708-0	K7	L3B	RVV	4*0.5	KD31	U_shape terminal	SV1.25-3	Intercom of pit
			FL12A	RVV	2*0.75+1*2	According to BOM	U_shape terminal	SV1.25-3	Overspeed governor(gearless)
			L3B	RVV	4*0.5	KD31	U_shape terminal	SV1.25-3	Intercom of pit
			FL12B	RVV	4*0.75+1*2	According to BOM	Pin terminal	VE040009	Overspeed governor(gearless)
32	AMP 1-480708-0	K8	L4C	RVV	3*0.75+1*2	KD41	U_shape terminal	SV1.25-3	Shaft switch $V \leq 1.75\text{m/s}$
			FL15A	RVV	4*0.75	According to BOM	Pin terminal	VE040009	Overspeed governor(gearless)
			L4D	RVV	5*0.75+1*2	KD41	U_shape terminal	SV1.25-3	Shaft switch $2.0\text{m/s} \leq V \leq 2.5\text{m/s}$
			FL15A	RVV	4*0.75	According to BOM	Pin terminal	VE040009	Overspeed governor(gearless)
33	AMP 1-480704-0	K9	L5B	RVVSP3	2*2P*0.75	KD51	communication plug-in	/	Landing call communication $LH \leq 120$
					2*2P*1.5				Landing call communication $LH > 120$

MRL

Shaft main cable marks	Branch cable marks	Cable types	Cable specification	Cable length	Quantity	Remarks
L1A/L1B/ L1C/L1D	JTM	RVV	2*0.75+1*2	According to BOM	KD6	Landing door lock of front door branch cable
	JHTM			According to BOM	KD7	Landing door lock of rear door branch cable
	JXS			According to BOM	1	Up final limit switch branch cable
	JXX			According to BOM	1	Down final limit switch branch cable
L2A/L2B	JZMF		2*0.75	According to BOM	KD8	Light lamps of shaft branch cable
L4A/L4B/ L4C/L4D	DSS		2*0.75+1*2	According to BOM	1	Up slow_down switch 1 branch cable
	ZSS			According to BOM	1	Up slow_down switch 2 branch cable
	ZSX			According to BOM	1	Down slow_down switch 2 branch cable
	DSX			According to BOM	1	Down slow_down switch 1 branch cable
L5A/L5B	JZH	RVVSP3	2*2P*0.75	According to BOM	KD6	Landing call communication of front door branch cable
	JHZH			According to BOM	KD7	Landing call communication of rear door branch cable

SRH

Sicher Elevator CO., LTD

GR31423AA-DL01.EN

Cable specification table

Design

XinfengLuo

Check

JianxueShen

Page

3D

Standardize

GuopingZhou

Approve

XiaoyingRu

Date

07/10/2021

D

C

B

A

D

C

B

A


Traveling cable SXA (Gearless & Single door)

Plug-in unit of control cabinet	Pin No.	Drawing wire mark	Cables' color and wire mark	Drawing wire mark	Pin No.	Plug-in unit of car top
K1 AMP 1-480708-0	1	500	SX-black-1	500	1	J1 AMP 1-480708-0
	2	501	SX-black-2	501	2	
	3	14	SX-black-3	14	3	
	4	15	SX-black-4	15	4	
	5	A12	SX-black-5	A12	5	
	6	A16	SX-black-6	A16	6	
	7	101	SX-black-7	101	7	
	8	102	SX-black-8	102	8	
	9				9	
	10				10	
	11				11	
	12	BK1	SX-black-9	BK1	12	
K2 AMP 1-480708-0	1	L1	SX-black-10	L1	1	J2 AMP 1-480708-0
	2	L2	SX-black-11	L2	2	
	3	L3	SX-black-12	L3	3	
	4	MQS	SX-black-13	MQS	4	
	5	MQX	SX-black-14	MQX	5	
	6				6	
	7				7	
	8				8	
	9				9	
	10				10	
	11	PE	SX-black-15	PE	11	
	12	PE	SX-black-16	PE	12	
	1				1	
	2				2	
	3				3	
	4				4	
	5				5	
	6				6	
	7				7	
	8				8	
	9				9	
	10				10	
	11				11	
	12				12	
K4 AMP 1-480704-0	1	202	SX-white-1	202	1	J4 AMP 1-480704-0
	2	201	SX-white-2	201	2	
	3				3	
	4	CAN+	SX-white-3	CAN+	4	
	5	CAN-	SX-white-4	CAN-	5	
	6	PE1	Shielding Layer	PE1	6	

AMP 1-480708-0

AMP 1-480708-0

AMP 1-480704-0

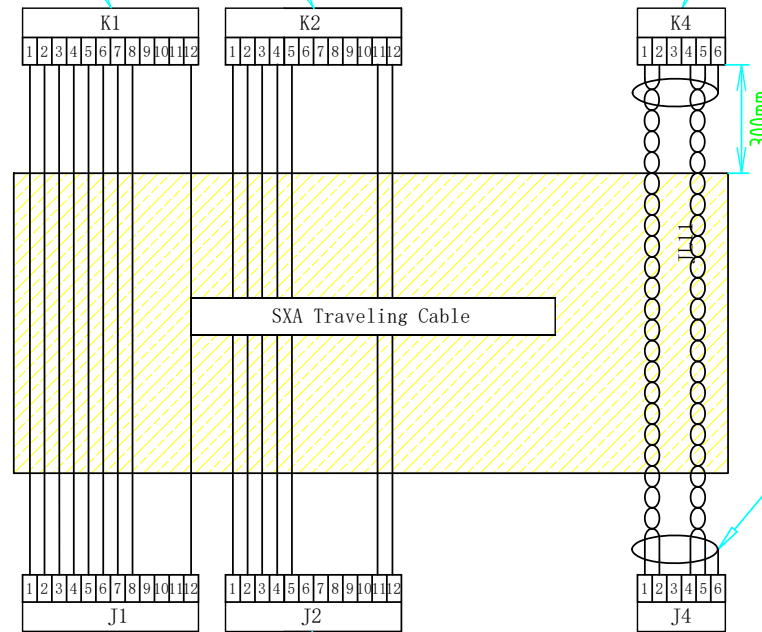

Shielding Layer

AMP 1-480708-0

AMP 1-480708-0

AMP 1-480704-0

Traveling cable selection table SXA(Gearless & Single door)

Code	Cable types	Cable specification	Remarks	Wire marks
SXA	TVVBP3	16*0.75+2*2P*0.75	LH≤65m	black:1-4,5-8,9-12,13-16; white:1-2,3-4
	TVVBP3G	16*0.75+2*2P*0.75	LH>65m	
	TVVBP3	16*0.75+2*2P*0.75+CAT5e	With network cable & LH≤65m	
	TVVBP3G	16*0.75+2*2P*0.75+CAT5e	With network cable & LH>65m	

SRH

Sicher Elevator CO., LTD

GR31423AA-DL01.EN		Traveling cable SXA (Gearless & Single door)			
Design	XinfengLuo	Check	JianxueShen	Page	7
Standardize	GuopingZhou	Approve	XiaoyingRu	Date	07/10/2021

D

C

B

A

D

C

B


A

Traveling cable SXB (Gearless & Single door)						
Plug-in unit of control cabinet	Pin No	Drawing wire mark	Cables' color and wire mark	Drawing wire mark	Pin No	Plug-in unit of car top
K1 AMP 1-480708-0	1	500	SX-blue-1	500	1	J1 AMP 1-480708-0
	2	501	SX-blue-2	501	2	
	3	14	SX-blue-3	14	3	
	4	15	SX-blue-4	15	4	
	5	A12	SX-blue-5	A12	5	
	6	A16	SX-blue-6	A16	6	
	7	101	SX-blue-18	101	7	
	8	102	SX-blue-19	102	8	
	9				9	
	10				10	
	11				11	
	12	BK1	SX-blue-20	BK1	12	
K2 AMP 1-480708-0	1	L1	SX-blue-13	L1	1	J2 AMP 1-480708-0
	2	L2	SX-blue-14	L2	2	
	3	L3	SX-blue-15	L3	3	
	4	MQS	SX-blue-16	MQS	4	
	5	MQX	SX-blue-17	MQX	5	
	6				6	
	7				7	
	8				8	
	9				9	
	10				10	
	11	PE	SX-YG-1	PE	11	
	12	PE	SX-YG-2	PE	12	
K4 AMP 1-480704-0	1				1	J4 AMP 1-480704-0
	2				2	
	3				3	
	4				4	
	5				5	
	6				6	
	7				7	
	8				8	
	9				9	
	10				10	
	11				11	
	12				12	
K4 AMP 1-480704-0	1	202	SX-white-1	202	1	J4 AMP 1-480704-0
	2	201	SX-white-2	201	2	
	3				3	
	4	CAN+	SX-white-3	CAN+	4	
	5	CAN-	SX-white-4	CAN-	5	
	6	PE1	Shielding Layer	PE1	6	

AMP 1-480708-0

AMP 1-480708-0

AMP 1-480704-0

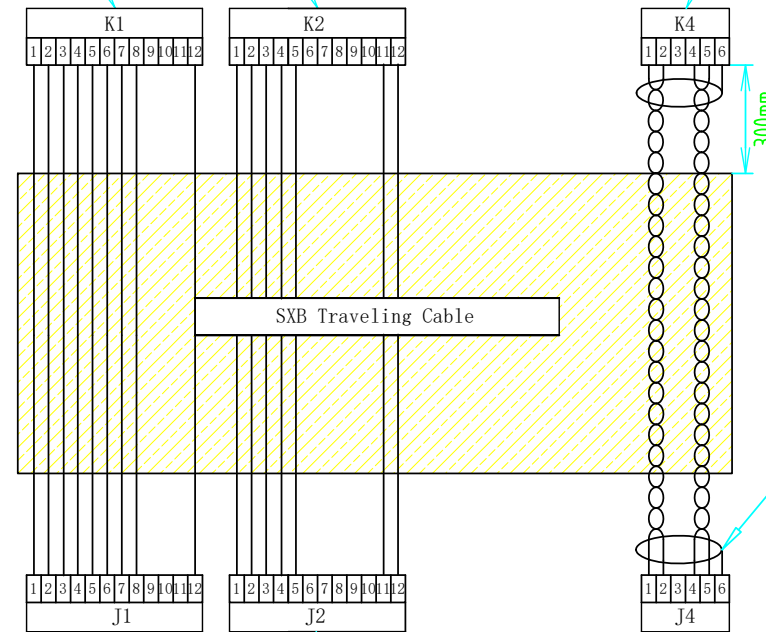

AMP 1-480708-0

AMP 1-480708-0

AMP 1-480704-0

Traveling cable selection table SXB(Gearless & Single door)				
Code	Cable types	Cable specification	Remarks	Wire marks
SXB	TVVBP3	20*0.75+2*2P*0.75+2*0.75	With air conditioning & LH≤65m	blue:1-6, 7-12, 13-17, 18-20; yellow&green:1-2; white:1-2, 3-4
	TVVBP3G	20*0.75+2*2P*0.75+2*0.75	With air conditioning & LH>65m	
	TVVBP3-TV	20*0.75+2*2P*0.75+2*0.75+75-5	(With air conditioning cable & coaxial cable/ With coaxial cable) & LH≤65m	
	TVVBP3G-TV	20*0.75+2*2P*0.75+2*0.75+75-5	(With air conditioning cable & coaxial cable/ With coaxial cable) & LH>65m	
	TVVBP3	20*0.75+2*2P*0.75+2*0.75	(With air conditioning cable & network cable) & LH≤65m	
	TVVBP3	CAT5e		
	TVVBP3G	20*0.75+2*2P*0.75+2*0.75	(With air conditioning cable & network cable) & LH>65m	
	TVVBP3G	CAT5e		

Notes:YG--Yellow&Green.

SRH		Sicher Elevator CO., LTD			
GR31423AA-DL01.EN		Traveling cable SXB (Gearless & Single door)			
Design	XinfengLuo	Check	JianxueShen	Page	7A
Standardize	GuopingZhou	Approve	XiaoyingRu	Date	07/10/2021

1

2

3

4

D

C

B

A

D

C

B


A

Traveling cable SXC(Gearless & Double door/Geared)						
Plug-in unit of control cabinet	Pin No	Drawing wire mark	Cables' color and wire mark	Drawing wire mark	Pin No	Plug-in unit of car top
K1 AMP 1-480708-0	1	500	SX-black-1	500	1	J1 AMP 1-480708-0
	2	501	SX-black-2	501	2	
	3	14	SX-black-3	14	3	
	4	15	SX-black-4	15	4	
	5	A12	SX-black-5	A12	5	
	6	A16	SX-black-6	A16	6	
	7	101	SX-black-7	101	7	
	8	102	SX-black-8	102	8	
	9	18	SX-black-9	18	9	
	10	19	SX-black-10	19	10	
	11				11	
	12	BK1	SX-black-13	BK1	12	
K2 AMP 1-480708-0	1	L1	SX-black-14	L1	1	J2 AMP 1-480708-0
	2	L2	SX-black-15	L2	2	
	3	L3	SX-black-16	L3	3	
	4	MQS	SX-black-17	MQS	4	
	5	MQX	SX-black-18	MQX	5	
	6	SMJ2	SX-black-19	SMJ2	6	
	7	S06	SX-black-20	S06	7	
	8				8	
	9				9	
	10				10	
	11	PE	SX-black-11	PE	11	
	12	PE	SX-black-12	PE	12	
	1				1	
	2				2	
	3				3	
	4				4	
	5				5	
	6				6	
	7				7	
	8				8	
	9				9	
	10				10	
	11				11	
	12				12	
K4 AMP 1-480704-0	1	202	SX-white-1	202	1	J4 AMP 1-480704-0
	2	201	SX-white-2	201	2	
	3				3	
	4	CAN+	SX-white-3	CAN+	4	
	5	CAN-	SX-white-4	CAN-	5	
	6	PE1	Shielding Layer	PE1	6	

AMP 1-480708-0

AMP 1-480708-0

AMP 1-480704-0

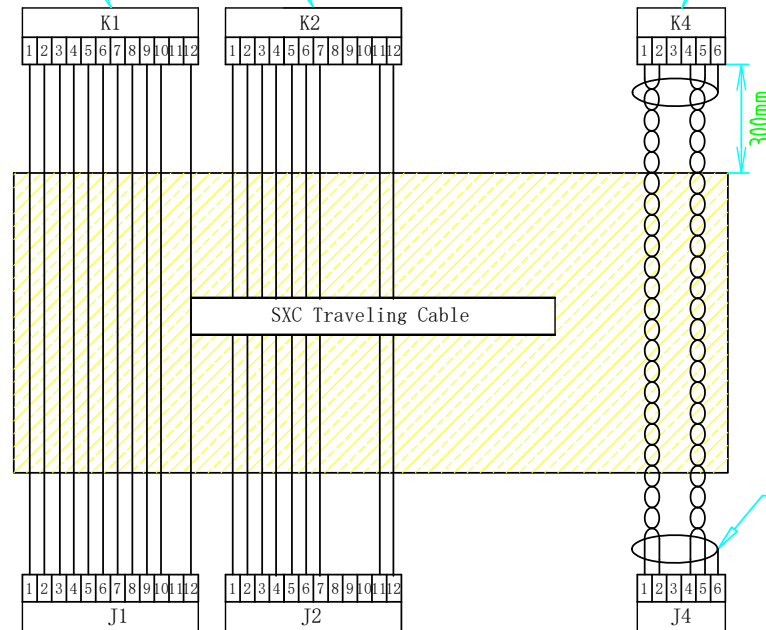

AMP 1-480708-0

AMP 1-480708-0

AMP 1-480704-0

Traveling cable selection table SXC(Gearless & Double door/Geared)				
Code	Cable types	Cable specification	Remarks	Wire marks
SXC	TVVBP3	20*0.75+2*2P*0.75	LH≤65m	black:1-4, 5-8, 9-12, 13-16, 17-20; white:1-2, 3-4
	TVVBP3G	20*0.75+2*2P*0.75	LH>65m	
	TVVBP3	20*0.75+2*2P*0.75	With network cable & LH≤65m	
	TVVBG	CAT5e		
	TVVBP3G	20*0.75+2*2P*0.75	With network cable & LH>65m	
	TVVBG	CAT5e		

SRH

Sicher Elevator CO., LTD

GR31423AA-DL01.EN		Traveling cable SXC (Gearless & Double door/Geared)			
Design	XinfengLuo	Check	JianxueShen	Page	7B
Standardize	GuopingZhou	Approve	XiaoyingRu	Date	07/10/2021

D

C

B

A

D

C

B


A

Traveling cable SXD (Gearless & Double door/Geared)						
Plug-in unit of control cabinet	Pin No	Drawing wire mark	Cables' color and wire mark	Drawing wire mark	Pin No	Plug-in unit of car top
K1 AMP 1-480708-0	1	500	SX-blue-1	500	1	J1 AMP 1-480708-0
	2	501	SX-blue-2	501	2	
	3	14	SX-blue-3	14	3	
	4	15	SX-blue-4	15	4	
	5	A12	SX-blue-5	A12	5	
	6	A16	SX-blue-6	A16	6	
	7	101	SX-blue-13	101	7	
	8	102	SX-blue-14	102	8	
	9	18	SX-blue-15	18	9	
	10	19	SX-blue-16	19	10	
	11				11	
	12	BK1	SX-blue-17	BK1	12	
K2 AMP 1-480708-0	1	L1	SX-blue-7	L1	1	J2 AMP 1-480708-0
	2	L2	SX-blue-8	L2	2	
	3	L3	SX-blue-9	L3	3	
	4	MQS	SX-blue-10	MQS	4	
	5	MQX	SX-blue-11	MQX	5	
	6	SMJ2	SX-blue-12	SMJ2	6	
	7	S06	SX-blue-18	S06	7	
	8				8	
	9				9	
	10				10	
	11	PE	SX-YG-1	PE	11	
	12	PE	SX-YG-2	PE	12	
K4 AMP 1-480704-0	1				1	J4 AMP 1-480704-0
	2				2	
	3				3	
	4				4	
	5				5	
	6				6	
	7				7	
	8				8	
	9				9	
	10				10	
	11				11	
	12				12	
K4 AMP 1-480704-0	1	202	SX-white-1	202	1	J4 AMP 1-480704-0
	2	201	SX-white-2	201	2	
	3				3	
	4	CAN+	SX-white-3	CAN+	4	
	5	CAN-	SX-white-4	CAN-	5	
	6	PE1	Shielding Layer	PE1	6	

AMP 1-480708-0

AMP 1-480708-0

AMP 1-480704-0

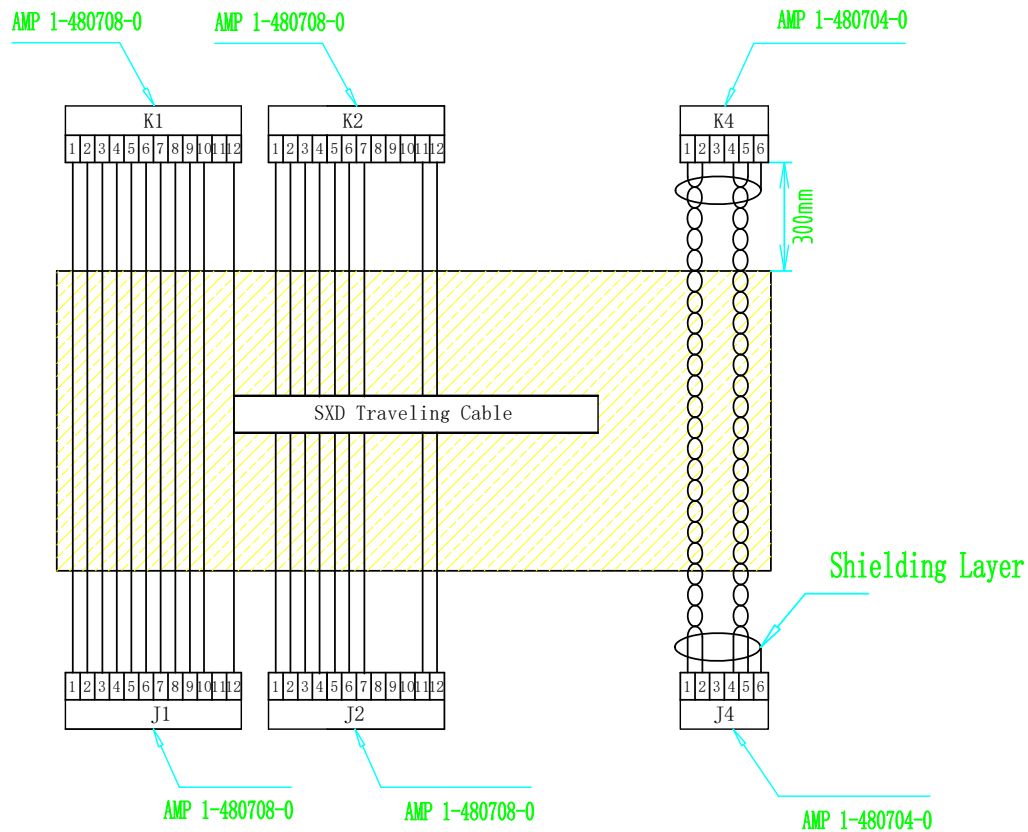

Traveling cable selection table SXD(Gearless & Double door/Geared)				
Code	Cable types	Cable specification	Remarks	Wire marks
SXD	TVVBP3-TV	20*0.75+2*2P*0.75+2*0.75+75-5	With coaxial cable & LH≤65m	blue:1-6,7-12,13-17,18-20; yellow&green:1-2; white:1-2,3-4
	TVVBP3G-TV	20*0.75+2*2P*0.75+2*0.75+75-5	With coaxial cable & LH>65m	

Notes:YG--Yellow&Green.

SRH		Sicher Elevator CO., LTD			
GR31423AA-DL01.EN		Traveling cable SXD (Gearless & Double door/Geared)			
Design	XinfengLuo	Check	JianxueShen	Page	7C
Standardize	GuopingZhou	Approve	XiaoyingRu	Date	07/10/2021

D

C

B

A

D

C

B


A

Traveling cable SXE (Gearless & Double door/Geared)						
Plug-in unit of control cabinet	Pin No	Drawing wire mark	Cables' color and wire mark	Drawing wire mark	Pin No	Plug-in unit of car top
K1 AMP 1-480708-0	1	500	SX-grey-1	500	1	J1 AMP 1-480708-0
	2	501	SX-grey-2	501	2	
	3	14	SX-grey-3	14	3	
	4	15	SX-grey-4	15	4	
	5	A12	SX-grey-5	A12	5	
	6	A16	SX-grey-6	A16	6	
	7	101	SX-grey-7	101	7	
	8	102	SX-grey-8	102	8	
	9	18	SX-grey-9	18	9	
	10	19	SX-grey-10	19	10	
	11				11	
	12	BK1	SX-blue-1	BK1	12	
K2 AMP 1-480708-0	1	L1	SX-blue-2	L1	1	J2 AMP 1-480708-0
	2	L2	SX-blue-3	L2	2	
	3	L3	SX-blue-4	L3	3	
	4	MQS	SX-blue-5	MQS	4	
	5	MQX	SX-blue-6	MQX	5	
	6	SMJ2	SX-orange-7	SMJ2	6	
	7	S06	SX-orange-8	S06	7	
	8				8	
	9				9	
	10				10	
	11	PE	SX-grey-11	PE	11	
	12	PE	SX-grey-12	PE	12	
K4 AMP 1-480704-0	1				1	J4 AMP 1-480704-0
	2				2	
	3				3	
	4				4	
	5				5	
	6				6	
	7				7	
	8				8	
	9				9	
	10				10	
	11				11	
	12				12	
K4 AMP 1-480704-0	1	202	SX-white-1	202	1	J4 AMP 1-480704-0
	2	201	SX-white-2	201	2	
	3				3	
	4	CAN+	SX-white-3	CAN+	4	
	5	CAN-	SX-white-4	CAN-	5	
	6	PE1	Shielding Layer	PE1	6	

AMP 1-480708-0

AMP 1-480708-0

AMP 1-480704-0

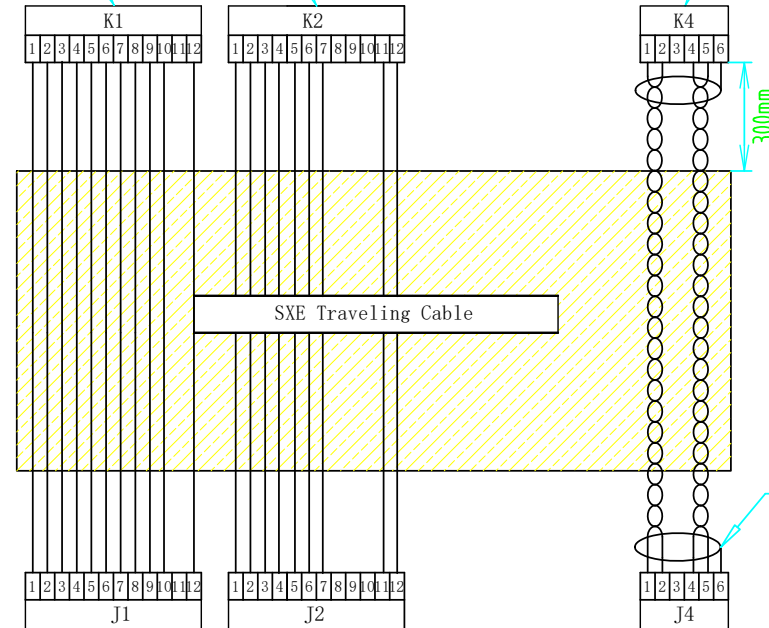

Shielding Layer

AMP 1-480708-0

AMP 1-480708-0

AMP 1-480704-0

Traveling cable selection table SXE(Gearless & Double door/Geared)				
Code	Cable types	Cable specification	Remarks	Wire marks
SXE	TVVBP3	26*0.75+2*2P*0.75+1*2	With air conditioning & LH≤65m	grey:1-6, 7-12; blue:1-6, 7-12; orange:7-8; yellow&green:1; white:1-2, 3-4
	TVVBP3G	26*0.75+2*2P*0.75+1*2	With air conditioning & LH>65m	
	TVVBP3	26*0.75+2*2P*0.75+1*2	(With air conditioning cable & network cable) & LH≤65m	
	TVVBG	CAT5e		
	TVVBP3G	26*0.75+2*2P*0.75+1*2	(With air conditioning cable & network cable) & LH>65m	
	TVVBG	CAT5e		

SRH

Sicher Elevator CO., LTD

GR31423AA-DL01.EN		Traveling cable SXE (Gearless & Double door/Geared)			
Design	XinfengLuo	Check	JianxueShen	Page	7D
Standardize	GuopingZhou	Approve	XiaoyingRu	Date	07/10/2021

D

C

B

A

D

C

B

A

1

2

3

4


Branch cable of car top JL11

Plug-in unit of car top	Pin No.	Drawing wire mark	Cables' color and wire mark	Drawing wire mark	Pin No.	Plug-in unit of main operation box
J11 AMP 1-480704-0	1	BK11	JL11-black-1	BK11	1	C11 AMP 1-480704-0
	2	502	JL11-black-2	502	2	
	3	503	JL11-black-3	503	3	
	4	504	JL11-black-4	504	4	
	5	A14	JL11-black-5	A14	5	
	6	A13	JL11-black-6	A13	6	

Branch cable of car top JL13A/B/C

Plug-in unit of car top	Pin No.	Drawing wire mark	Cables' color and wire mark	Drawing wire mark	Pin No.	Plug-in unit of shaped terminal
J13 AMP 1-480710-0	1	1M6	JL13A-black-1	1M6	1	VE040009
	2	1M8	JL13A-black-2	1M8	2	VE040009
	3	1M9	JL13A-black-3	1M9	3	VE040009
	4	36	JL13A-black-4	36	4	VE040009
	5	37	JL13A-black-5	37	5	VE040009
	6	202	JL13A-black-6	202	6	VE040009
	7	1AP	JL13B-black	1AP	7	VE040009
	8	202	JL13B-brown	202	8	VE040009
	9	L1	JL13C-black-1	L1	1	C13 AMP 1-480706-0
	10	L2	JL13C-black-2	L2	2	
	11	L3	JL13C-black-3	L3	3	
	12	201	JL13C-black-4	201	4	
	13	YJ1	JL13C-black-5	YJ1	5	
	14	YJ2	JL13C-black-6	YJ2	6	
	15	PE	JL13C-YG	PE	7	

Notes:YG--Yellow&Green.

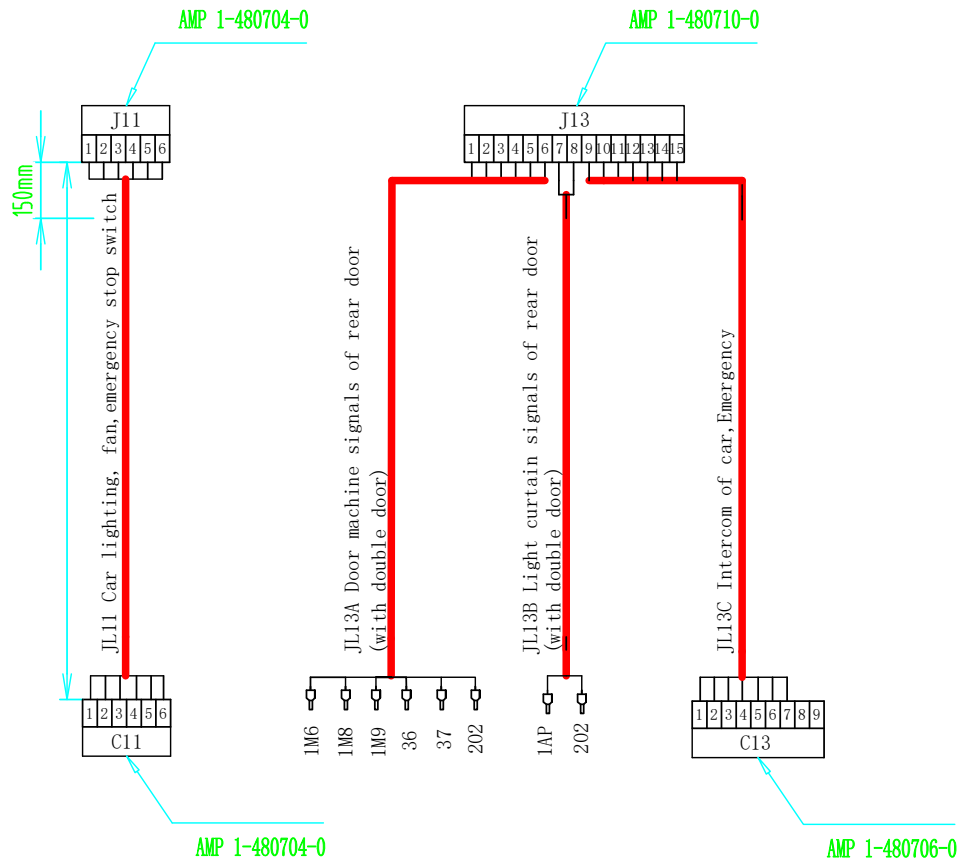

SRH		Sicher Elevator CO., LTD			
GR31423AA-DL01.EN		Branch Cable of Car Top(JL11,JL13A/B/C)			
Design	XinfengLuo	Check	JianxueShen	Page	8
Standardize	GuopingZhou	Approve	XiaoyingRu	Date	07/10/2021

1

2

3

4

D

C

B

A

D

C

B


A

Branch cable of car top JL14						
Plug-in unit of car top	Pin No.	Drawing wire mark	Cables color and wire mark	Drawing wire mark	Pin No.	Plug-in unit of main operation box
J14 AMP 1-480704-0	1	24V	JL14-white-1	24V	1	C14 AMP 1-480704-0
	2	COM	JL14-white-2	COM	2	
	3				3	
	4	MOD+	JL14-white-3	MOD+	4	
	5	MOD-	JL14-white-4	MOD-	5	
	6	PE1	Shielding Layer	PE1	6	

Branch cable of car top JL15A/B					
Plug-in unit of car top	Pin No.	Drawing wire mark	Cables color and wire mark	Drawing wire mark	U shaped terminal types
J15 AMP 1-480704-0	1	501	JL15A-brown	501	SV1.25-3
	2	503	JL15A-black	503	SV1.25-3
	3	PE	JL15A-YG	PE	SV1.25-3
	4	501	JL15B-brown	501	SV1.25-3
	5	504	JL15B-black	504	SV1.25-3
	6	PE	JL15B-YG	PE	SV1.25-3

Branch cable of car top JL16					
Plug-in unit of car top	Pin No.	Drawing wire mark	Cables color and wire mark	Drawing wire mark	U shaped terminal types
J16 AMP 1-480700-0	1	101	JL16-brown	101	SV1.25-3
	2	102	JL16-black	102	SV1.25-3
	3	PE	JL16-YG	PE	SV1.25-3

Notes:YG--Yellow&Green.

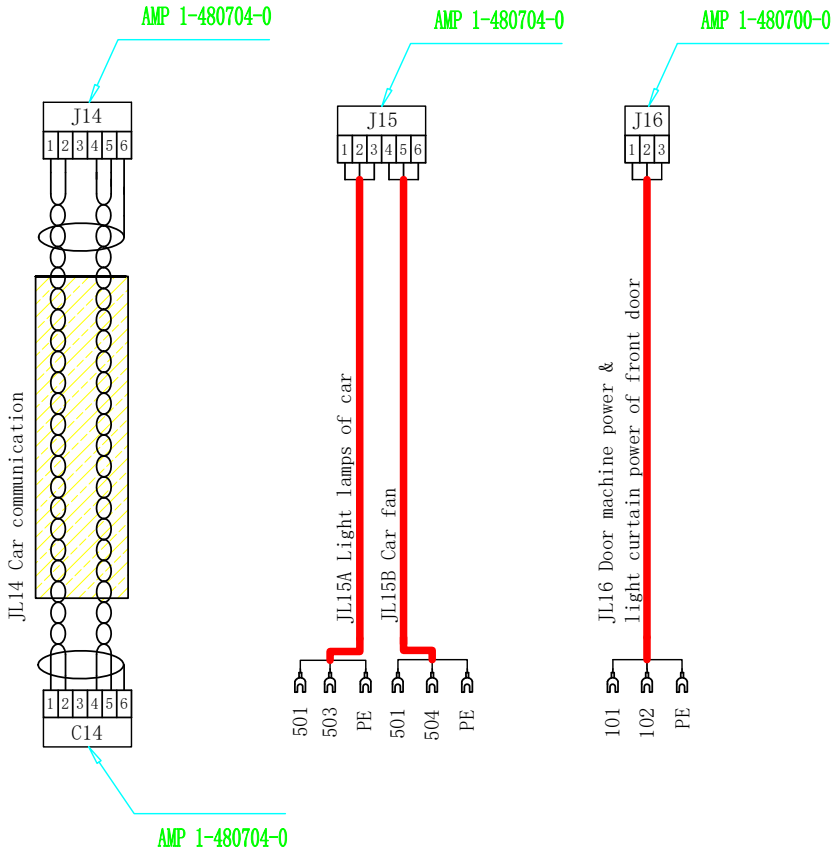

SRH		Sicher Elevator CO., LTD			
GR31423AA-DL01. EN		Branch Cable of Car Top (JL14, JL15A/B, JL16)			
Design	XinfengLuo	Check	JianxueShen	Page	8A
Standardize	GuopingZhou	Approve	XiaoyingRu	Date	07/10/2021

D

C

B

A

D

C

B

A

Branch cable of car top JL17A/B(Single door)

Plug-in unit of car top	Pin No.	Drawing wire mark	Cables' color and wire mark	Drawing wire mark	U shaped terminal types
J17 AMP 1-480704-0	1	14	JL17A-brown	14	SV1.25-3
	2	15	JL17A-black	15	SV1.25-3
	3	PE	JL17A-YG	PE	SV1.25-3
	4	A12	JL17B-brown	A12	SV1.25-3
	5	A13	JL17B-black	A13	SV1.25-3
	6	PE	JL17B-YG	PE	SV1.25-3


Branch cable of car top JL18A/B/C(Double door)

Plug-in unit of car top	Pin No.	Drawing wire mark	Cables' color and wire mark	Drawing wire mark	U shaped terminal types
J18 AMP 1-480706-0	1	14	JL18A-brown	14	SV1.25-3
	2	15	JL18A-black	15	SV1.25-3
	3	PE	JL18A-YG	PE	SV1.25-3
	4	18	JL18B-brown	18	SV1.25-3
	5	19	JL18B-black	19	SV1.25-3
	6	PE	JL18B-YG	PE	SV1.25-3
	7	A12	JL18C-brown	A12	SV1.25-3
	8	A13	JL18C-black	A13	SV1.25-3
	9	PE	JL18C-YG	PE	SV1.25-3

Branch cable of car top JL19A/B(Double door)

Plug-in unit of car top	Pin No.	Drawing wire mark	Cables' color and wire mark	Drawing wire mark	U shaped terminal types
J19 AMP 1-480702-0	1	MSJ2	JL19A-black	MSJ	SV1.25-3
	2	MSJH2	JL19A-brown	MSJH2	SV1.25-3
	3	MSJH2	JL19B-black	MSJH2	SV1.25-3
	4	S06	JL19B-brown	S06	SV1.25-3

Notes:YG--Yellow&Green.

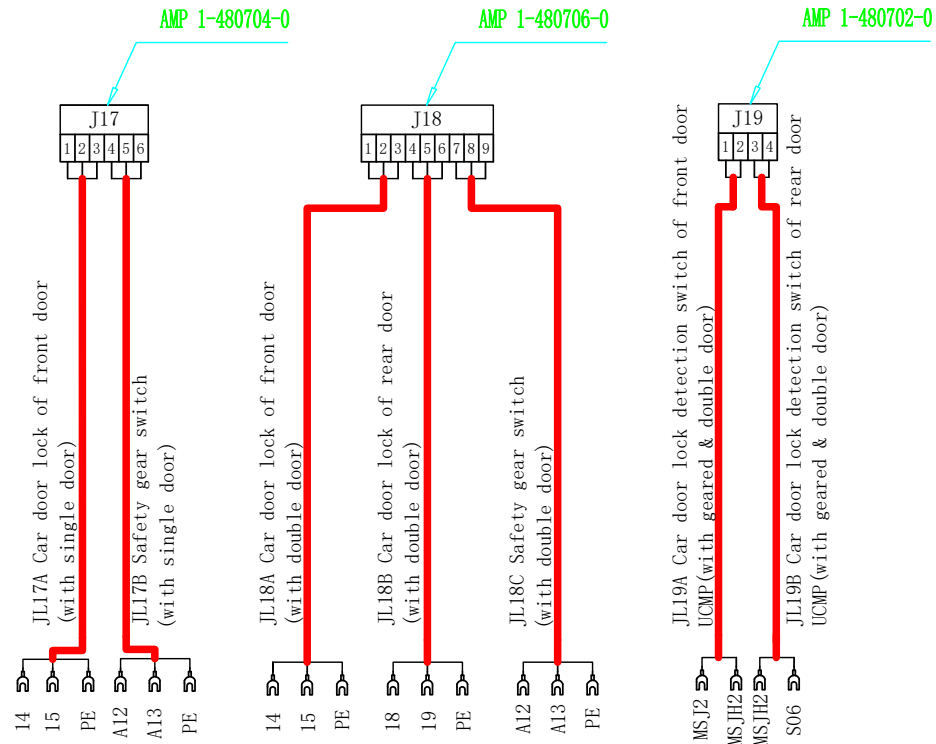

SRH		Sicher Elevator CO., LTD			
GR31423AA-DL01. EN		Branch Cables of Car Top(JL17A/B, JL18A/B/C, JL19A/B)			
Design	XinfengLuo	Check	JianxueShen	Page	8B
Standardize	GuopingZhou	Approve	XiaoyingRu	Date	07/10/2021

D

C

B

A

D

C

B


A

Branch cable of car top JL20(Double door)					
Plug-in unit of car top	Pin No.	Drawing wire mark	Cables' color and wire mark	Drawing wire mark	U shaped terminal types
J20 AMP 1-480700-0	1	101	JL20-brown	101	SV1.25-3
	2	102	JL20-black	102	SV1.25-3
	3	PE	JL20-YG	PE	SV1.25-3

Branch cable of car top JL21A/B					
Plug-in unit of car top	Pin No.	Drawing wire mark	Cables' color and wire mark	Drawing wire mark	U shaped terminal types
J21 AMP 1-480704-0	1	A14	JL21A-brown	A14	SV1.25-3
	2	A15	JL21A-black	A15	SV1.25-3
	3	PE	JL21A-YG	PE	SV1.25-3
	4				
	5	MSJ2	JL21B-brown	MSJ2	SV1.25-3
	6	S06	JL21B-black	S06	SV1.25-3

Branch cable of car top JL22A/B					
Plug-in unit of car top	Pin No.	Drawing wire mark	Cables' color and wire mark	Drawing wire mark	U shaped terminal types
J22 AMP 1-480706-0	1	M6	JL22A-black-1	M6	VE040009
	2	M8	JL22A-black-2	M8	VE040009
	3	M9	JL22A-black-3	M9	VE040009
	4	26	JL22A-black-4	26	VE040009
	5	27	JL22A-black-5	27	VE040009
	6	202	JL22A-black-6	202	VE040009
	7	AP	JL22B-brown	AP	VE040009
	8	202	JL22B-black	202	VE040009
	9				

Notes:YG--Yellow&Green.

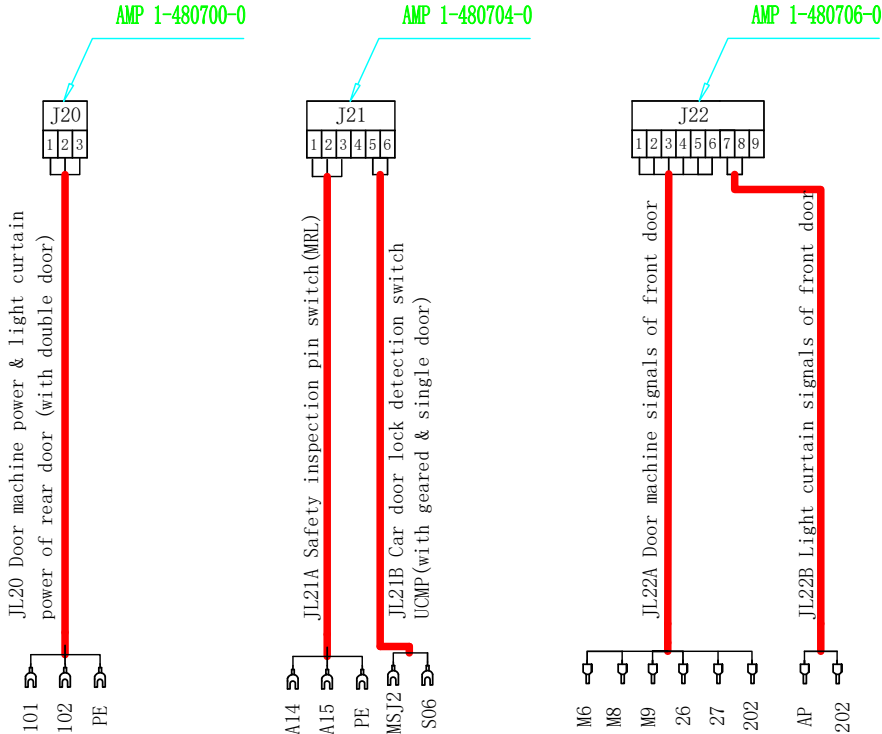

SRH		Sicher Elevator CO., LTD			
GR31423AA-DL01. EN		Branch Cable of Car Top(JL20, JL21A/B, JL22A/B)			
Design	XinfengLuo	Check	JianxueShen	Page	8C
Standardize	GuopingZhou	Approve	XiaoyingRu	Date	07/10/2021

D

C

B

A

D

C

B

A

1

2

3

4

1

2

3

4

Branch cable of car top JL23

Plug-in unit of car top	Pin No.	Drawing wire mark	Cables' color and wire mark	Drawing wire mark	U shaped terminal types	
J23 AMP 1-480706-0	1	202	JL23-black-1	202	SV1.25-3	
	2	MQS	JL23-black-2	MQS	SV1.25-3	
	3	MQX	JL23-black-3	MQX	SV1.25-3	
	4	PS	JL23-black-4	PS	SV1.25-3	
	5	PX	JL23-black-5	PX	SV1.25-3	
	6	201	JL23-black-6	201	SV1.25-3	
	7					
	8					
	9					


Branch cable of car top JL23A

Plug-in unit of car top	Pin No.	Drawing wire mark	Cables' color and wire mark	Drawing wire mark	U shaped terminal types	
J23 AMP 1-480706-0	1	202	JL23A-brown	202	SV1.25-3	
	2	MQS	JL23A-black	MQS	SV1.25-3	
	3					
	4					
	5					
	6	201	JL23A-grey	201	SV1.25-3	
	7					
	8					
	9					


Branch cable of car top JL24A/B

Plug-in unit of car top	Pin No.	Drawing wire mark	Cables' color and wire mark	Drawing wire mark	U shaped terminal types	
J24 AMP 1-480704-0	1	202	JL24A-brown	202	SV1.25-3	
	2	CZ	JL24A-black	CZ	SV1.25-3	
	3	MZ	JL24A-grey	MZ	SV1.25-3	
	4					
	5	EM	JL24B-brown	EM	1	AMP
	6	201	JL24B-black	201	2	1-480700-0


AMP 1-480706-0

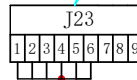


JL23 Door zone

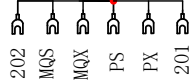

AMP 1-480706-0

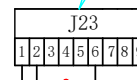

JL23A Door zone (non UCMP)

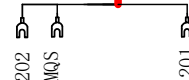

AMP 1-480704-0



JL24A Digital weigh device of car bottom (for passenger lift)

JL24B Acoustooptic alarming device



AMP 1-480700-0

SRH

Sicher Elevator CO., LTD

GR31423AA-DL01. EN		Branch Cable of Car Top(JL23, JL23A, JL24A/B)			
Design	XinfengLuo	Check	JianxueShen	Page	8D
Standardize	GuopingZhou	Approve	XiaoyingRu	Date	07/10/2021

D

D

C

C

B


B

A

A

Branch cable of operation box CL15A/B						
(Wiht auxiliary operation box /Non auxiliary operation box & with disability operation box (with car display))						
Plug-in unit of auxiliary operation box	Pin No.	Drawing wire mark	Cables' color and wire mark	Drawing wire mark	Pin No.	Plug-in unit of main operation box
FC15 AMP 1-480706-0	1	24V	CL15A-white-1	24V	1	C15 AMP 1-480706-0
	2	COM	CL15A-white-2	COM	2	
	3				3	
	4	MOD+	CL15A-white-3	MOD+	4	
	5	MOD-	CL15A-white-4	MOD-	5	
	6	PE1	Shielding Layer	PE1	6	
	7				7	
	8	EB1	CL15B-black	EB1	8	
	9	EB2	CL15B-brown	EB2	9	

Branch cable of operation box CL16				
(With disability operation box (non car display))				
U shaped terminal types	Drawing wire mark	Cables' color and wire mark	Drawing wire mark	U shaped terminal types
SV1.25-3	EB1	CL16-black	EB1	SV1.25-3
	EB2	CL16-brown	EB2	

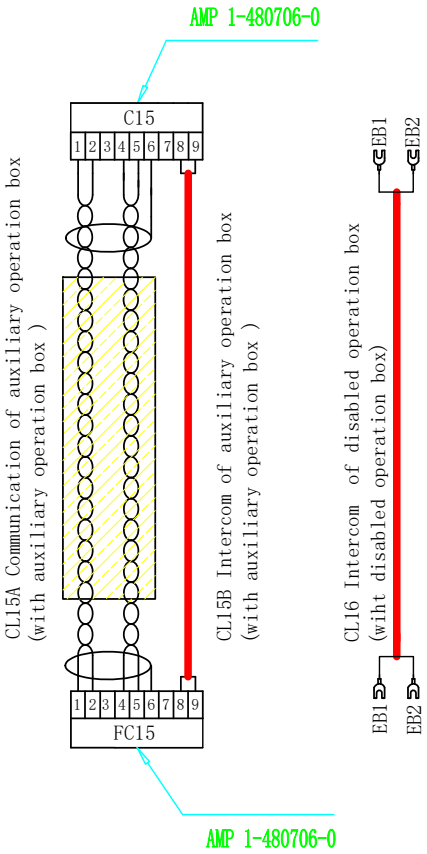

SRH		Sicher Elevator CO., LTD			
GR31423AA-DL01. EN		Branch cable of car (CL15A/B, CL16)			
Design	XinfengLuo	Check	JianxueShen	Page	9
Standardize	GuopingZhou	Approve	XiaoyingRu	Date	07/10/2021

D

C

B

A

D


C

B

A

Shaft cable L1A,Machine room cable FL16A (Single door)						
Plug-in unit of control cabinet	Pin No.	Drawing wire mark	Cables' color and wire mark	Drawing wire mark	Pin No.	Plug-in unit of pit
K5 AMP 1-480708-0	1	A04	L1A-black-1	A04	1	DK5 AMP 1-480706-0
	2	A07	L1A-black-2	A07	2	
	3	A10	L1A-black-3	A08	3	
	4	16	L1A-black-4	16	4	
	5	17	L1A-black-5	17	5	
	6				6	
	7				7	
	8	500	L1A-black-6	500	8	
	9	PE	L1A-YG	PE	9	
	10				10	
	11	X13	FL16A-brown	X13	11	SV1. 25-3
	12	501	FL16A-black	501	12	SV1. 25-3
MR						

Notes:YG--Yellow&Green.

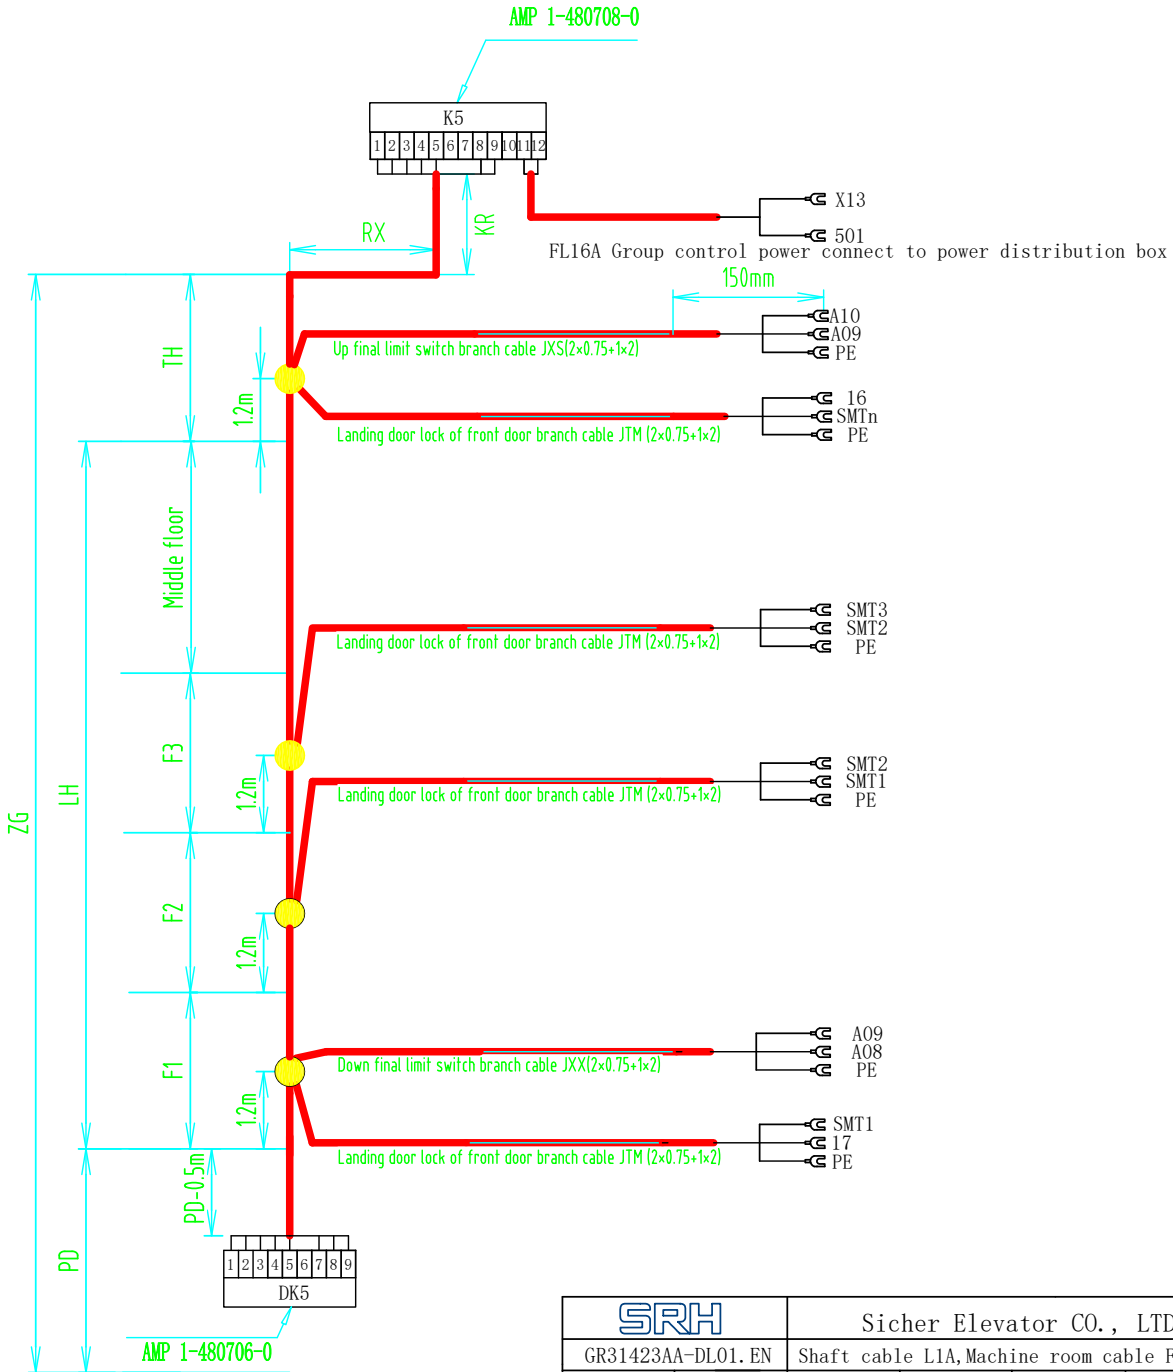

SRH		Sicher Elevator CO., LTD			
GR31423AA-DL01.EN		Shaft cable L1A,Machine room cable FL16A			
Design	XinfengLuo	Check	JianxueShen	Page	10
Standardize	GuopingZhou	Approve	XiaoyingRu	Date	07/10/2021

D

C

B

A

D

C


B

A

Shaft cable L1B,Machine room cable FL16A (Double door)					
Plug-in unit of control cabinet	Pin No.	Drawing wire mark	Cables color and wire mark	Drawing wire mark	Pin No.
K5 AMP 1-480708-0	1	A04	L1B-black-1	A04	1
	2	A07	L1B-black-2	A07	2
	3	A10	L1B-black-3	A08	3
	4	16	L1B-black-4	16	4
	5	17	L1B-black-5	17	5
	6	18	L1B-black-6	18	6
	7				7
	8	500	L1B-black-7	500	8
	9	PE	L1B-YG	PE	9
	10				10
	11	X13	FL16A-brown	X13	11
	12	501	FL16A-black	501	12
MR					

Notes:YG--Yellow&Green.

Notes2: If the rear door control exists,add the branch cables of rear door lock,the specification is 2*0.75+1*2,and if the opposite door in other floor exists,add the branch cables like the 1st floor, the naming method of marks in sequence is SMTH 1~SMTH n(the numbers like before).

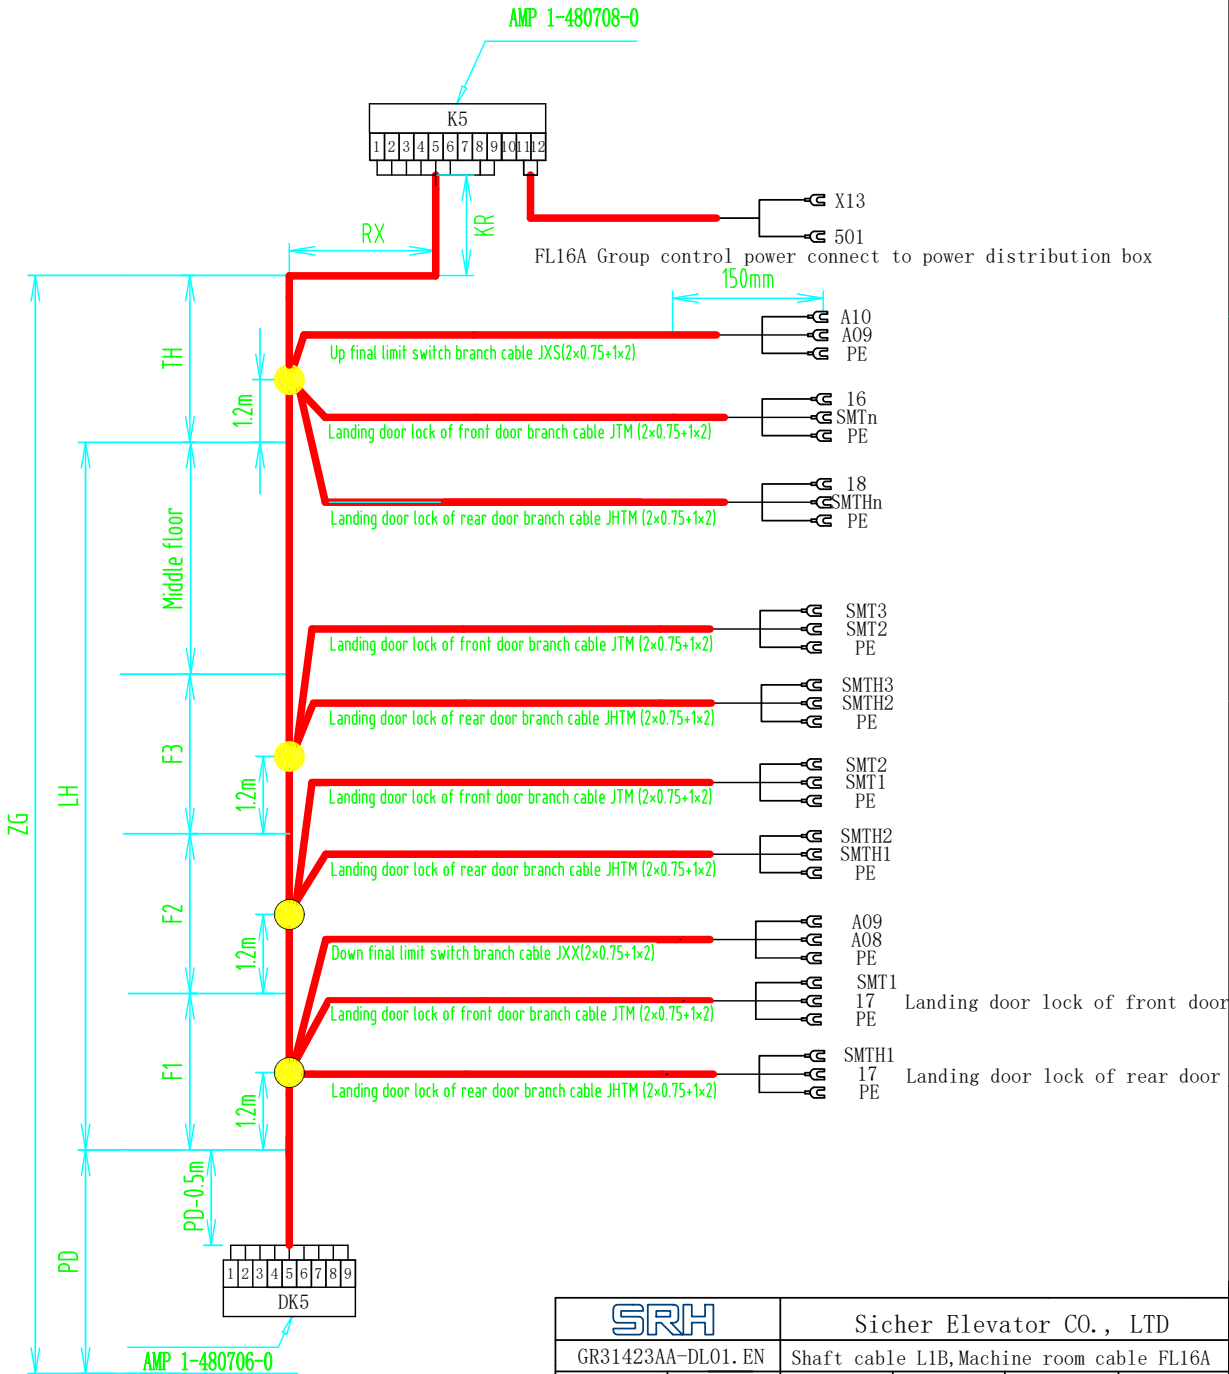

SRH		Sicher Elevator CO., LTD			
GR31423AA-DL01.EN		Shaft cable L1B,Machine room cable FL16A			
Design	XinfengLuo	Check	JianxueShen	Page	10A
Standardize	GuopingZhou	Approve	XiaoyingRu	Date	07/10/2021

D

C

B

A


D

C

B

A

Shaft cable L2A, Machine room cable FL17, FL9							
Plug-in unit of control cabinet	Pin No.	Drawing wire mark	Cables color and wire mark	Drawing wire mark	Pin No.	Plug-in unit of pit	
K6 AMP 1-480708-0	1	501	L2A-brown	501	1	DK6 AMP 1-480704-0	
	2	702	L2A-black	702	2		
	3	704	L2A-grey	704	3		
	4	705	L2A-blue	705	4		
	5				5		
	6				6		
	7	501	FL17-brown	501	7	SV1. 25-3	
	8	GS	FL17-black	GS	8	SV1. 25-3	
	9	L1	FL9-brown	L1	9	SV1. 25-3	
	10	L2	FL9-black	L2	10	SV1. 25-3	
	11	L3	FL9-grey	L3	11	SV1. 25-3	
	12	201	FL9-blue	201	12	SV1. 25-3	
MR							

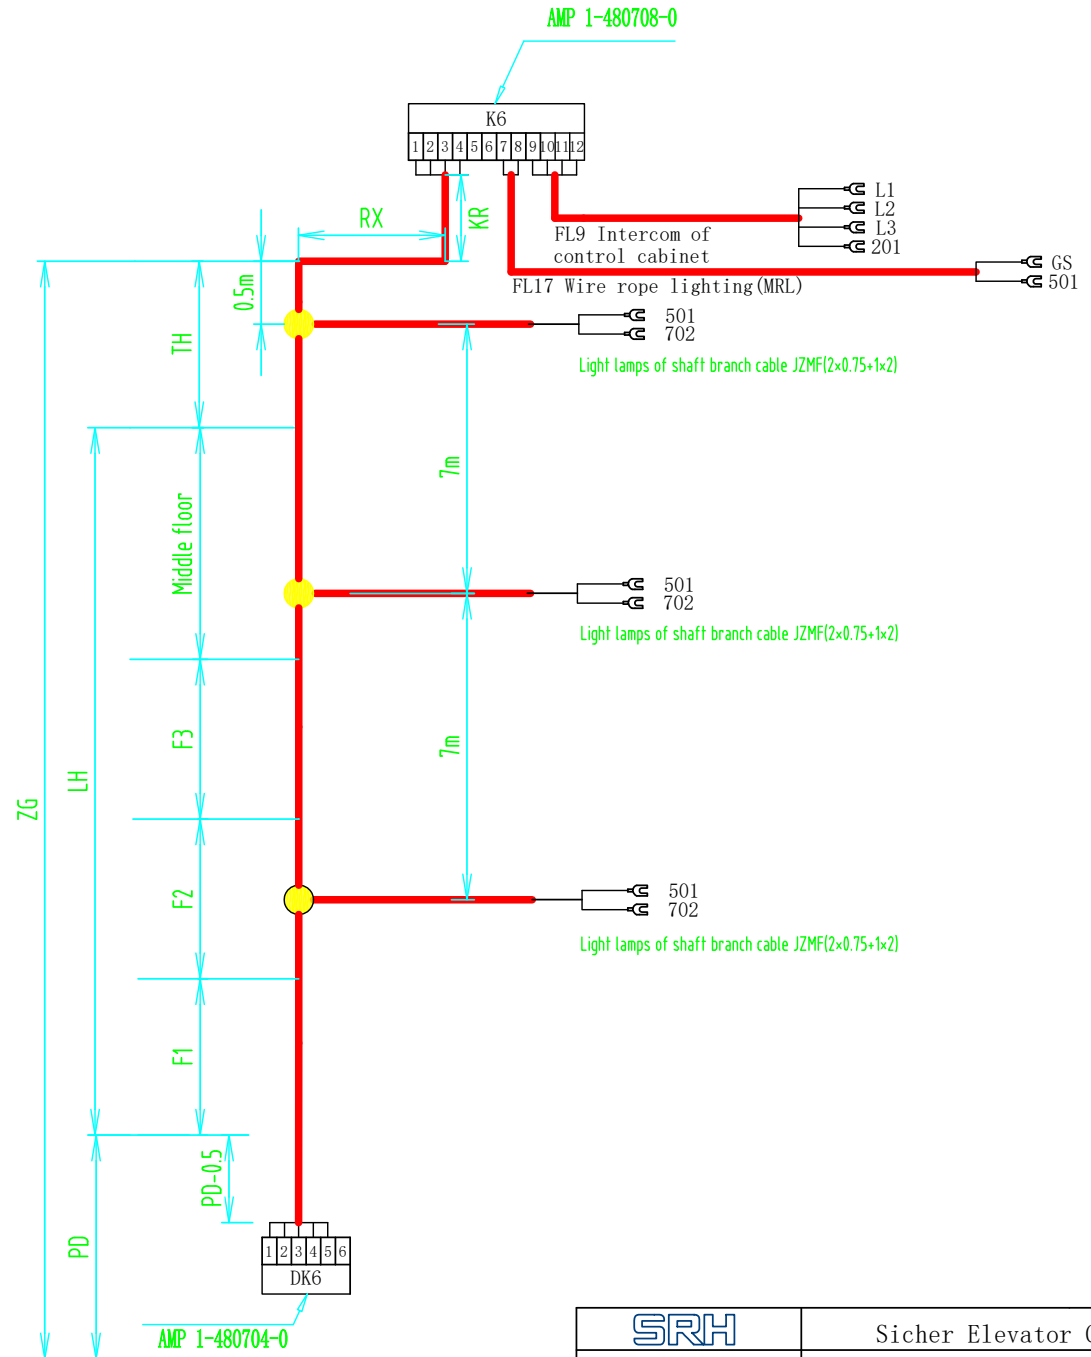

SRH		Sicher Elevator CO., LTD			
GR31423AA-DL01. EN		Shaft cable L2A, Machine room cable FL17, FL9			
Design	XinfengLuo	Check	JianxueShen	Page	10B
Standardize	GuopingZhou	Approve	XiaoyingRu	Date	07/10/2021

D

C

B

A

D

C


B

A

Shaft cable L3A,Machine room cable FL12A (Gearless)						
Plug-in unit of control cabinet	Pin No.	Drawing wire mark	Cables color and wire mark	Drawing wire mark	Pin No.	U shaped terminal types
K7 AMP 1-480708-0	1	L1	L3A-brown	L1	1	SV1.25-3
	2	L2	L3A-black	L2	2	SV1.25-3
	3	L3	L3A-grey	L3	3	SV1.25-3
	4	201	L3A-blue	201	4	SV1.25-3
	5				5	
	6				6	
	7				7	
	8	A11	FL12A-black	A11	8	SV1.25-3
	9	A12	FL12A-brown	A12	9	SV1.25-3
	10	PE	FL12A-YG	PE	10	SV1.25-3
	11				11	SV1.25-3
	12				12	SV1.25-3
MR						

Shaft cable L3A,Machine room cable FL12B (Geared)						
Plug-in unit of control cabinet	Pin No.	Drawing wire mark	Cables color and wire mark	Drawing wire mark	Pin No.	U shaped terminal types
K7 AMP 1-480708-0	1	L1	L3A-brown	L1	1	SV1.25-3
	2	L2	L3A-black	L2	2	SV1.25-3
	3	L3	L3A-grey	L3	3	SV1.25-3
	4	201	L3A-blue	201	4	SV1.25-3
	5				5	
	6	101	FL12B-black	101	6	SV1.25-3
	7	102	FL12B-brown	102	7	SV1.25-3
	8	A11	FL12B-grey	A11	8	SV1.25-3
	9	A12	FL12B-blue	A12	9	SV1.25-3
	10	PE	FL12B-YG	PE	10	SV1.25-3
	11				11	SV1.25-3
	12				12	SV1.25-3
MR						

Notes:YG--Yellow&Green.

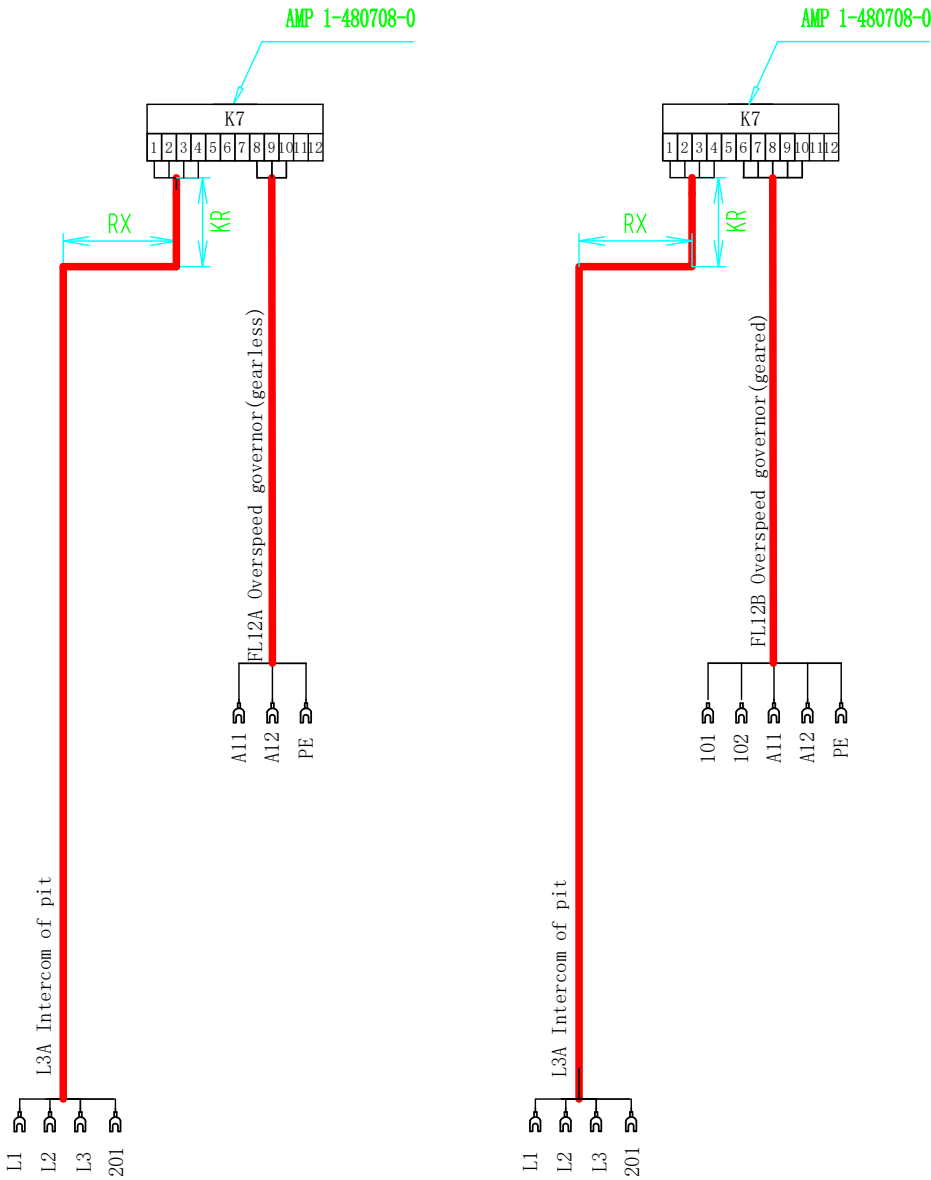

SRH		Sicher Elevator CO., LTD			
GR31423AA-DL01.EN		Shaft Cable(L3A),Machine room cable(FL12A/B)			
Design	XinfengLuo	Check	JianxueShen	Page	10C
Standardize	GuopingZhou	Approve	XiaoyingRu	Date	07/10/2021

D

C

B

A

D

C


B

A

Shaft cable L4A,Machine room cable FL15A						
Plug-in unit of control cabinet	Pin No.	Drawing wire mark	Cables' color and wire mark	Drawing wire mark	Pin No.	U shaped terminal types
K8 AMP 1-480708-0	1	202	L4A-brown	202	1	SV1. 25-3
	2	WS	L4A-black	WS	2	
	3	WX	L4A-grey	WX	3	
	4				4	
	5				5	
	6	PE	L4A-YG	PE	6	
	7				7	
	8				8	
	9	202	FL15A-brown	202	9	
	10	NC	FL15A-black	NC	10	
	11	CS1	FL15A-grey	CS1	11	
	12	S06	FL15A-blue	S06	12	
MR						

Shaft cable L4B,Machine room cable FL15A						
Plug-in unit of control cabinet	Pin No.	Drawing wire mark	Cables' color and wire mark	Drawing wire mark	Pin No.	U shaped terminal types
K8 AMP 1-480708-0	1	202	L4B-black-1	202	1	SV1. 25-3
	2	WS	L4B-black-2	WS	2	
	3	WX	L4B-black-3	WX	3	
	4	W2S	L4B-black-4	W2S	4	
	5	W2X	L4B-black-5	W2X	5	
	6	PE	L4B-YG	PE	6	
	7				7	
	8				8	
	9	202	FL15A-brown	202	9	
	10	NC	FL15A-black	NC	10	
	11	CS1	FL15A-grey	CS1	11	
	12	S06	FL15A-blue	S06	12	
MR						

Notes: YG--Yellow&Green.

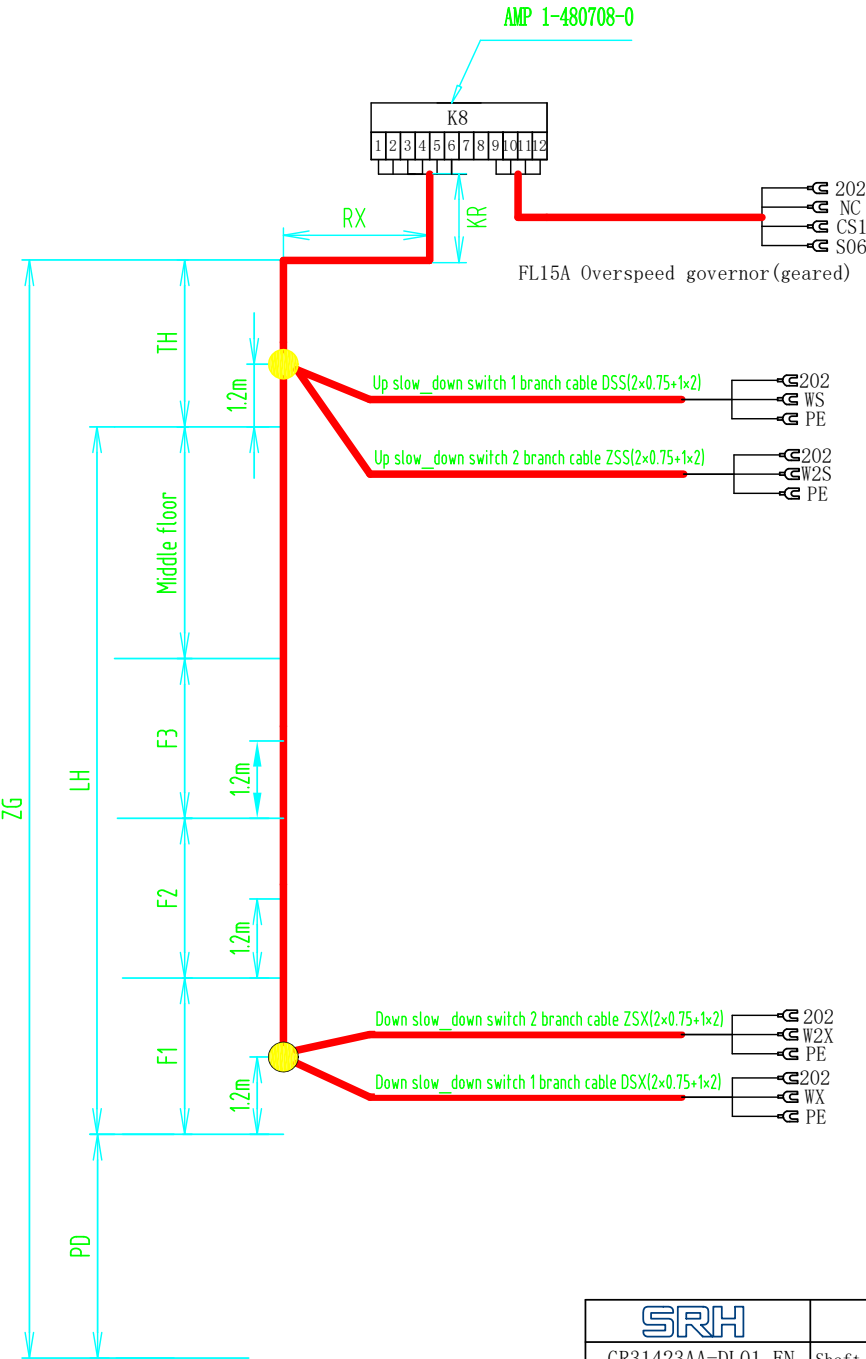

SRH		Sicher Elevator CO., LTD			
GR31423AA-DL01. EN		Shaft cable (L4A/B), Machine room cable (FL15A)			
Design	XinfengLuo	Check	JianxueShen	Page	10D
Standardize	GuopingZhou	Approve	XiaoyingRu	Date	07/10/2021

D

C

B

A

D

C

B

A

1




2

3

4

Shaft cable L5A

Plug-in unit of control cabinet	Pin No.	Drawing wire mark	Cables color and wire mark	Drawing wire mark	Plug-in unit of each floor and grounding
K9 AMP 1-480704-0	1	202	L5A-white-1	202	Plug-in of communication port of matched landing calling board
	2	201	L5A-white-2	201	
	3				
	4	MOD+	L5A-white-3	MOD+	
	5	MOD-	L5A-white-4	MOD-	
	6	PE1	shielding layer	PE1	
MR					

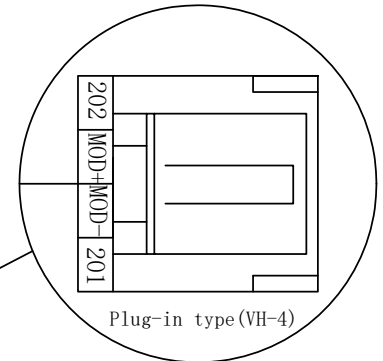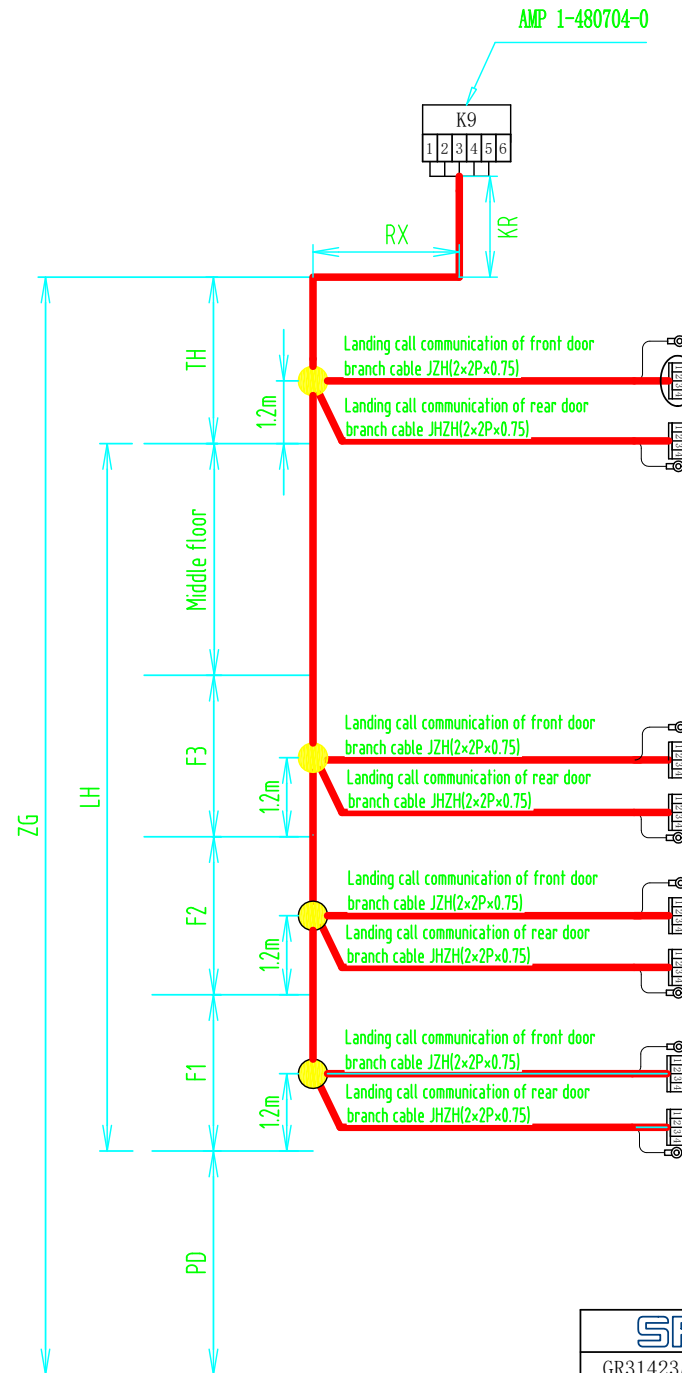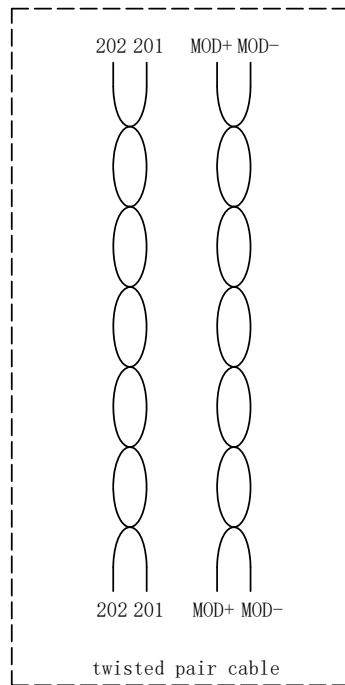

SRH		Sicher Elevator CO., LTD			
GR31423AA-DL01.EN		Shaft Cable (L5A)			
Design	XinfengLuo	Check	JianxueShen	Page	10E
Standardize	GuopingZhou	Approve	XiaoyingRu	Date	07/10/2021

1

2

3

4

D

C

B

A

D

C


B

A

Shaft cable L1D, Machine room cable FL16A (Double door)					
Plug-in unit of control cabinet	Pin No.	Drawing wire mark	Cables color and wire mark	Drawing wire mark	Pin No.
K5 AMP 1-480708-0	1	A04	L1D-black-1	A04	1
	2	A07	L1D-black-2	A07	2
	3	A10	L1D-black-3	A08	3
	4	16	L1D-black-4	16	4
	5	17	L1D-black-5	17	5
	6	18	L1D-black-6	18	6
	7				7
	8	500	L1D-black-7	500	8
	9	PE	L1D-YG	PE	9
	10				10
DK5 AMP 1-480706-0	11	X13	FL16A-brown	X13	11
	12	501	FL16A-black	501	12
MRL					

Notes: YG--Yellow&Green.

Notes2: If the rear door control exists, add the branch cables of rear door lock, the specification is $2 \times 0.75 + 1 \times 2$, and if the opposite door in other floor exists, add the branch cables like the 1st floor, the naming method of marks in sequence is SMTH₁~SMTH_n (the numbers like before).

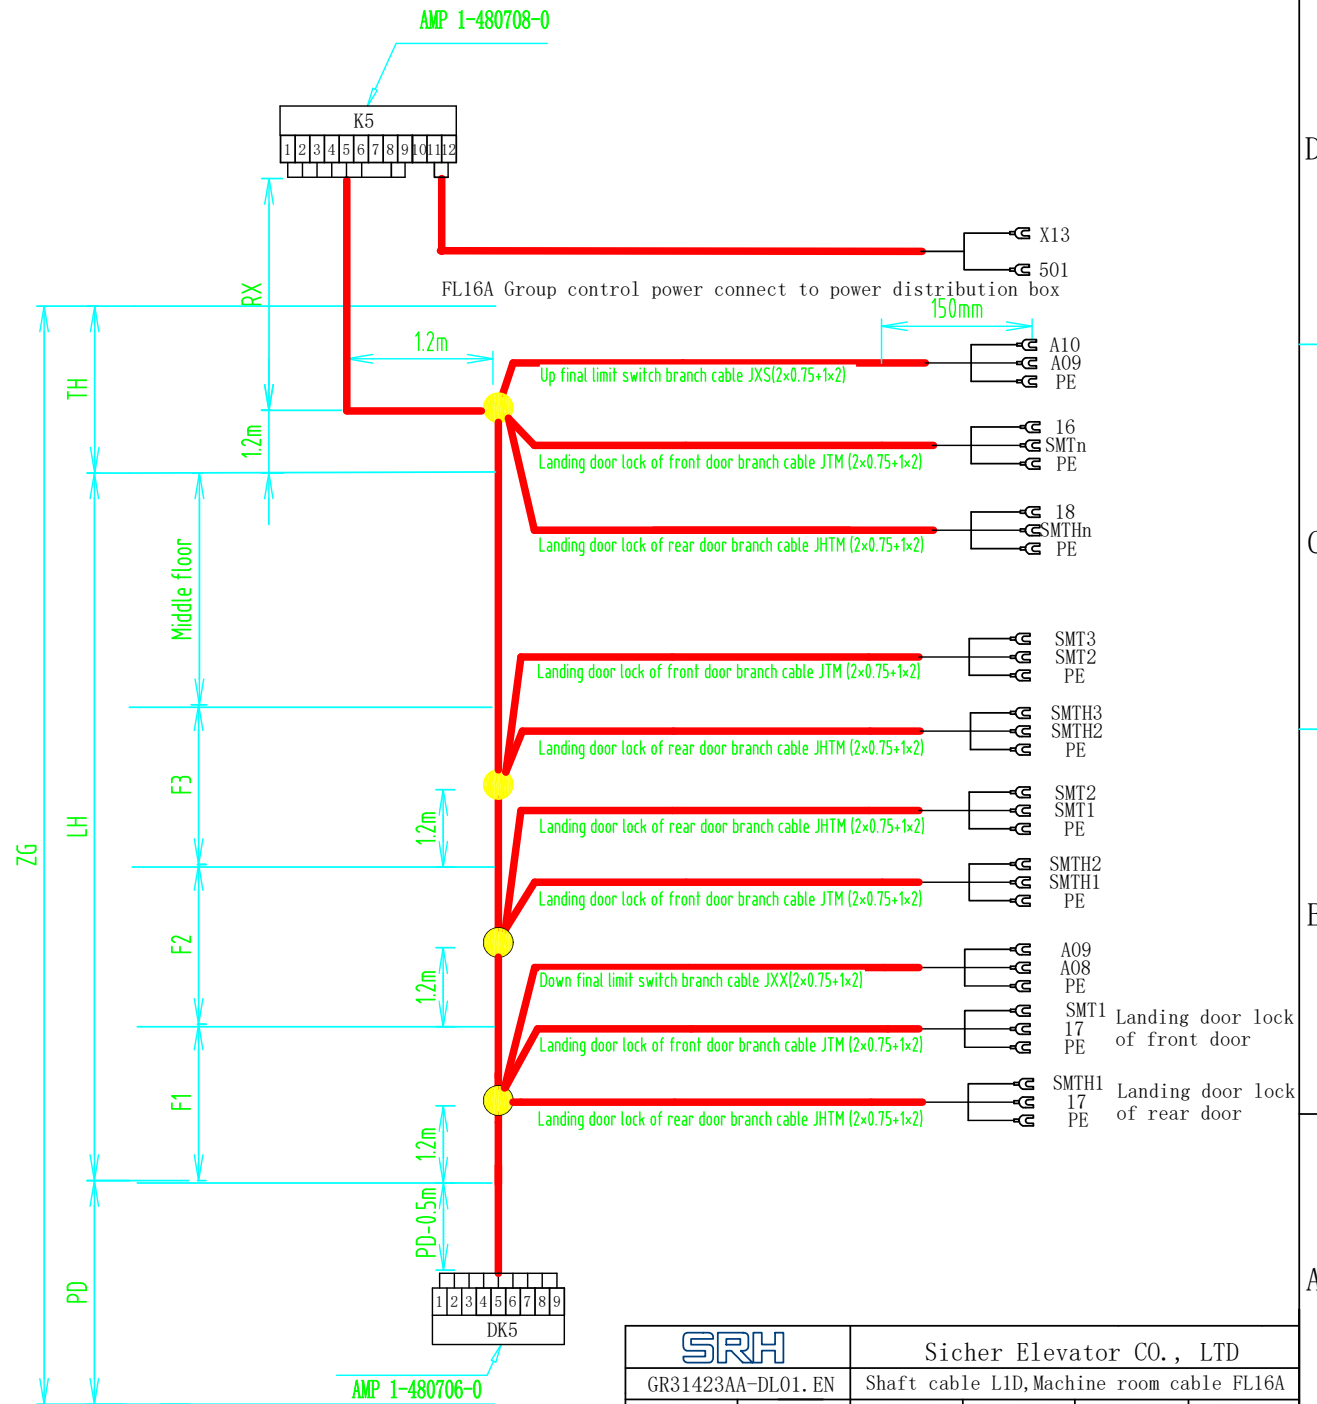

SRH		Sicher Elevator CO., LTD			
GR31423AA-DL01.EN		Shaft cable L1D, Machine room cable FL16A			
Design	XinfengLuo	Check	JianxueShen	Page	10G
Standardize	GuopingZhou	Approve	XiaoyingRu	Date	07/10/2021

D

C

B

A

D


C

B

A

Shaft cable L2B,Machine room cable FL17,FL9						
Plug-in unit of control cabinet	Pin No.	Drawing wire mark	Cables' color and wire mark	Drawing wire mark	Pin No.	Plug-in unit of pit
K6 AMP 1-480708-0	1	501	L2B-brown	501	1	DK6 AMP 1-480704-0
	2	702	L2B-black	702	2	
	3	704	L2B-grey	704	3	
	4	705	L2B-blue	705	4	
	5				5	
	6				6	
	7	501	FL17-brown	501	7	SV1. 25-3
	8	GS	FL17-black	GS	8	SV1. 25-3
	9	L1	FL9-brown	L1	9	SV1. 25-3
	10	L2	FL9-black	L2	10	SV1. 25-3
	11	L3	FL9-grey	L3	11	SV1. 25-3
	12	201	FL9-blue	201	12	SV1. 25-3
MRL						

Notes:YG--Yellow&Green.

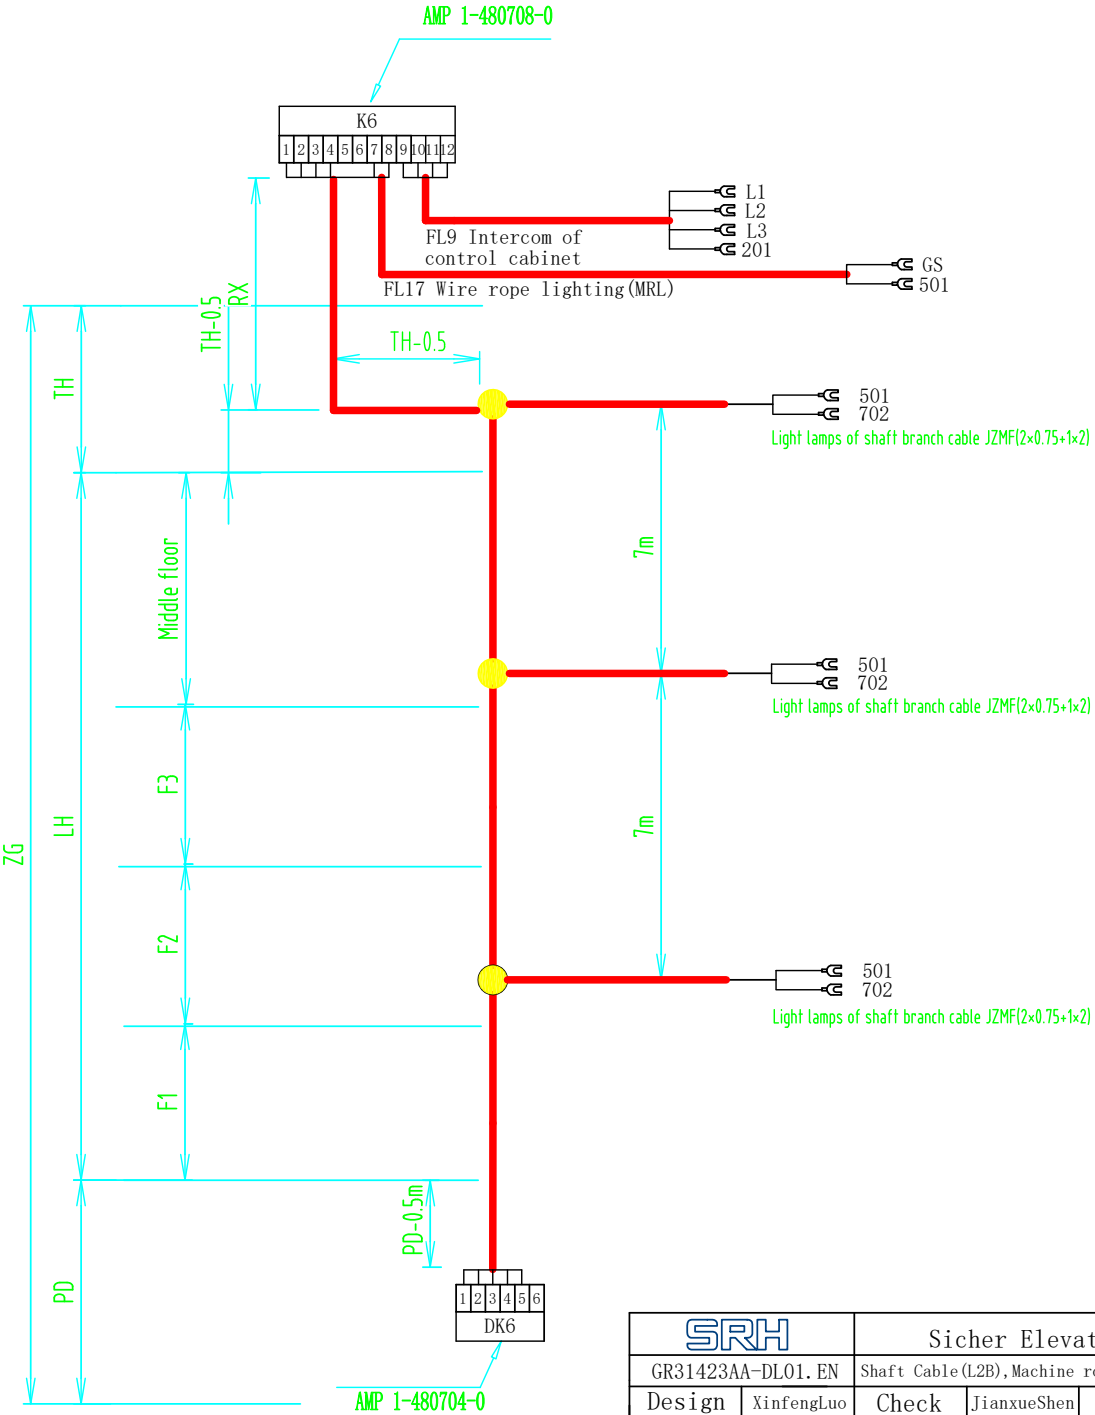

SRH		Sicher Elevator CO., LTD			
GR31423AA-DL01. EN		Shaft Cable (L2B), Machine room cable (FL17, FL9)			
Design	XinfengLuo	Check	JianxueShen	Page	10H
Standardize	GuopingZhou	Approve	XiaoyingRu	Date	07/10/2021

D

C

B

A

D

C

B

A



Shaft cable L3B, Machine room cable FL12A
(Gearless)

Plug-in unit of control cabinet	Pin No.	Drawing wire mark	Cables color and wire mark	Drawing wire mark	Pin No.	U shaped terminal types
K7 AMP 1-480708-0	1	L1	L3B-brown	L1	1	SV1.25-3
	2	L2	L3B-black	L2	2	SV1.25-3
	3	L3	L3B-grey	L3	3	SV1.25-3
	4	201	L3B-blue	201	4	SV1.25-3
	5				5	
	6				6	
	7				7	
	8	A11	FL12A-black	A11	8	SV1.25-3
	9	A12	FL12A-brown	A12	9	SV1.25-3
	10	PE	FL12A-YG	PE	10	SV1.25-3
	11				11	SV1.25-3
	12				12	SV1.25-3
MRL						

Shaft cable L3B, Machine room cable FL12B
(Geared)

Plug-in unit of control cabinet	Pin No.	Drawing wire mark	Cables color and wire mark	Drawing wire mark	Pin No.	U shaped terminal types
K7 AMP 1-480708-0	1	L1	L3B-brown	L1	1	SV1.25-3
	2	L2	L3B-black	L2	2	SV1.25-3
	3	L3	L3B-grey	L3	3	SV1.25-3
	4	201	L3B-blue	201	4	SV1.25-3
	5				5	
	6	101	FL12B-black	101	6	SV1.25-3
	7	102	FL12B-brown	102	7	SV1.25-3
	8	A11	FL12B-grey	A11	8	SV1.25-3
	9	A12	FL12B-blue	A12	9	SV1.25-3
	10	PE	FL12B-YG	PE	10	SV1.25-3
	11				11	SV1.25-3
	12				12	SV1.25-3
MRL						

Notes: YG--Yellow&Green.

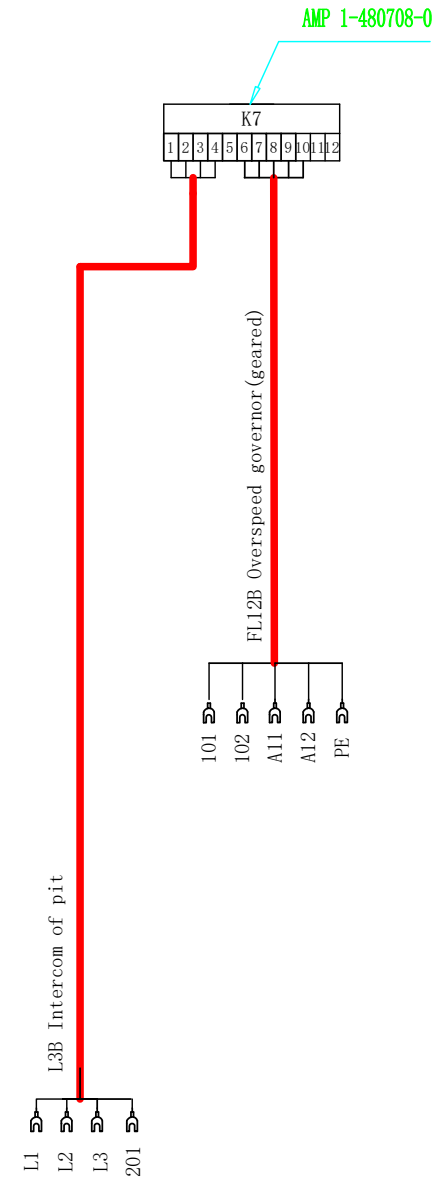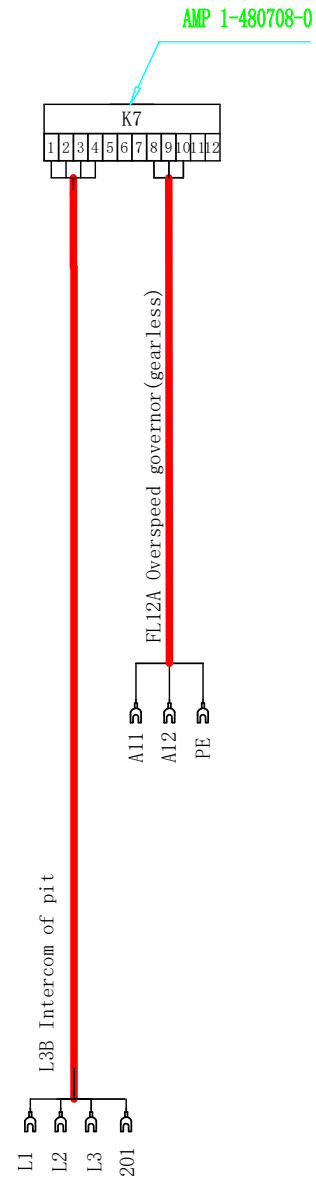

SRH

Sicher Elevator CO., LTD

GR31423AA-DL01. EN		Shaft Cable(L3B), Machine room cable (FL12A/B)			
Design	XinfengLuo	Check	JianxueShen	Page	10I
Standardize	GuopingZhou	Approve	XiaoyingRu	Date	07/10/2021

D

C

B

A

D

C

B

A

Shaft cable L4C, Machine room cable FL15A

Plug-in unit of control cabinet	Pin No.	Drawing wire mark	Cables' color and wire mark	Drawing wire mark	Pin No.	U shaped terminal types
K8 AMP 1-480708-0	1	202	L4C-brown	202	1	SV1. 25-3
	2	WS	L4C-black	WS	2	
	3	WX	L4C-grey	WX	3	
	4				4	
	5				5	
	6	PE	L4C-YG	PE	6	
	7				7	
	8				8	
	9	202	FL15A-brown	202	9	
	10	NC	FL15A-black	NC	10	
	11	CS1	FL15A-grey	CS1	11	
	12	S06	FL15A-blue	S06	12	


MRL

Shaft cable L4D, Machine room cable FL15A

Plug-in unit of control cabinet	Pin No.	Drawing wire mark	Cables' color and wire mark	Drawing wire mark	Pin No.	U shaped terminal types
K8 AMP 1-480708-0	1	202	L4D-black-1	202	1	SV1. 25-3
	2	WS	L4D-black-2	WS	2	
	3	WX	L4D-black-3	WX	3	
	4	W2S	L4D-black-4	W2S	4	
	5	W2X	L4D-black-5	W2X	5	
	6	PE	L4D-YG	PE	6	
	7				7	
	8				8	
	9	202	FL15A-brown	202	9	
	10	NC	FL15A-black	NC	10	
	11	CS1	FL15A-grey	CS1	11	
	12	S06	FL15A-blue	S06	12	



MRL

Notes:YG--Yellow&Green.

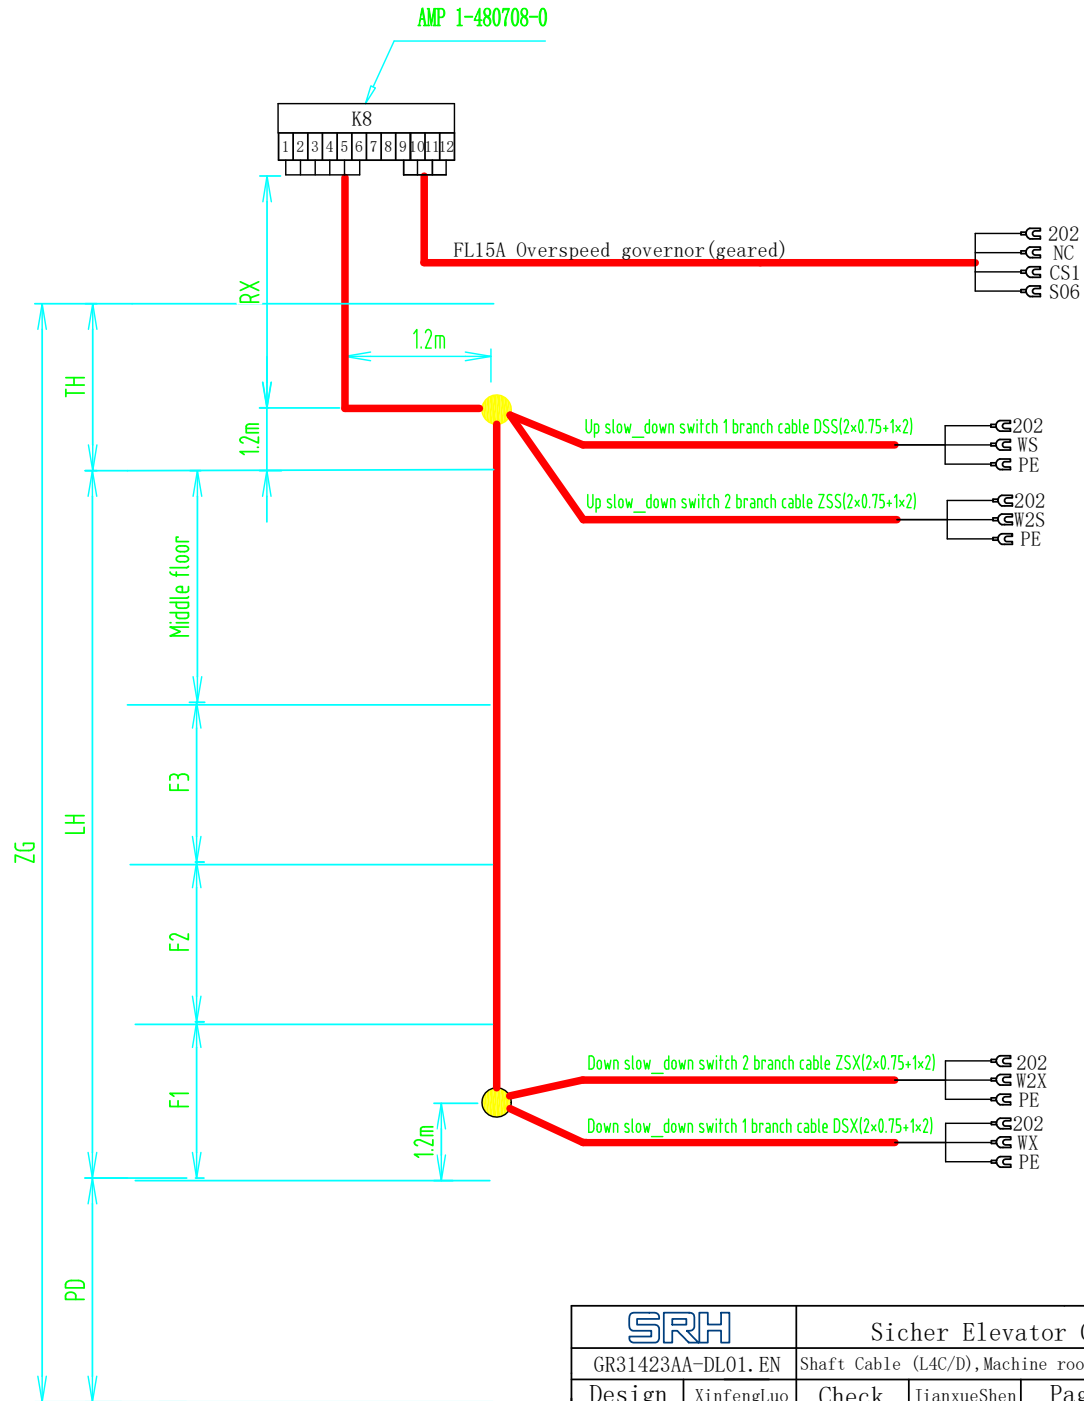

SRH		Sicher Elevator CO., LTD			
GR31423AA-DL01. EN		Shaft Cable (L4C/D), Machine room cable(FL15A)			
Design	XinfengLuo	Check	JianxueShen	Page	10J
Standardize	GuopingZhou	Approve	XiaoyingRu	Date	07/10/2021

Shaft cable L5B					
Plug-in unit of control cabinet	Pin No.	Drawing wire mark	Cables' color and wire mark	Drawing wire mark	Plug-in unit of each floor and grounding
K9 AMP 1-480704-0	1	202	L5B-white-1	202	Plug-in of communication port of matched outside calling board
	2	201	L5B-white-2	201	
	3				
	4	MOD+	L5B-white-3	MOD+	
	5	MOD-	L5B-white-4	MOD-	
	6	PE1	shielding layer	PE1	
MRL					

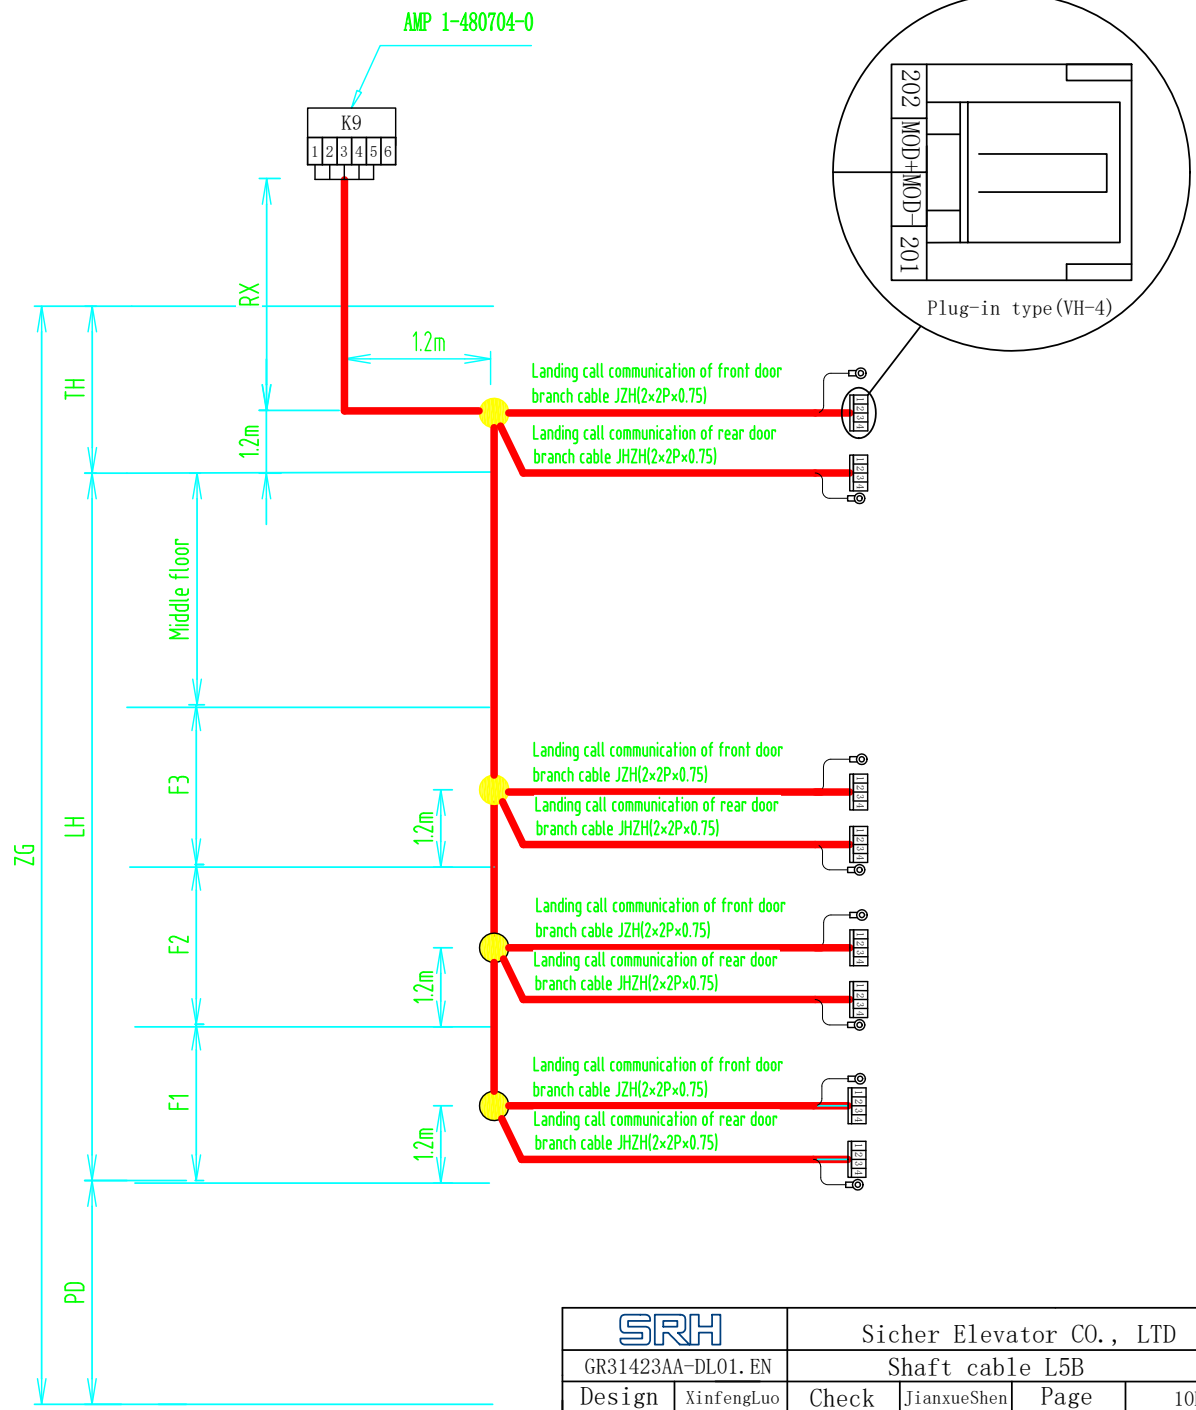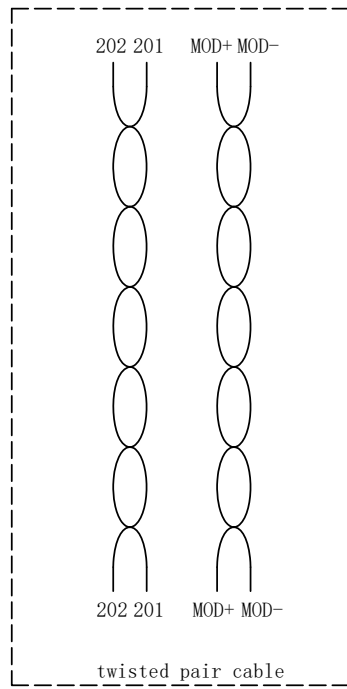

		Sicher Elevator CO., LTD			
GR31423AA-DL01. EN		Shaft cable L5B			
Design	XinfengLuo	Check	JianxueShen	Page	10K
Standardize	GuopingZhou	Approve	XiaoyingRu	Date	07/10/2021

D

C

B

A

D


C

B

A

Machine room cable FL1, FL2, FL3, FL13						
Plug-in unit of control cabinet	Pin No.	Drawing wire mark	Cables color and wire mark	Drawing wire mark	Pin No.	U shaped terminal types
K10 AMP 1-480710-0	1	ZQ1	FL1-brown	ZQ1	1	SV1.25-3
	2	ZQ2	FL1-black	ZQ2	2	SV1.25-3
	3	PE	FL1-YG	PE	3	SV1.25-3
	4	500	FL2-brown	500	4	SV1.25-3
	5	501	FL2-black	501	5	SV1.25-3
	6	704	FL2-grey	704	6	SV1.25-3
	7	705	FL2-blue	705	7	SV1.25-3
	8	PE	FL2-YG	PE	8	SV1.25-3
	9	501	FL3-black	501	9	SV1.25-3
	10	XD	FL3-brown	XD	10	SV1.25-3
	11	XJ	FL3-grey	XJ	11	SV1.25-3
	12	201	FL13-brown	201	12	SV1.25-3
	13	202	FL13-black	202	13	SV1.25-3
	14	CZ	FL13-grey	CZ	14	SV1.25-3
	15	MZ	FL13-blue	MZ	15	SV1.25-3

Notes:YG--Yellow&Green.

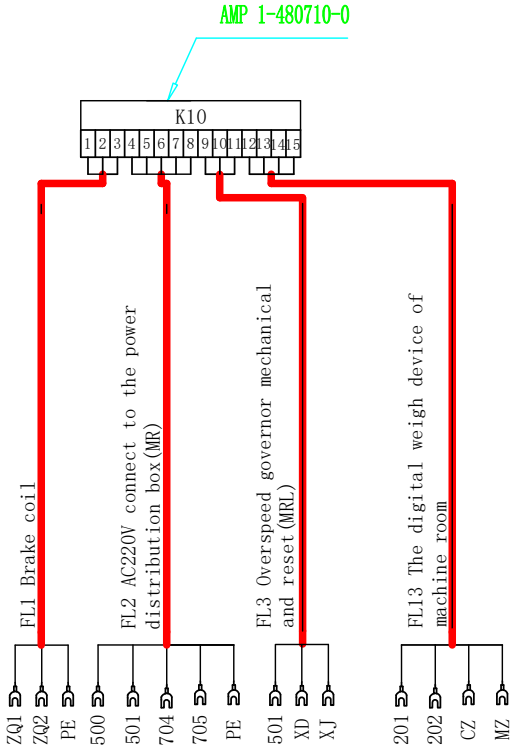

SRH		Sicher Elevator CO., LTD			
GR31423AA-DL01. EN		Machine room cable (FL1, FL2, FL3, FL13)			
Design	XinfengLuo	Check	JianxueShen	Page	11
Standardize	GuopingZhou	Approve	XiaoyingRu	Date	07/10/2021

D

C

B

A

D


C

B

A

Machine room cable FL4, FL5, FL6, FL7, FL14						
Plug-in unit of control cabinet	Pin No.	Drawing wire mark	Cables' color and wire mark	Drawing wire mark	Pin No.	U shaped terminal types
K11 AMP 1-480710-0	1	AD7	FL4-brown	AD7	1	SV1.25-3
	2	AD8	FL4-black	AD8	2	SV1.25-3
	3	202	FL5-brown	202	3	SV1.25-3
	4	TC	FL5-black	TC	4	SV1.25-3
	5	A03	FL6-brown	A03	5	SV1.25-3
	6	A04	FL6-black	A04	6	SV1.25-3
	7	PE	FL6-YG	PE	7	SV1.25-3
	8	A10	FL7-brown	A10	8	SV1.25-3
	9	A11	FL7-black	A11	9	SV1.25-3
	10	PE	FL7-YG	PE	10	SV1.25-3
	11				11	
	12				12	
	13	202	FL14-brown	202	13	SV1.25-3
	14	ZD1	FL14-black	ZD1	14	SV1.25-3
	15	ZD2	FL14-grey	ZD2	15	SV1.25-3

Notes:YG--Yellow&Green.

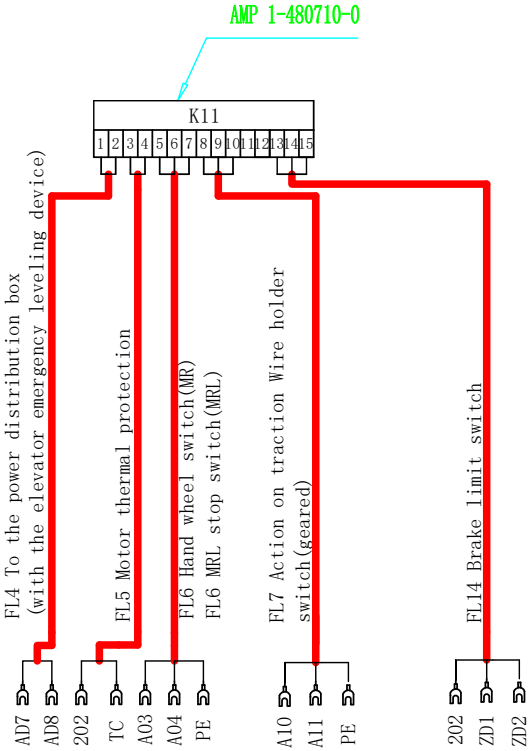

SRH		Sicher Elevator CO., LTD			
GR31423AA-DL01.EN		Machine room cable FL4, FL5, FL6, FL7, FL14			
Design	XinfengLuo	Check	JianxueShen	Page	11A
Standardize	GuopingZhou	Approve	XiaoyingRu	Date	07/10/2021

D

C

B

A

D

C

B

A

1

2

3

4

Branch cable of pit KL1

Plug-in unit of pit	Pin No.	Drawing wire mark	Cables' color and wire mark	Drawing wire mark	U shaped terminal types
DK11 AMP 1-480700-0	1	A07	KL1-brown	A07	SV1.25-3
	2	A08	KL1-black	A08	SV1.25-3
	3	PE	KL1-YG	PE	SV1.25-3

Branch cable of pit KL2

Plug-in unit of pit	Pin No.	Drawing wire mark	Cables' color and wire mark	Drawing wire mark	U shaped terminal types
DK12 AMP 1-480700-0	1	A06	KL2-brown	A06	SV1.25-3
	2	A07	KL2-black	A07	SV1.25-3
	3	PE	KL2-YG	PE	SV1.25-3

Branch cable of pit KL3


Plug-in unit of pit	Pin No.	Drawing wire mark	Cables' color and wire mark	Drawing wire mark	U shaped terminal types
DK13 AMP 1-480700-0	1	A04	KL3-brown	A04	SV1.25-3
	2	A05	KL3-black	A05	SV1.25-3
	3				

Branch cable of pit KL4

Plug-in unit of pit	Pin No.	Drawing wire mark	Cables' color and wire mark	Drawing wire mark	U shaped terminal types
DK14 AMP 1-480700-0	1	704	KL4-brown	704	Insert spring 4.8
	2	705	KL4-black	705	Insert spring 4.8
	3	702	KL4-grey	702	Insert spring 4.8

Branch cable of pit KL5

Plug-in unit of pit	Pin No.	Drawing wire mark	Cables' color and wire mark	Drawing wire mark	U shaped terminal types
DK15 AMP 1-480700-0	1	501	KL5-brown	501	SV1.25-3
	2	702	KL5-grey	702	SV1.25-3
	3				

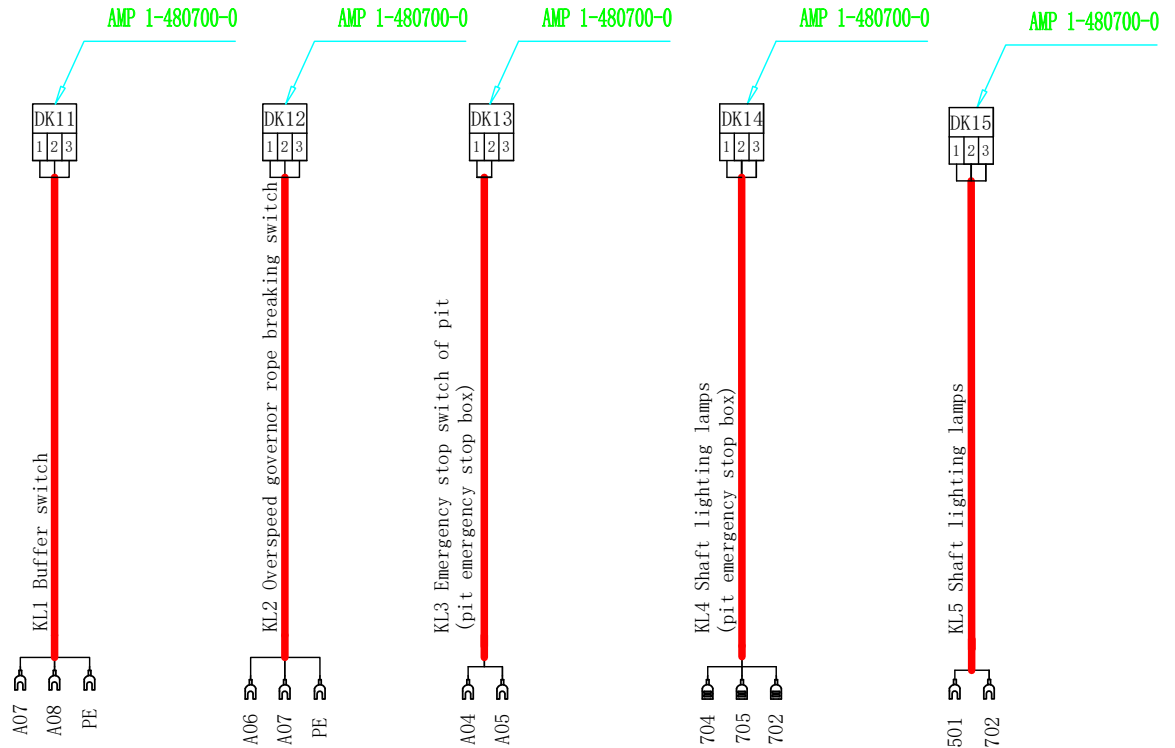

SRH		Sicher Elevator CO., LTD			
GR31423AA-DL01. EN		Branch cable of pit (KL1, KL2, KL3, KL4, KL5)			
Design	XinfengLuo	Check	JianxueShen	Page	12
Standardize	GuopingZhou	Approve	XiaoyingRu	Date	07/10/2021

1

2

3

4